



REV. #


G:\shand drives\Project Drafting\24-4949D ODA Drafting 23-229 Dunkirk Self Storage\Working File\Bldg A\23-229 Dunkirk Self Storage R23_Structure bldg A 2026\106 JC23-229 Dunkirk Self Storage R25_Building A.rvt

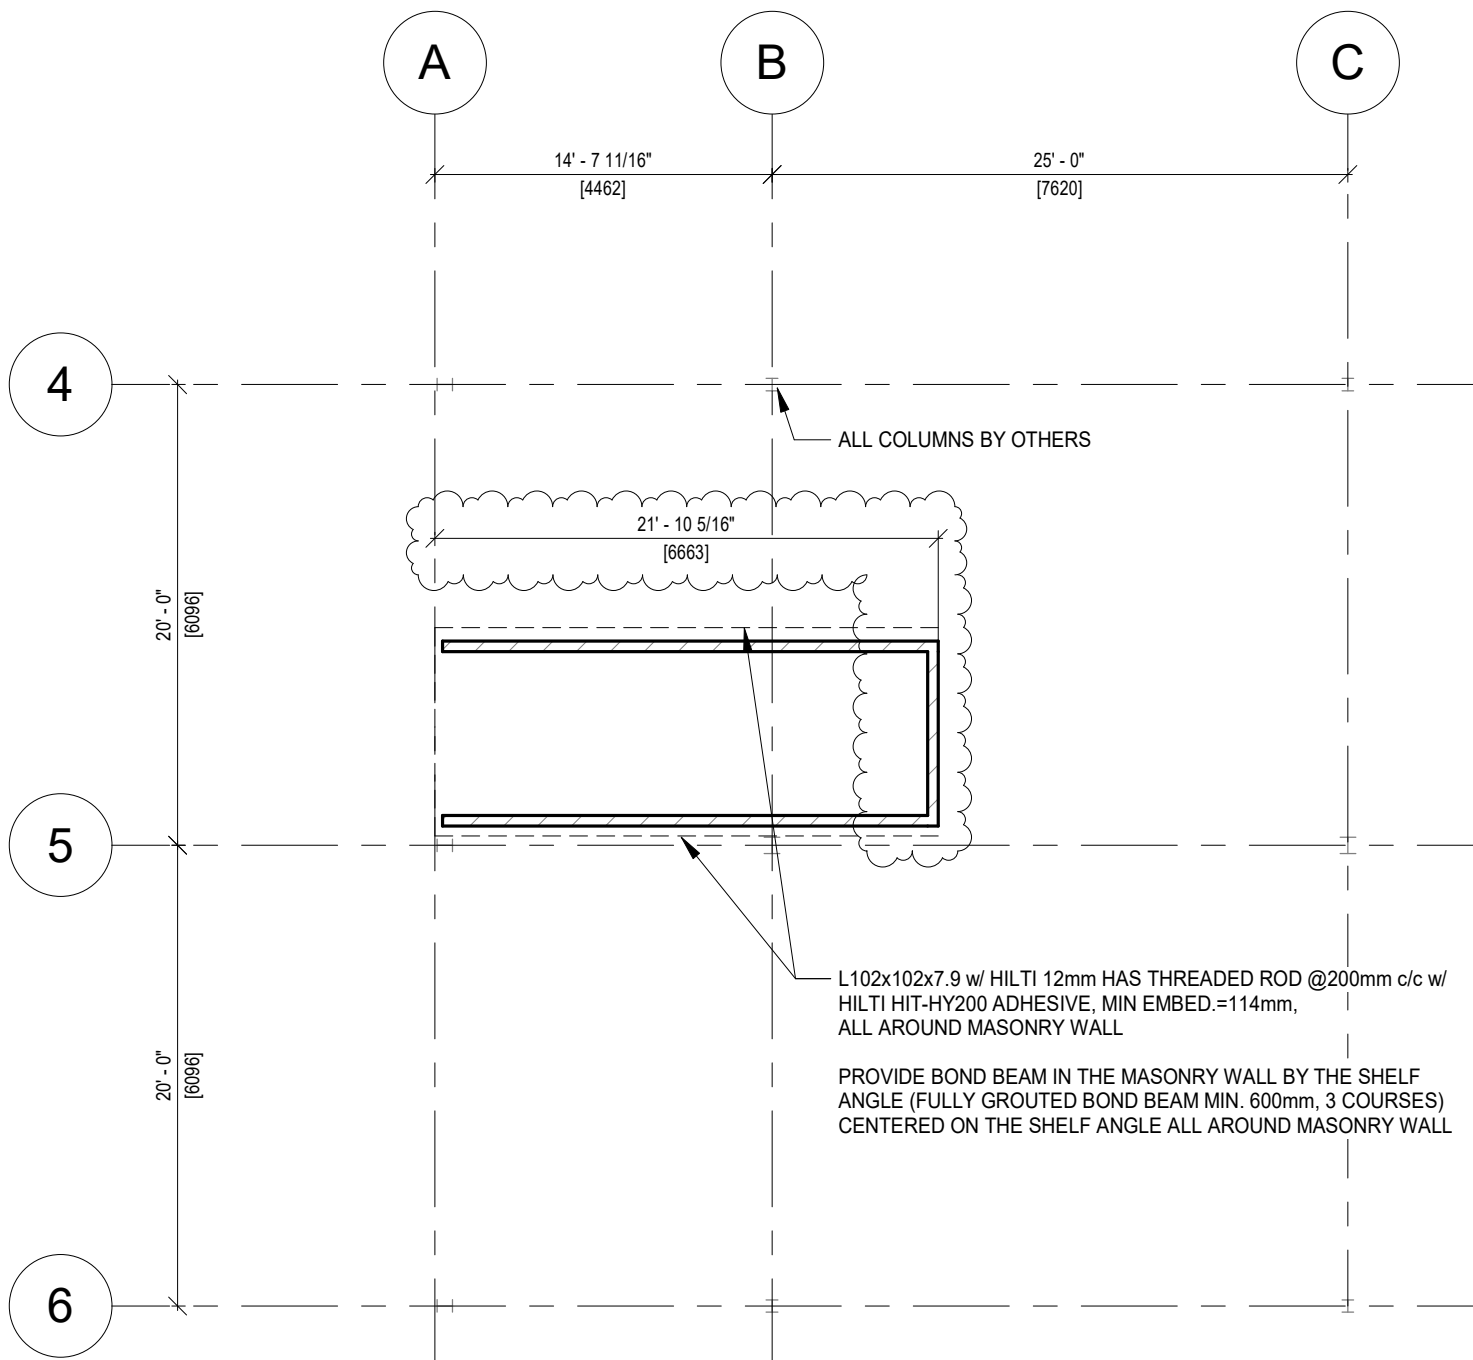


1 2ND FLOOR LEVEL - STAIRWELL B
S202 1 : 100

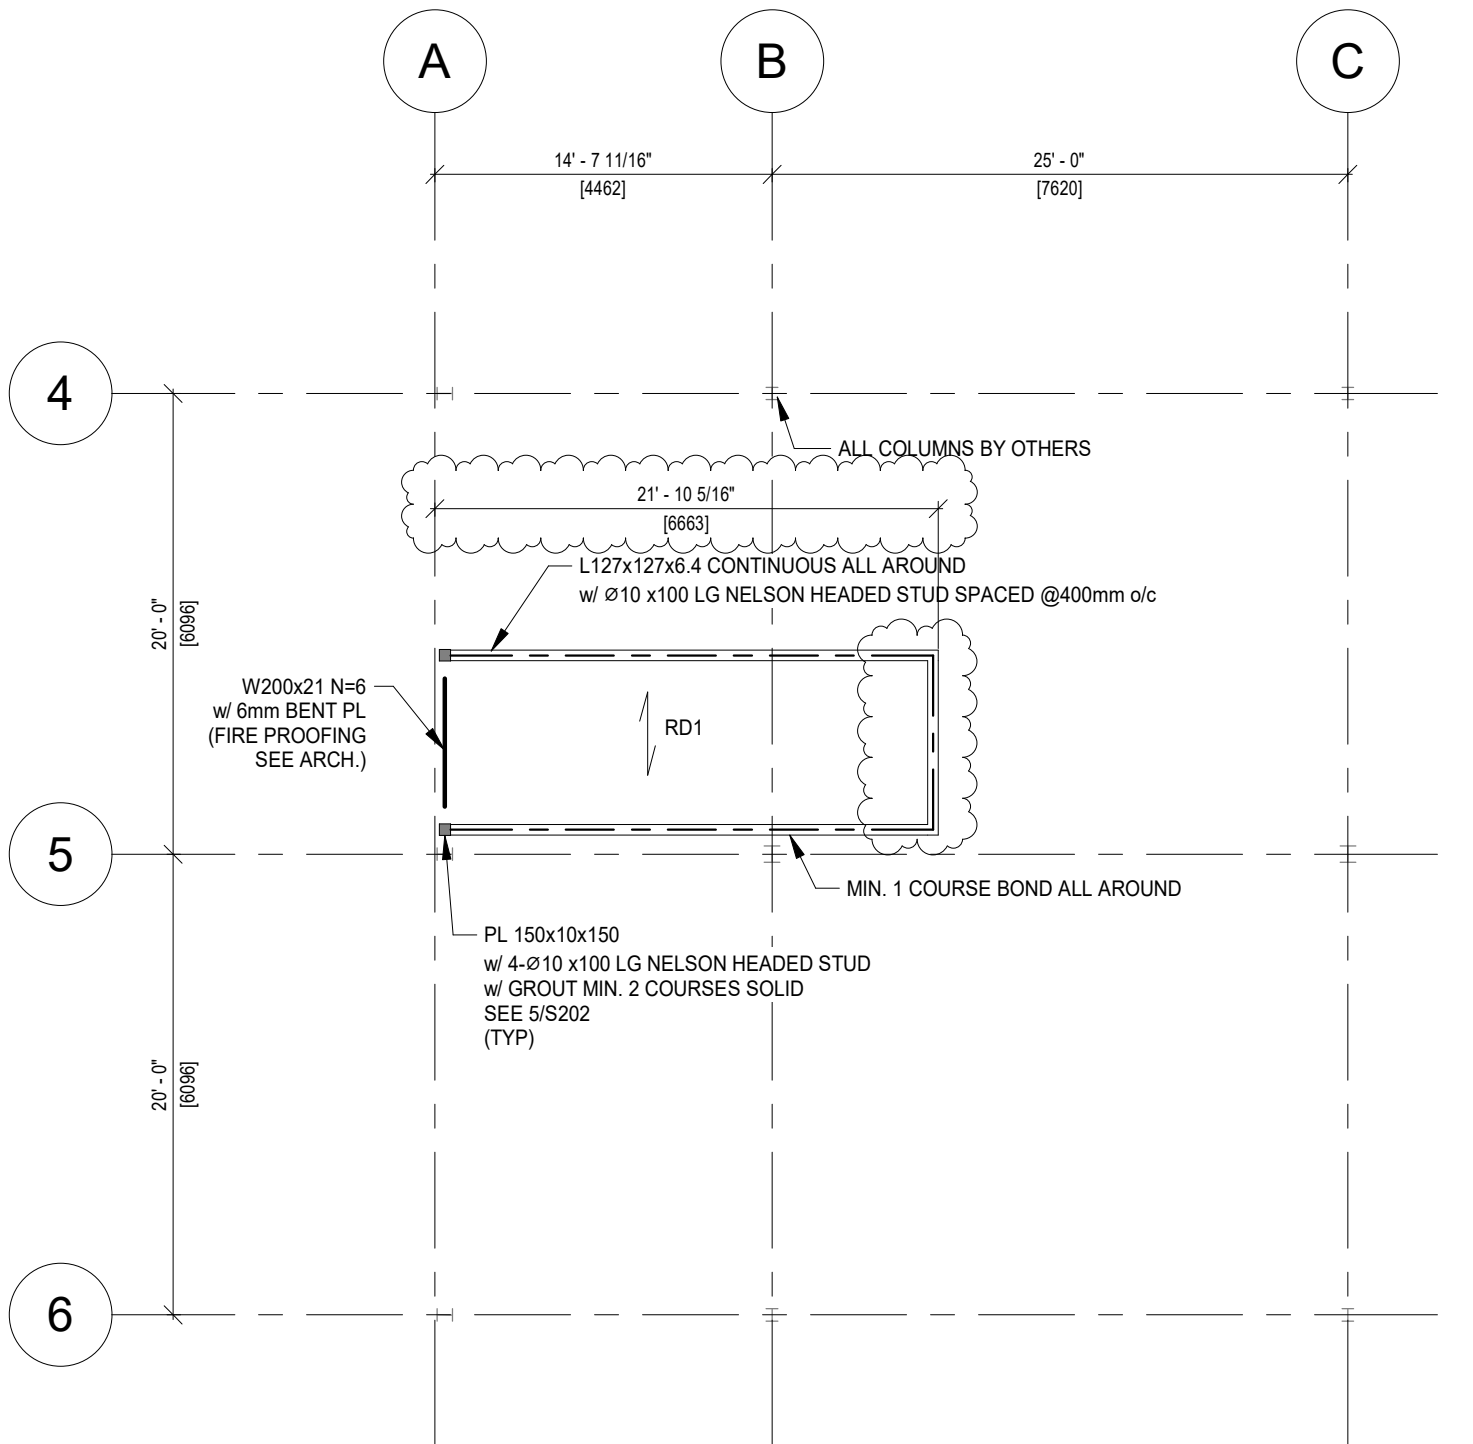





3 ROOF OF STAIRWELL B
S202 1 : 100
NOTE: SEE ARCH. DRAWING FOR TOP ELEVATION

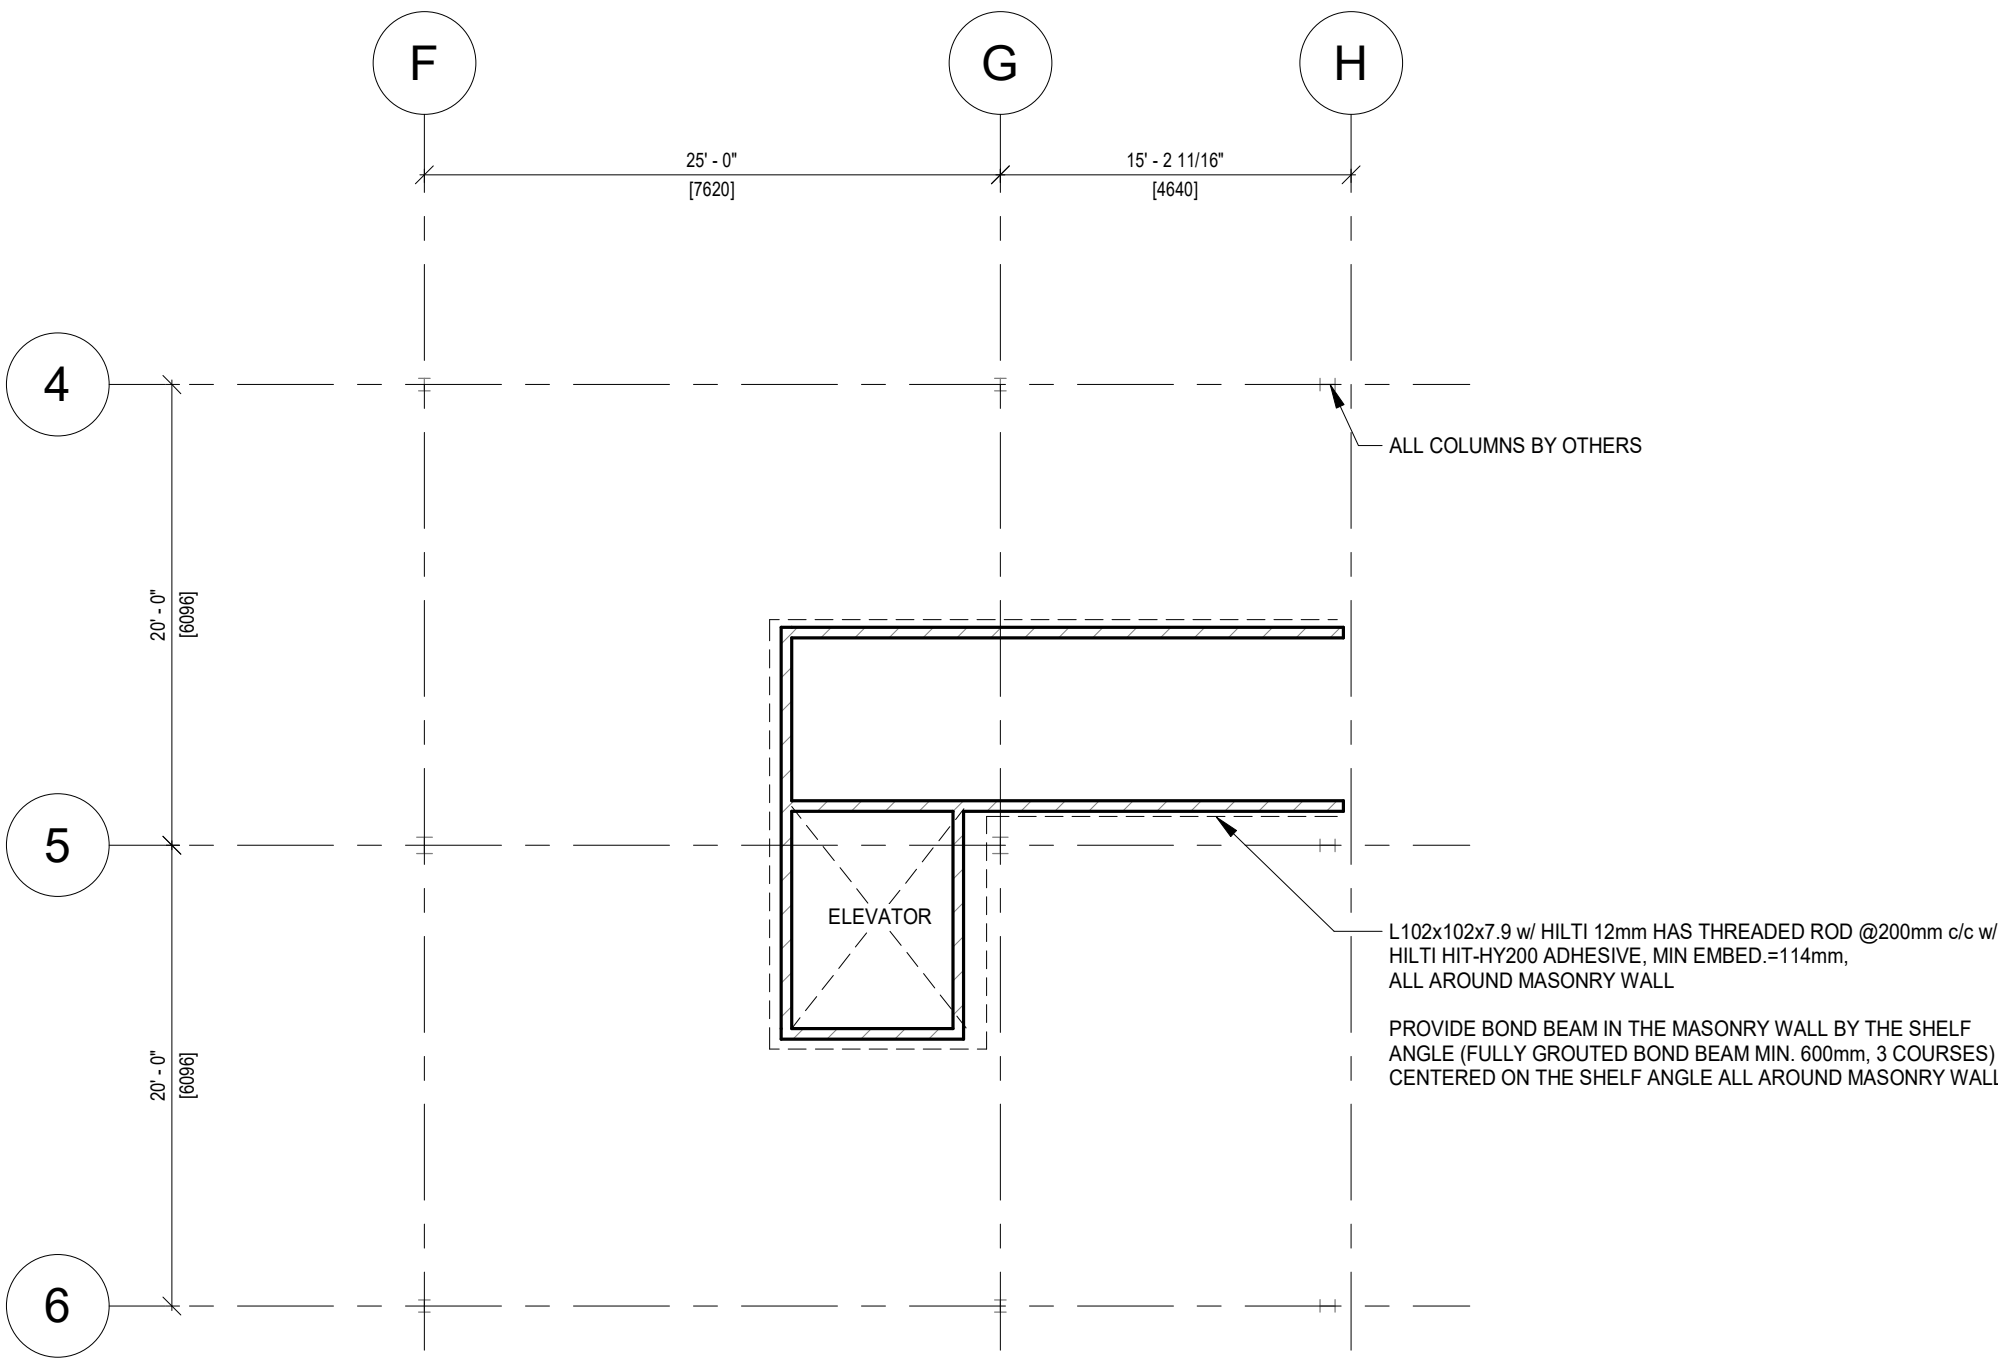


2 2ND FLOOR LEVEL - STAIRWELL A AND ELEVATOR
S202 1 : 100

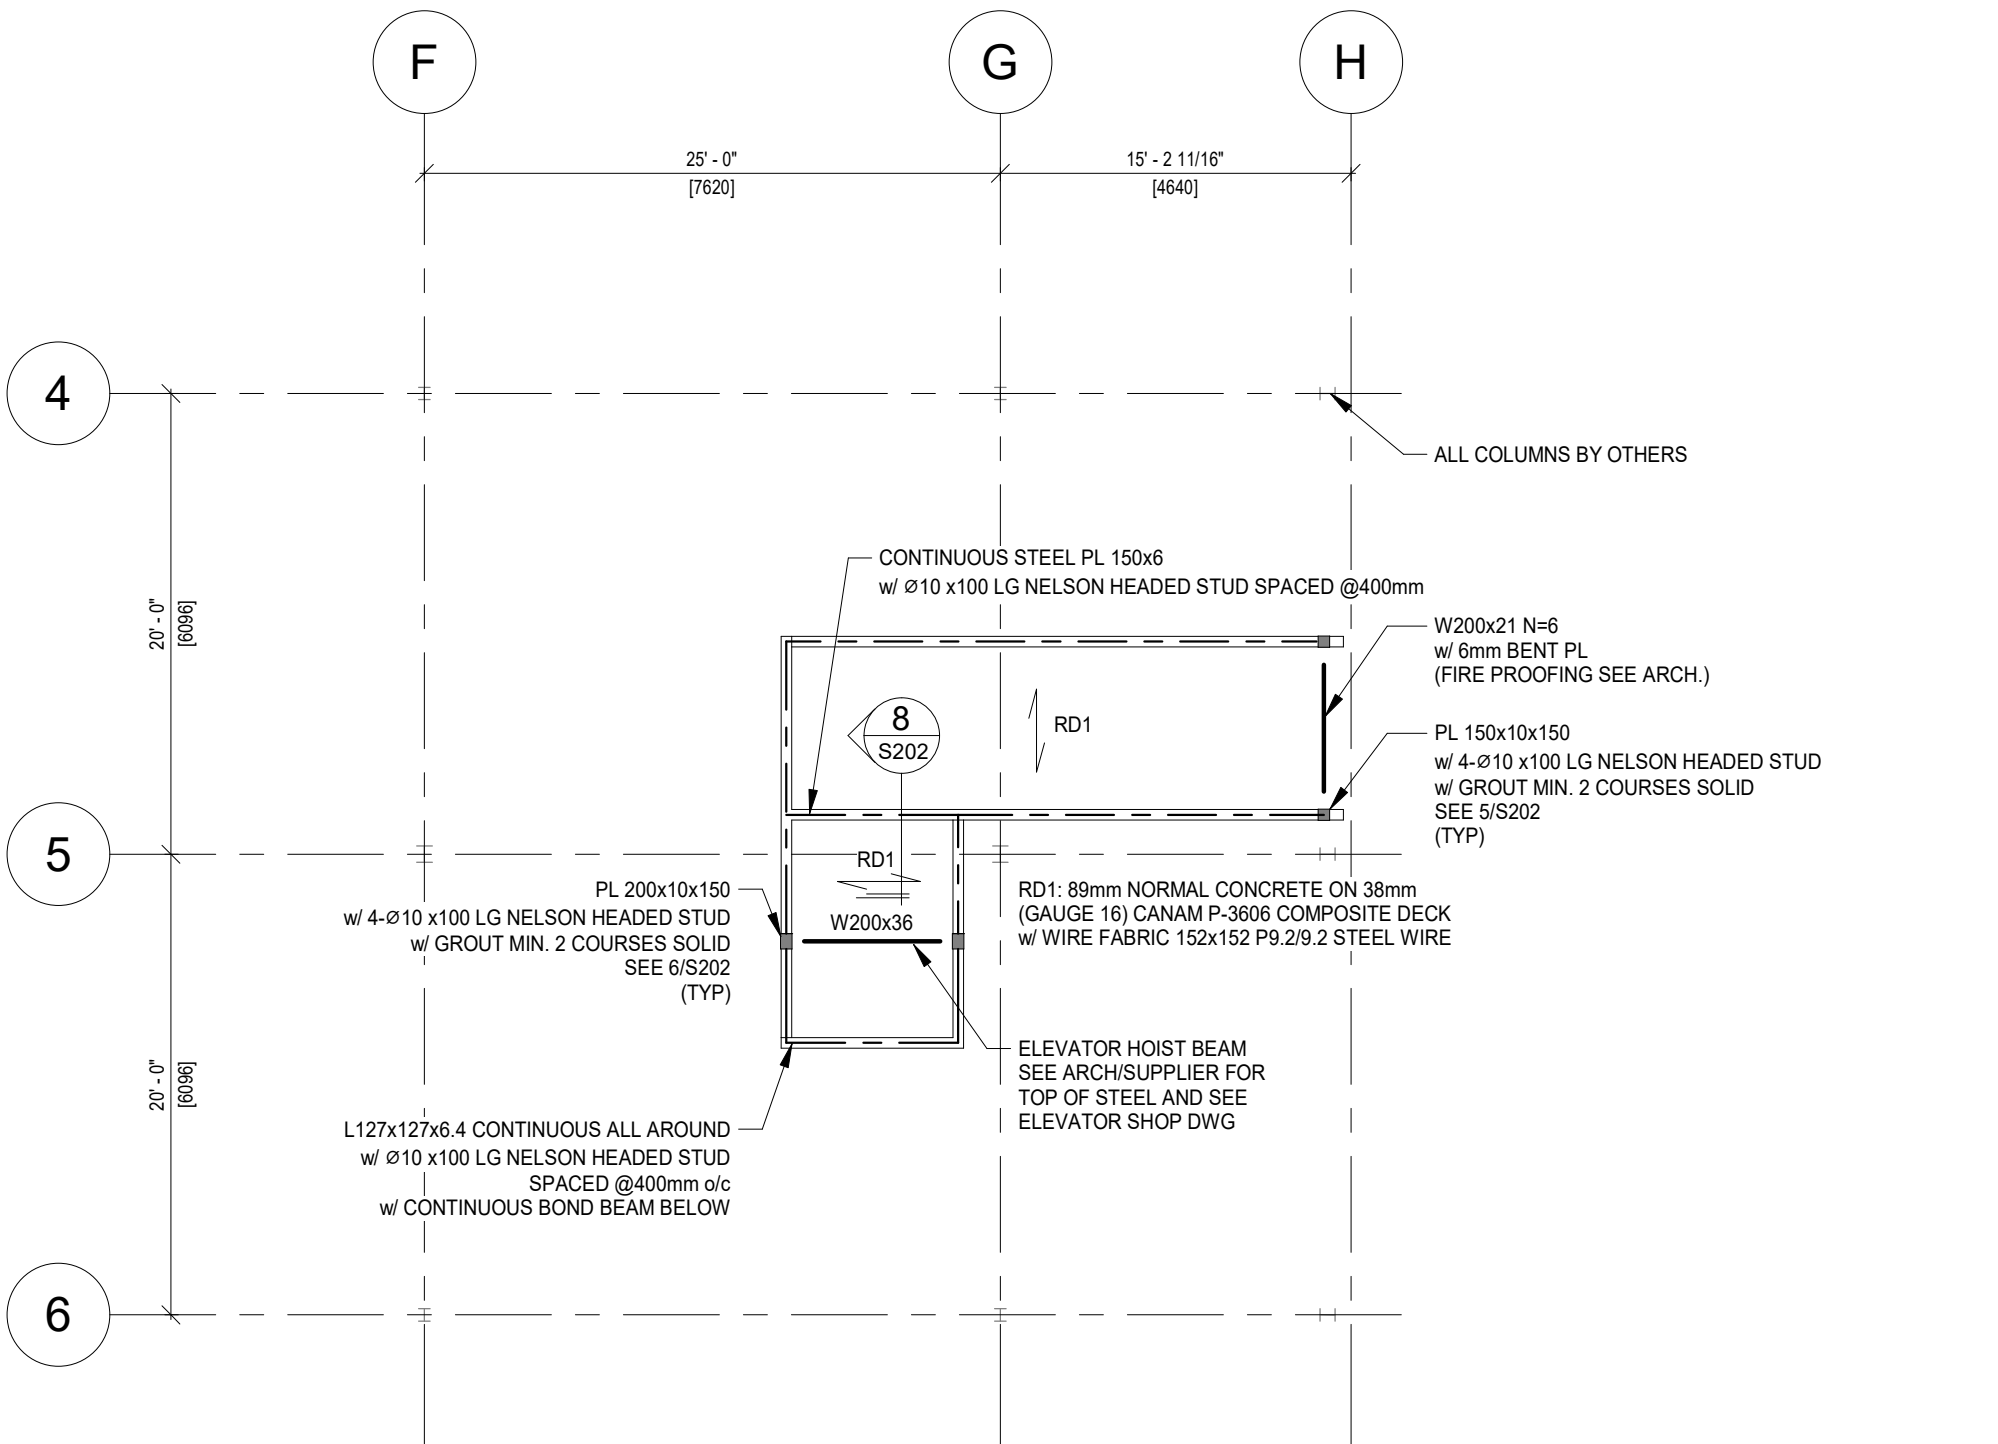

4 ROOF OF STAIRWELL A AND ELEVATOR
S202 1 : 100
NOTE: SEE ARCH. DRAWING FOR TOP ELEVATION

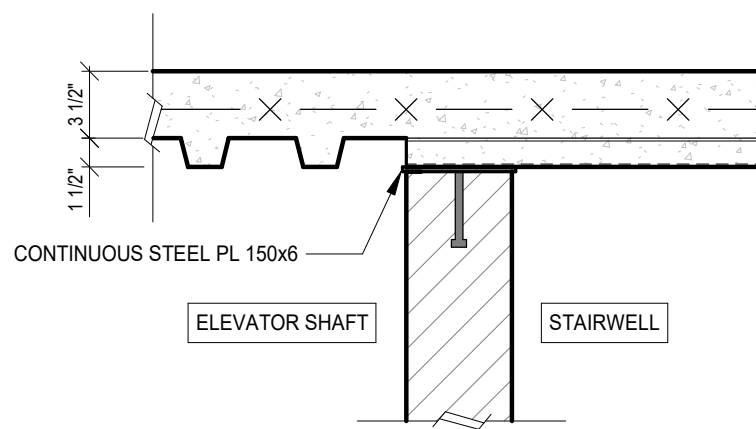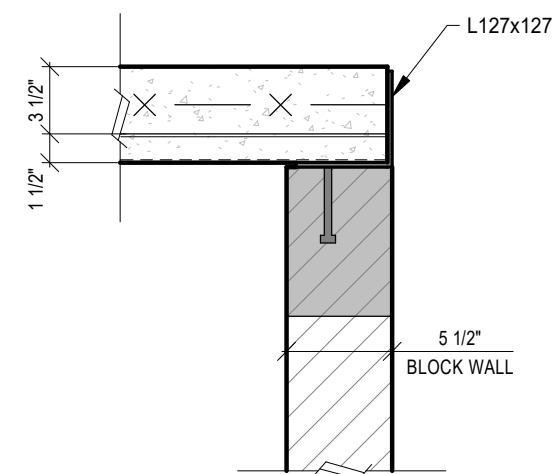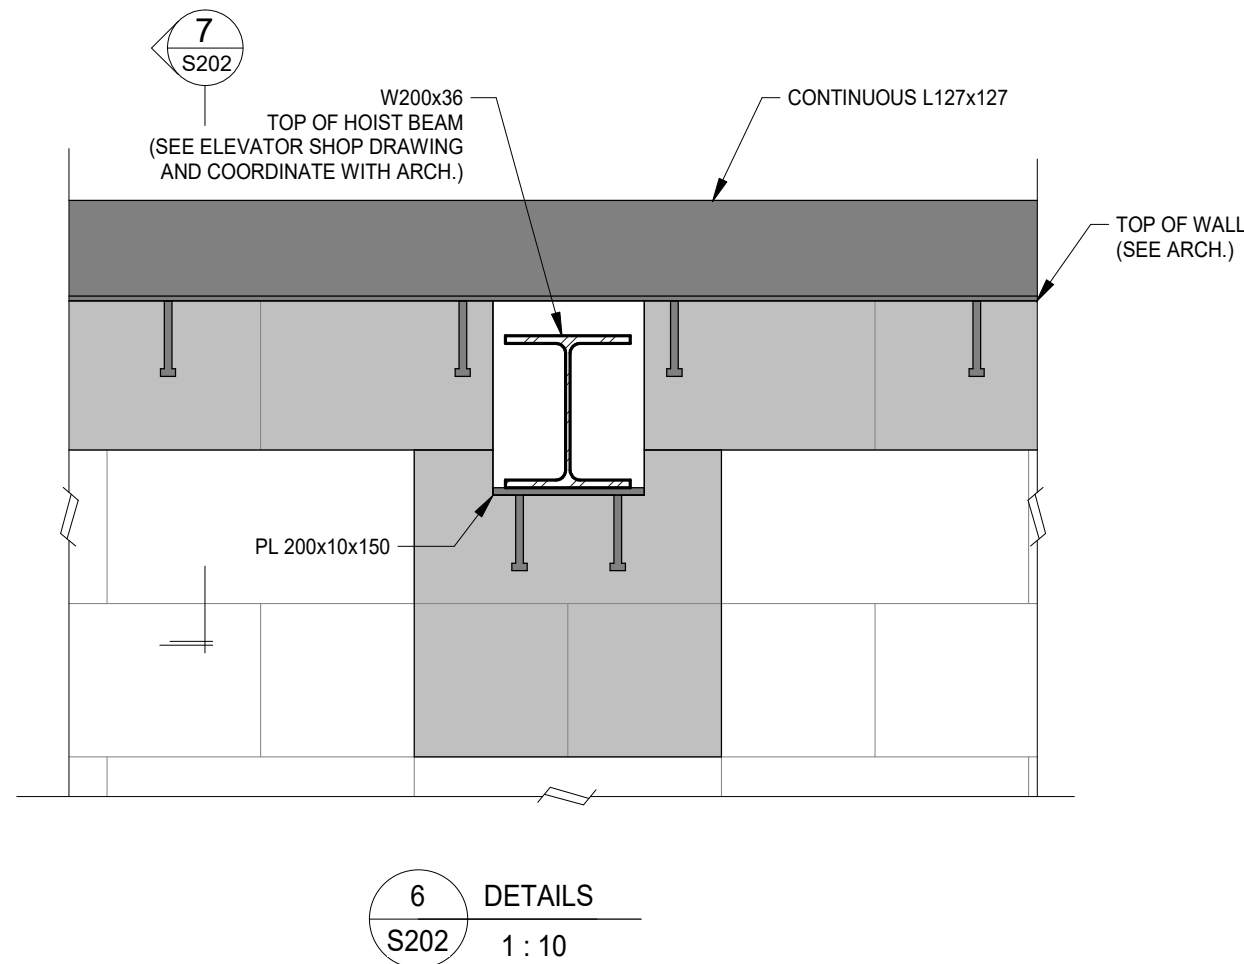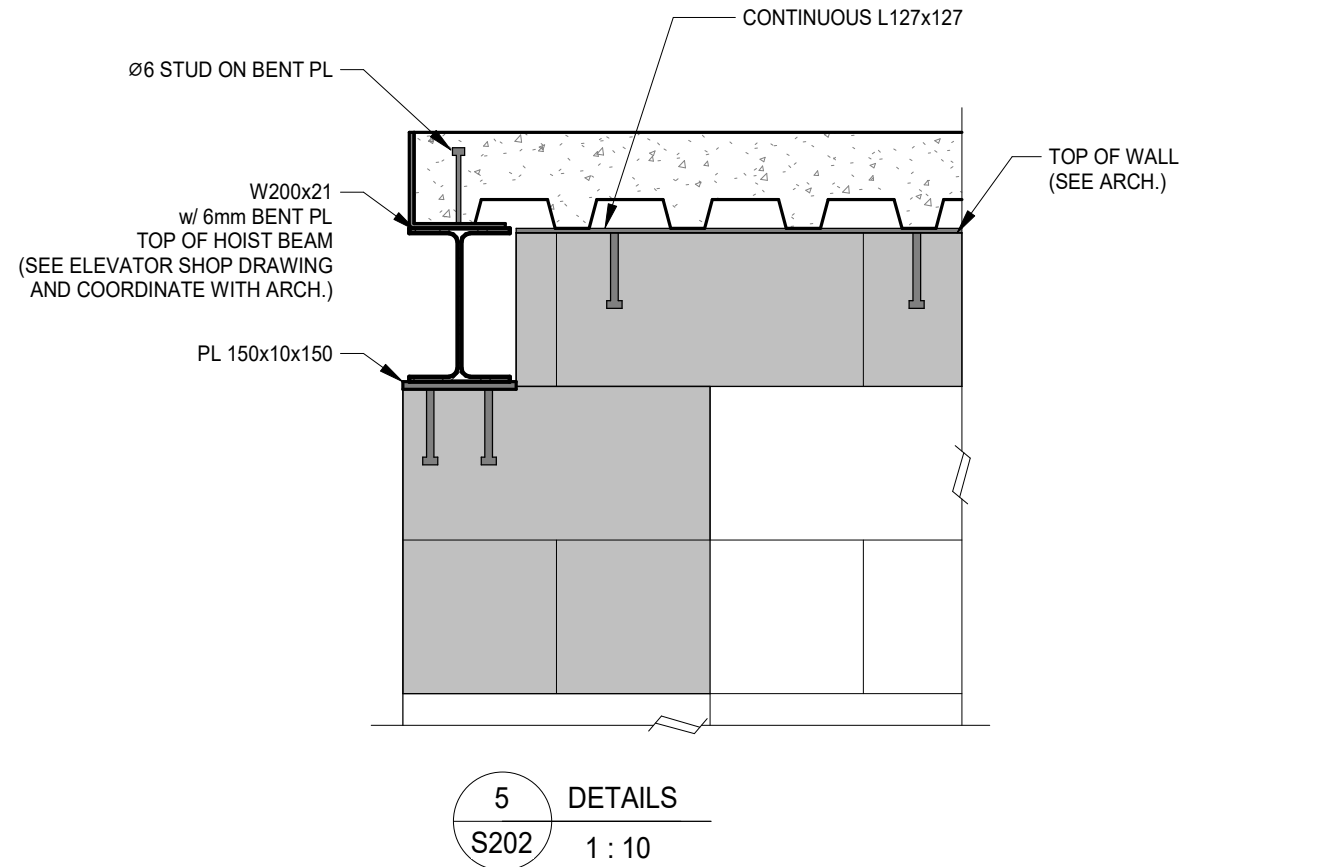

1	Issued for Permit	2024-11-14
2	Issued for Update	2025-01-26
3	Re-Issued for Permit	2025-01-29
4	Issued for Construction	2025-03-21
5	Issued for Update	2025-05-23
6	Issued for Update	2025-06-19
7	Issued for Update	2025-06-26
8	Issued for Update	2025-07-15
9	Issued for Stairwall Remedial Work	2026-01-07
NO.	REVISIONS	DATE

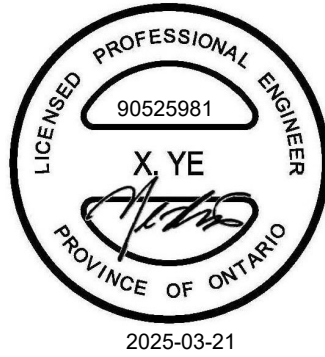

CLIENT NAME
1000115729 Ontario Limited
PROJECT NAME
Stanley Self Storage

PROJECT ADDRESS
228 Dunkirk Rd, St. Catharines, ON L2R 7K6
SHEET NAME
PART PLANS FOR STAIR A & B AND ELEVATOR - BUILDING 'A'

DRAWN BY: LS
DATE: 2026-01-07 11:03:56 AM
SCALE: As Indicated
PROJECT NO.: 23-229
CHECKED: RY




DRAWINGS ARE NOT VALID FOR CONSTRUCTION UNTIL SEALED AND SIGNED BY THE ARCHITECT.
DO NOT SCALE DRAWINGS. REPORT ALL DISCREPANCIES TO THE ARCHITECT BEFORE PROCEEDING. ALL DRAWINGS AND DESIGNS REMAIN THE PROPERTY OF THE ARCHITECT, AND ARE PROTECTED UNDER COPYRIGHT.
THESE DESIGN DOCUMENTS ARE PREPARED SOLELY FOR THE USE BY THE PARTY WITH WHOM THE DESIGN PROFESSIONAL HAS ENTERED INTO A CONTRACT AND THERE ARE NO REPRESENTATIONS OF ANY KIND MADE BY THE DESIGN PROFESSIONAL TO ANY PARTY WITH WHOM THE DESIGN PROFESSIONAL HAS NOT ENTERED INTO A CONTRACT.

SHEET #

S202

REV. #

G:\shand drives\Project Drafting\24-4945D ODA Drafting 23-229 Dunkirk Self Storage\Working File\Bldg A\23-229 Dunkirk Self Storage R23_Structure bldg A 2026\105 JC23-229 Dunkirk Self Storage R25_Building A.rvt

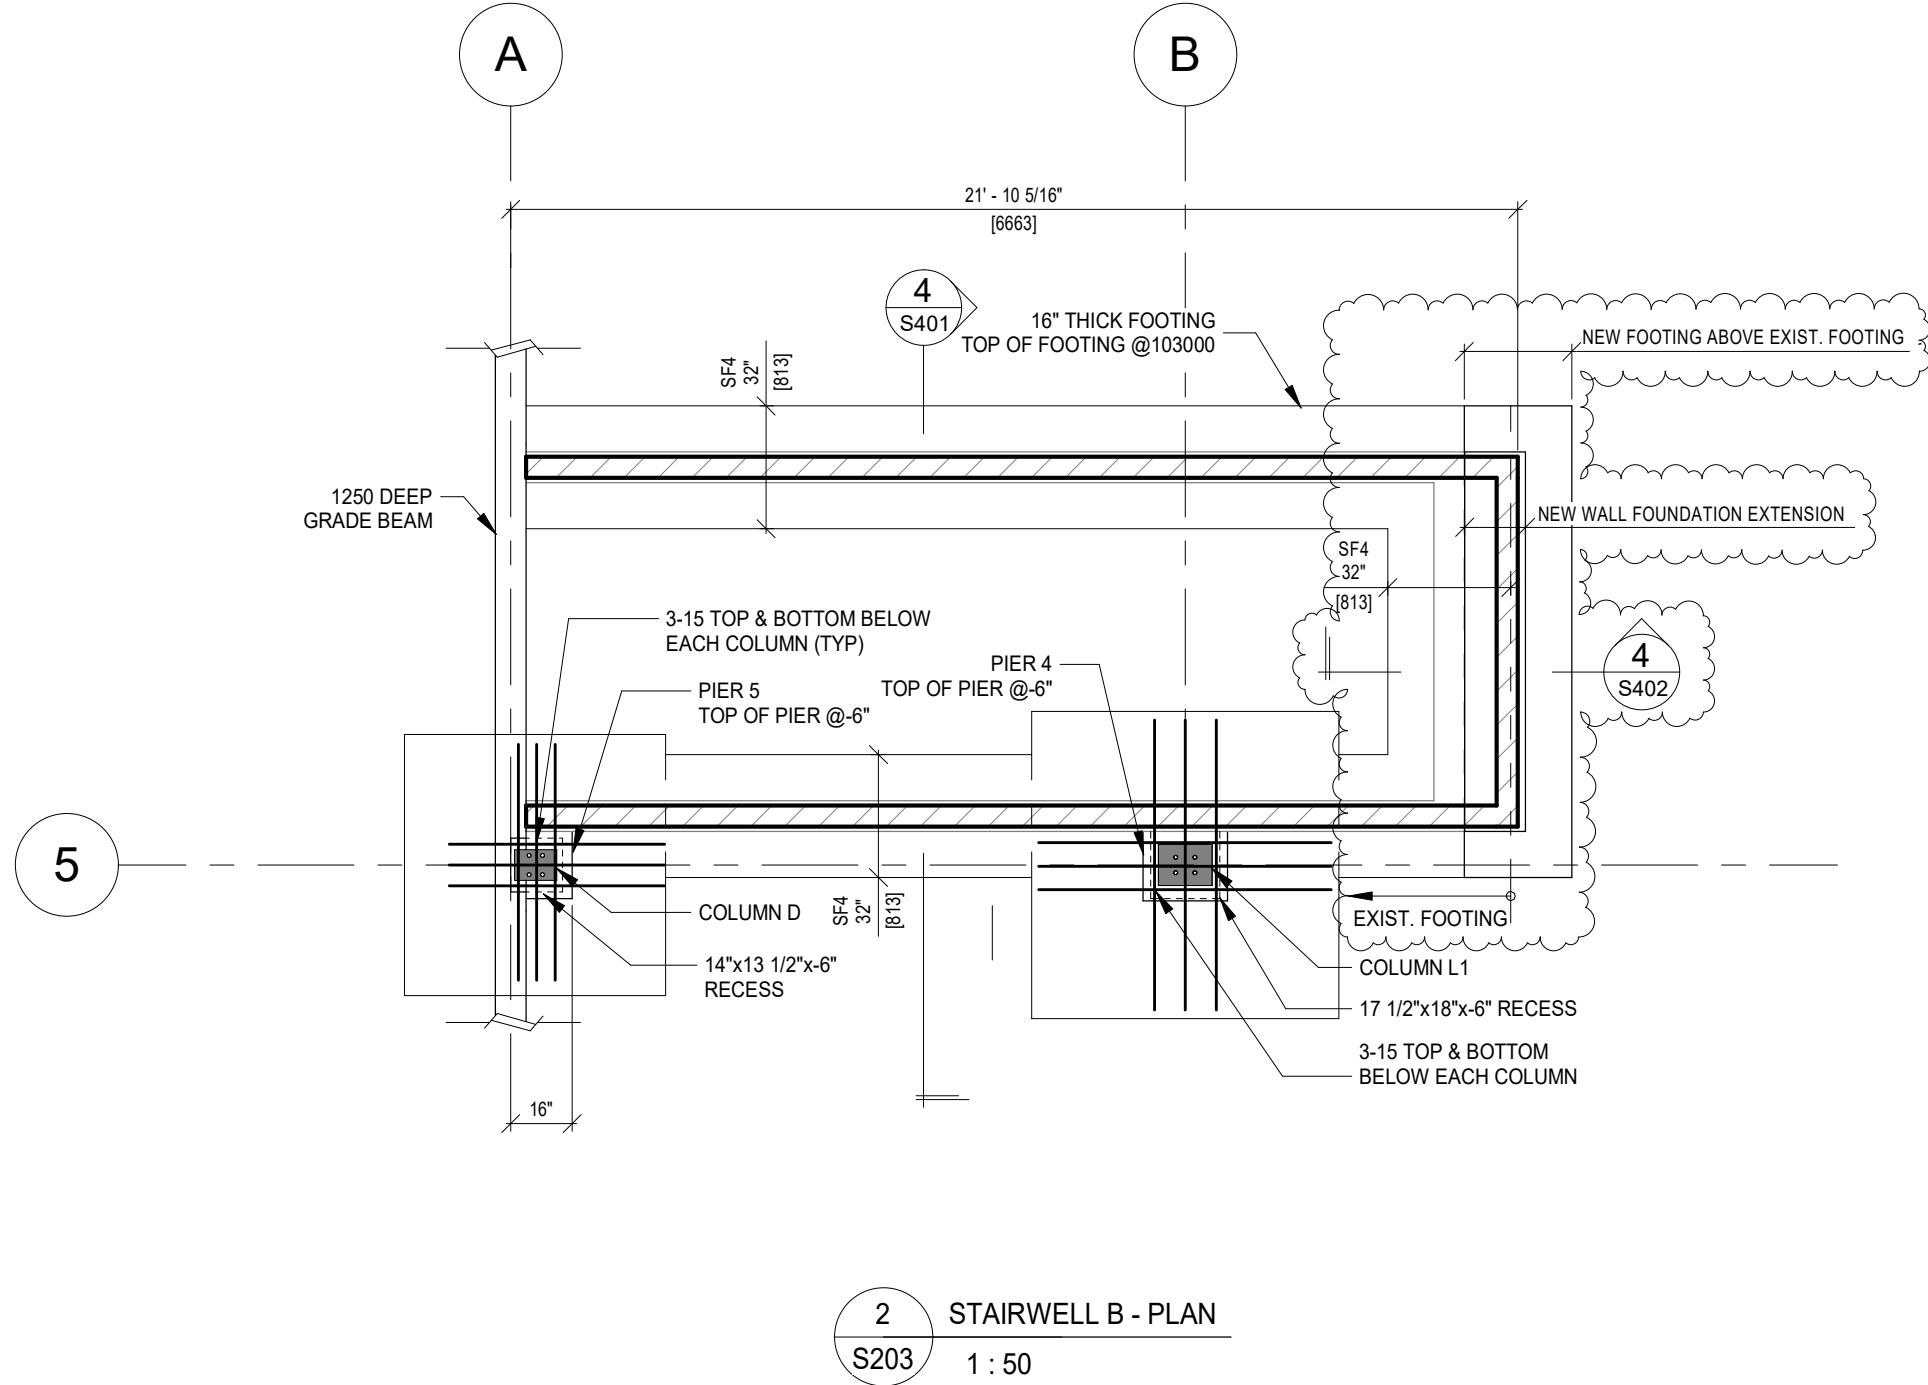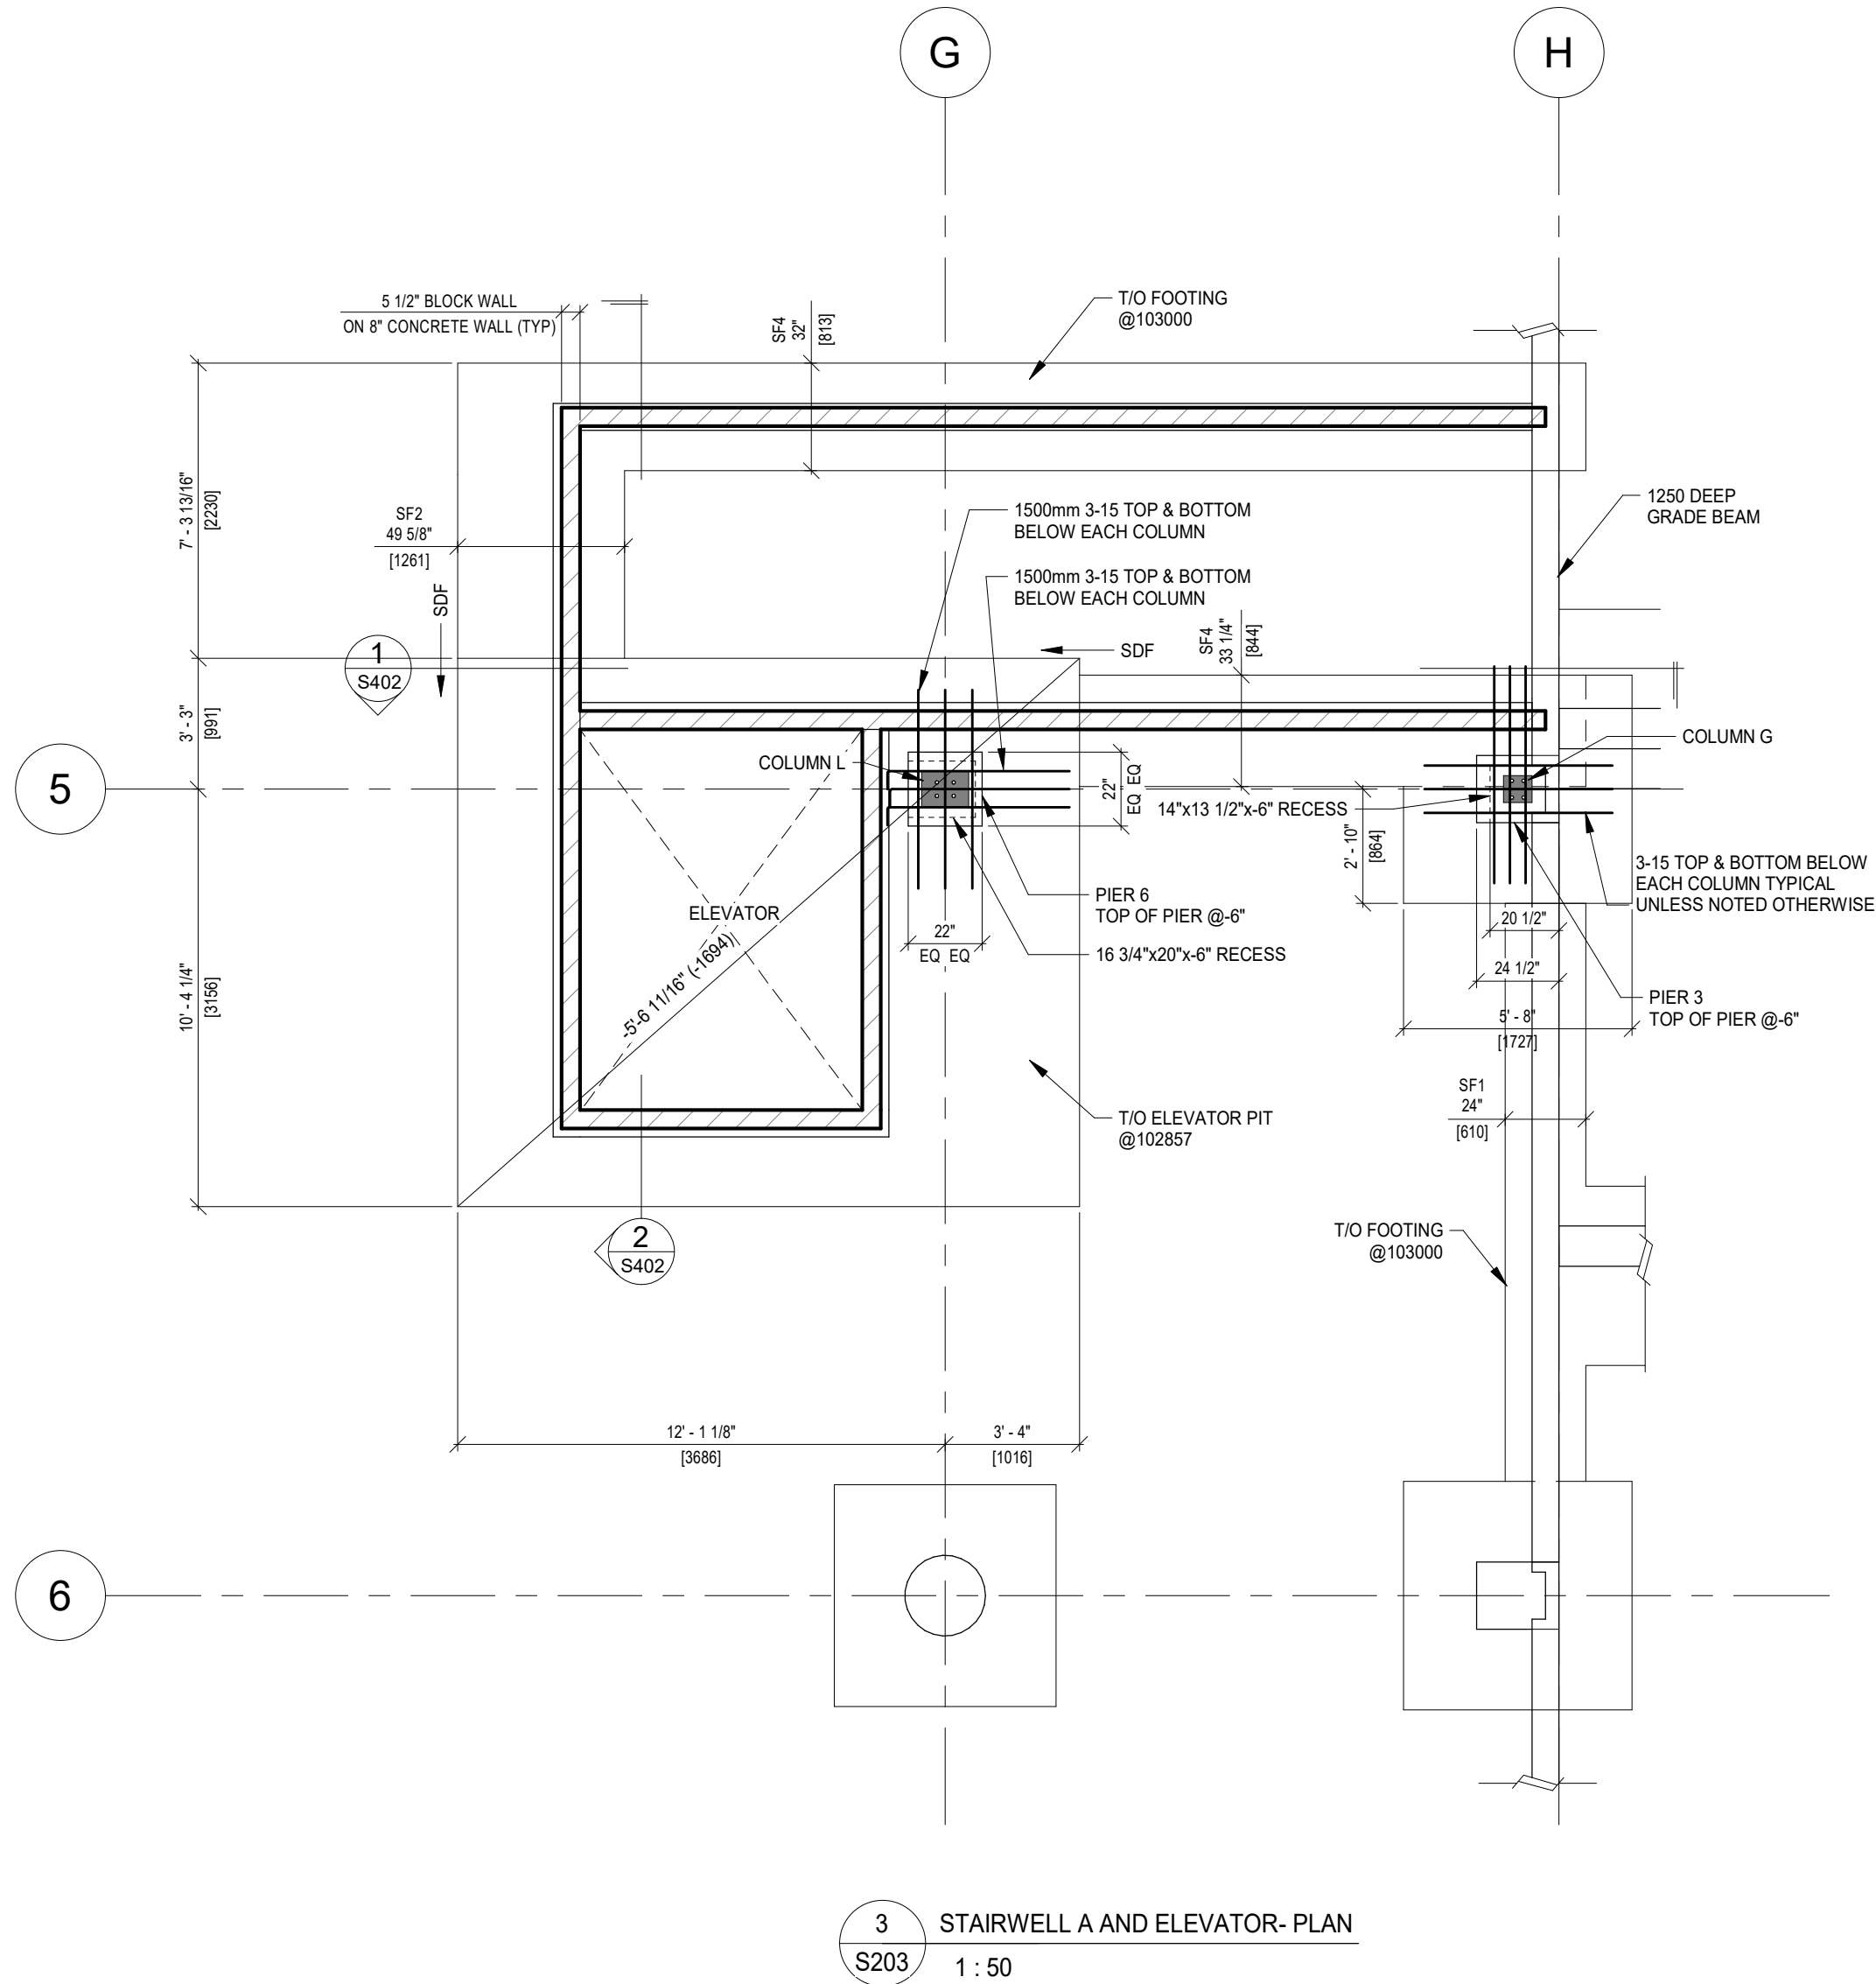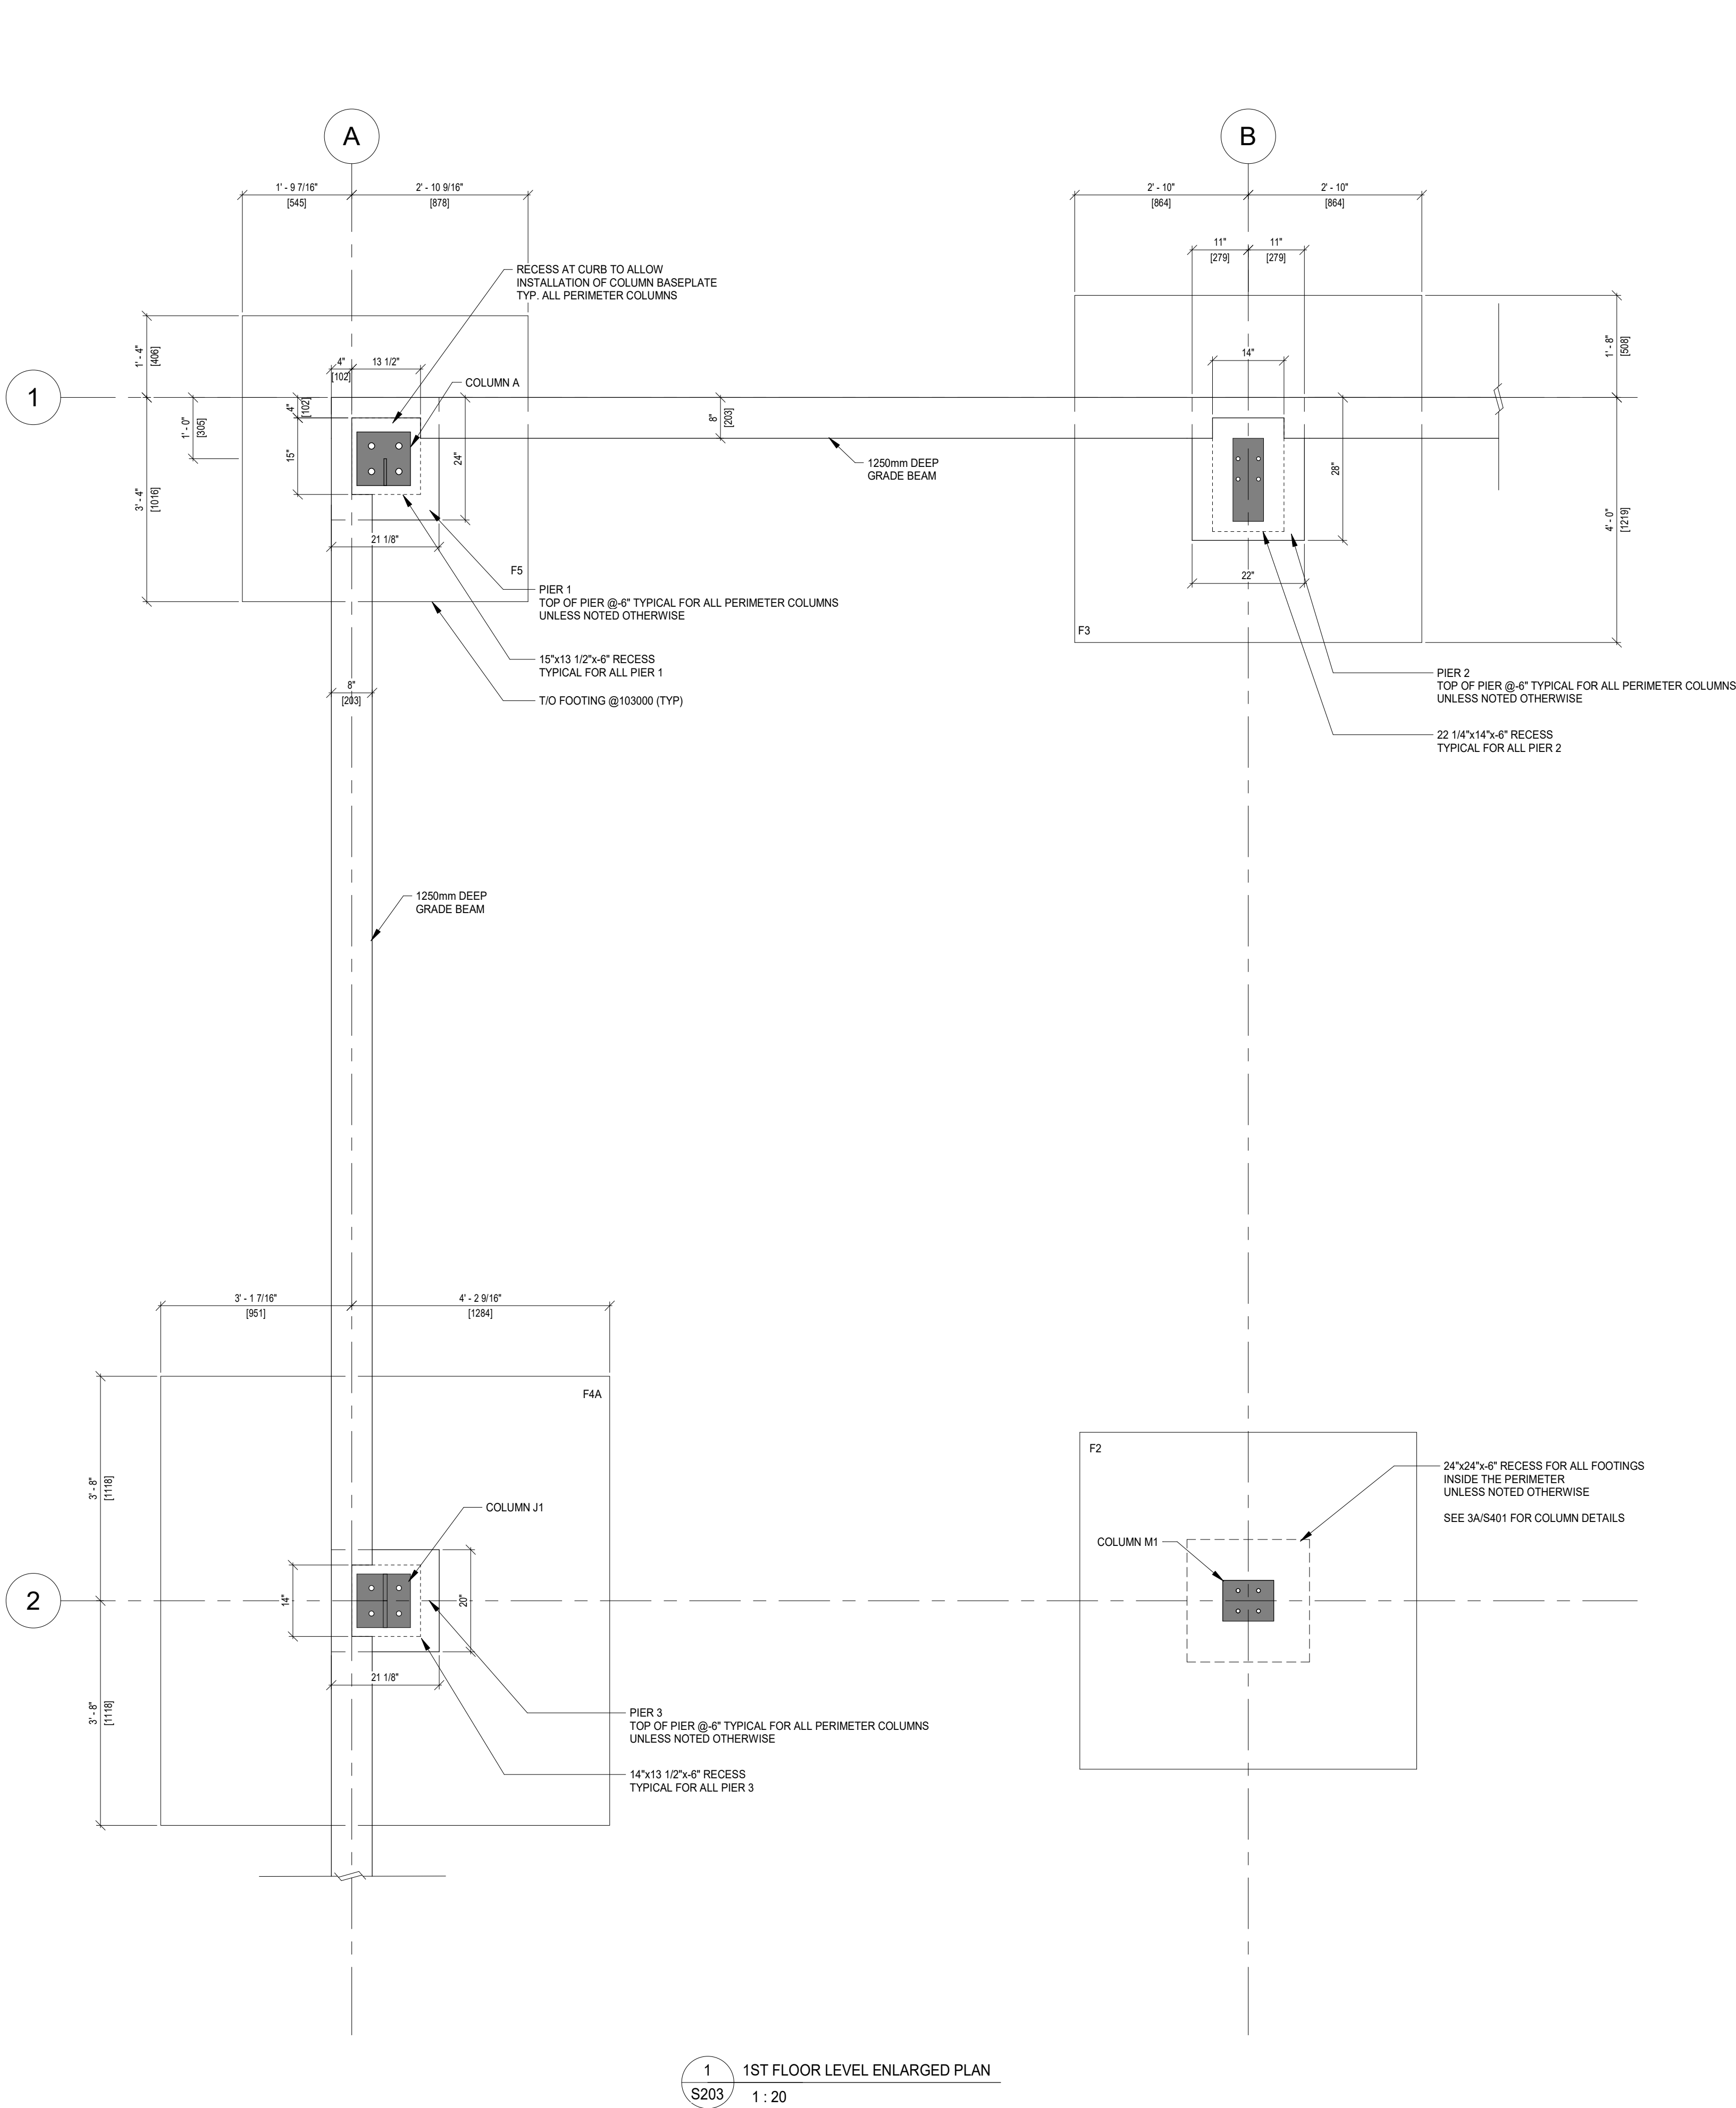

1	Issued for Permit	2024-11-14
2	Issued for Update	2025-01-26
3	Re-Issued for Permit	2025-01-26
4	Issued for Construction	2025-03-21
5	Issued for Update	2025-05-23
6	Issued for Update	2025-06-11
7	Issued for Update	2025-06-26
8	Issued for Stairwell Remedial Work	2026-01-07
NO.	REVISIONS	DATE



4687 Queen Street Suite 2,
Niagara Falls, ON, L2E 2L9
T | 905-357-4441
F | 905-357-9203
W | www.raimondoaarchitects.com
E | mail@raimondoaarchitects.com

CLIENT NAME
1000115729 Ontario Limited
PROJECT NAME
Stanley Self Storage

PROJECT ADDRESS
228 Dunkirk Rd, St. Catharines, ON L2R 7K6
SHEET NAME
ENLARGED FLOOR
PLANS - BUILDING 'A'

DRAWN BY: LS
DATE: 2026-01-07 11:03:56 AM
SCALE: As Indicated
PROJECT NO.: 23-229
CHECKED: RY

DRAWINGS ARE NOT VALID FOR CONSTRUCTION UNTIL SEALED AND SIGNED BY THE ARCHITECT.
DO NOT SCALE DRAWINGS. REPORT ALL DISCREPANCIES TO THE ARCHITECT BEFORE PROCEEDING. ALL DRAWINGS AND DESIGNS REMAIN THE PROPERTY OF THE ARCHITECT, AND ARE PROTECTED UNDER COPYRIGHT.





THESE DESIGN DOCUMENTS ARE PREPARED SOLELY FOR THE USE BY THE PARTY WITH WHOM THE DESIGN PROFESSIONAL HAS ENTERED INTO A CONTRACT AND THERE ARE NO REPRESENTATIONS OF ANY KIND MADE BY THE DESIGN PROFESSIONAL TO ANY PARTY WITH WHOM THE DESIGN PROFESSIONAL HAS NOT ENTERED INTO A CONTRACT.

SHEET #

S203

REV. #

G:\shand drives\Project Drafting\24-4945D ODA Drafting 23-229 Dunkirk Self Storage\Working File\Bldg A\23-229 Dunkirk Self Storage R23_Structure bldg A 2026\105 JC23-229 Dunkirk Self Storage R25_Building A.rvt

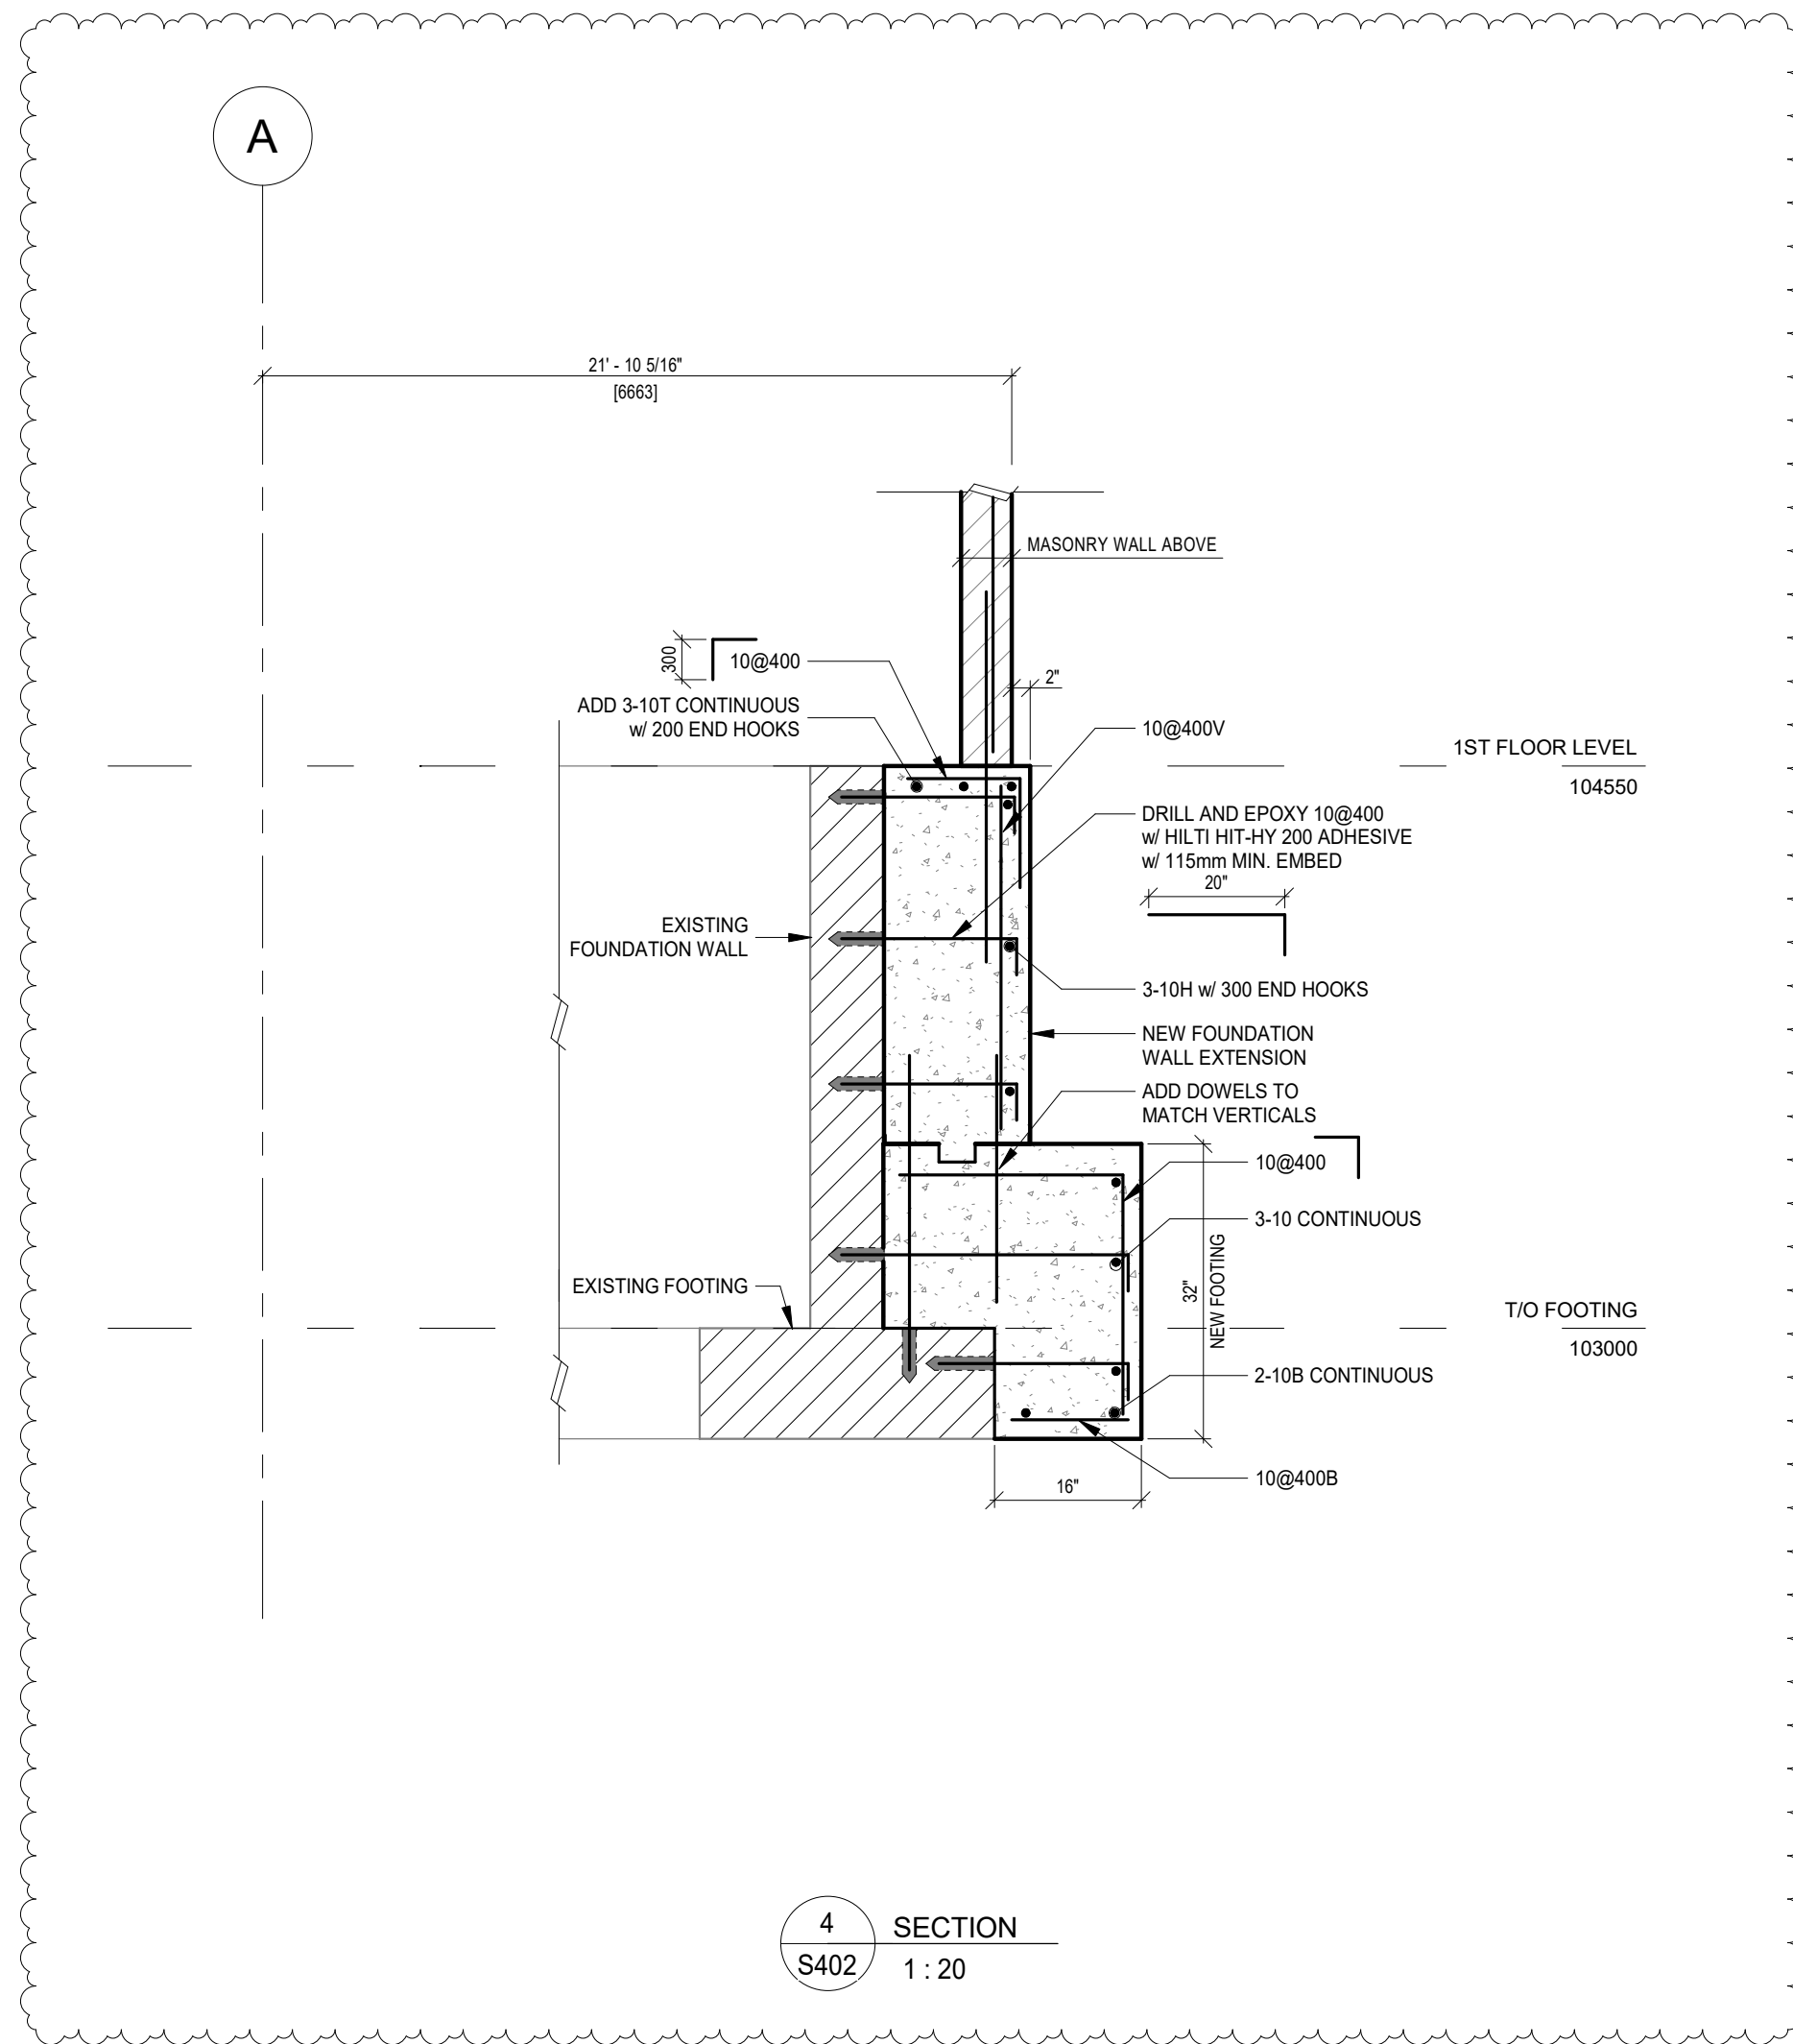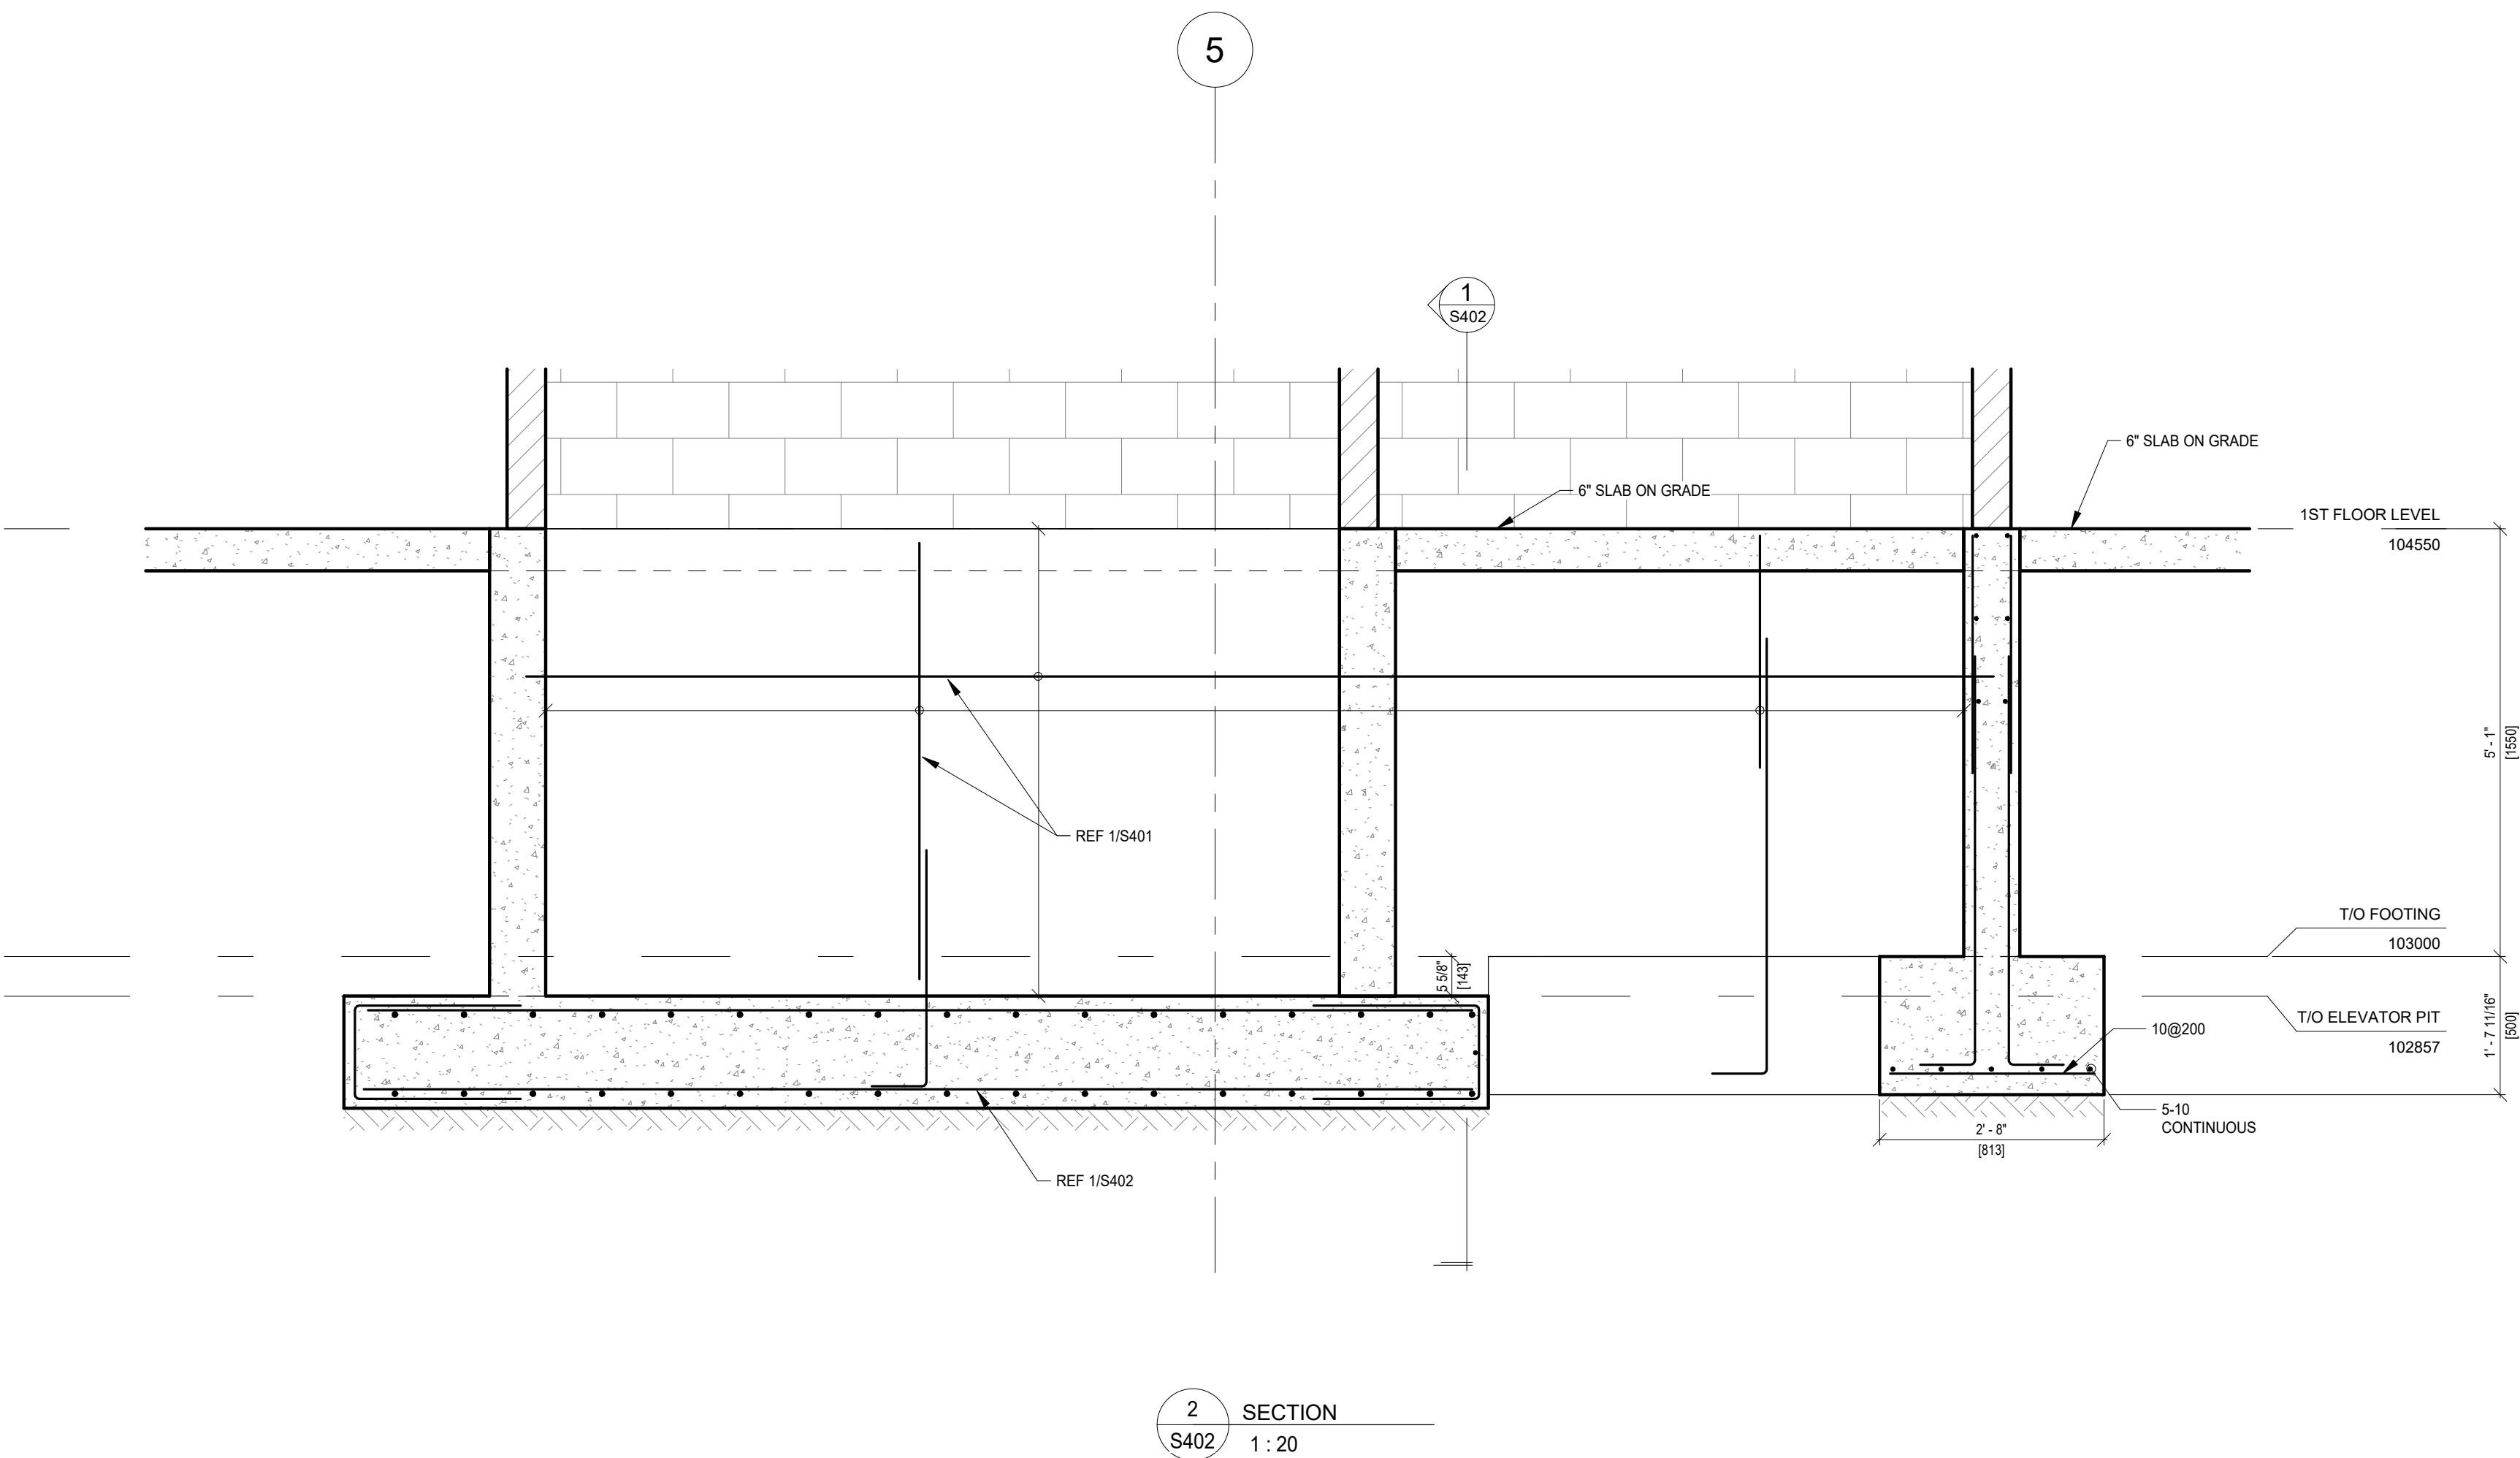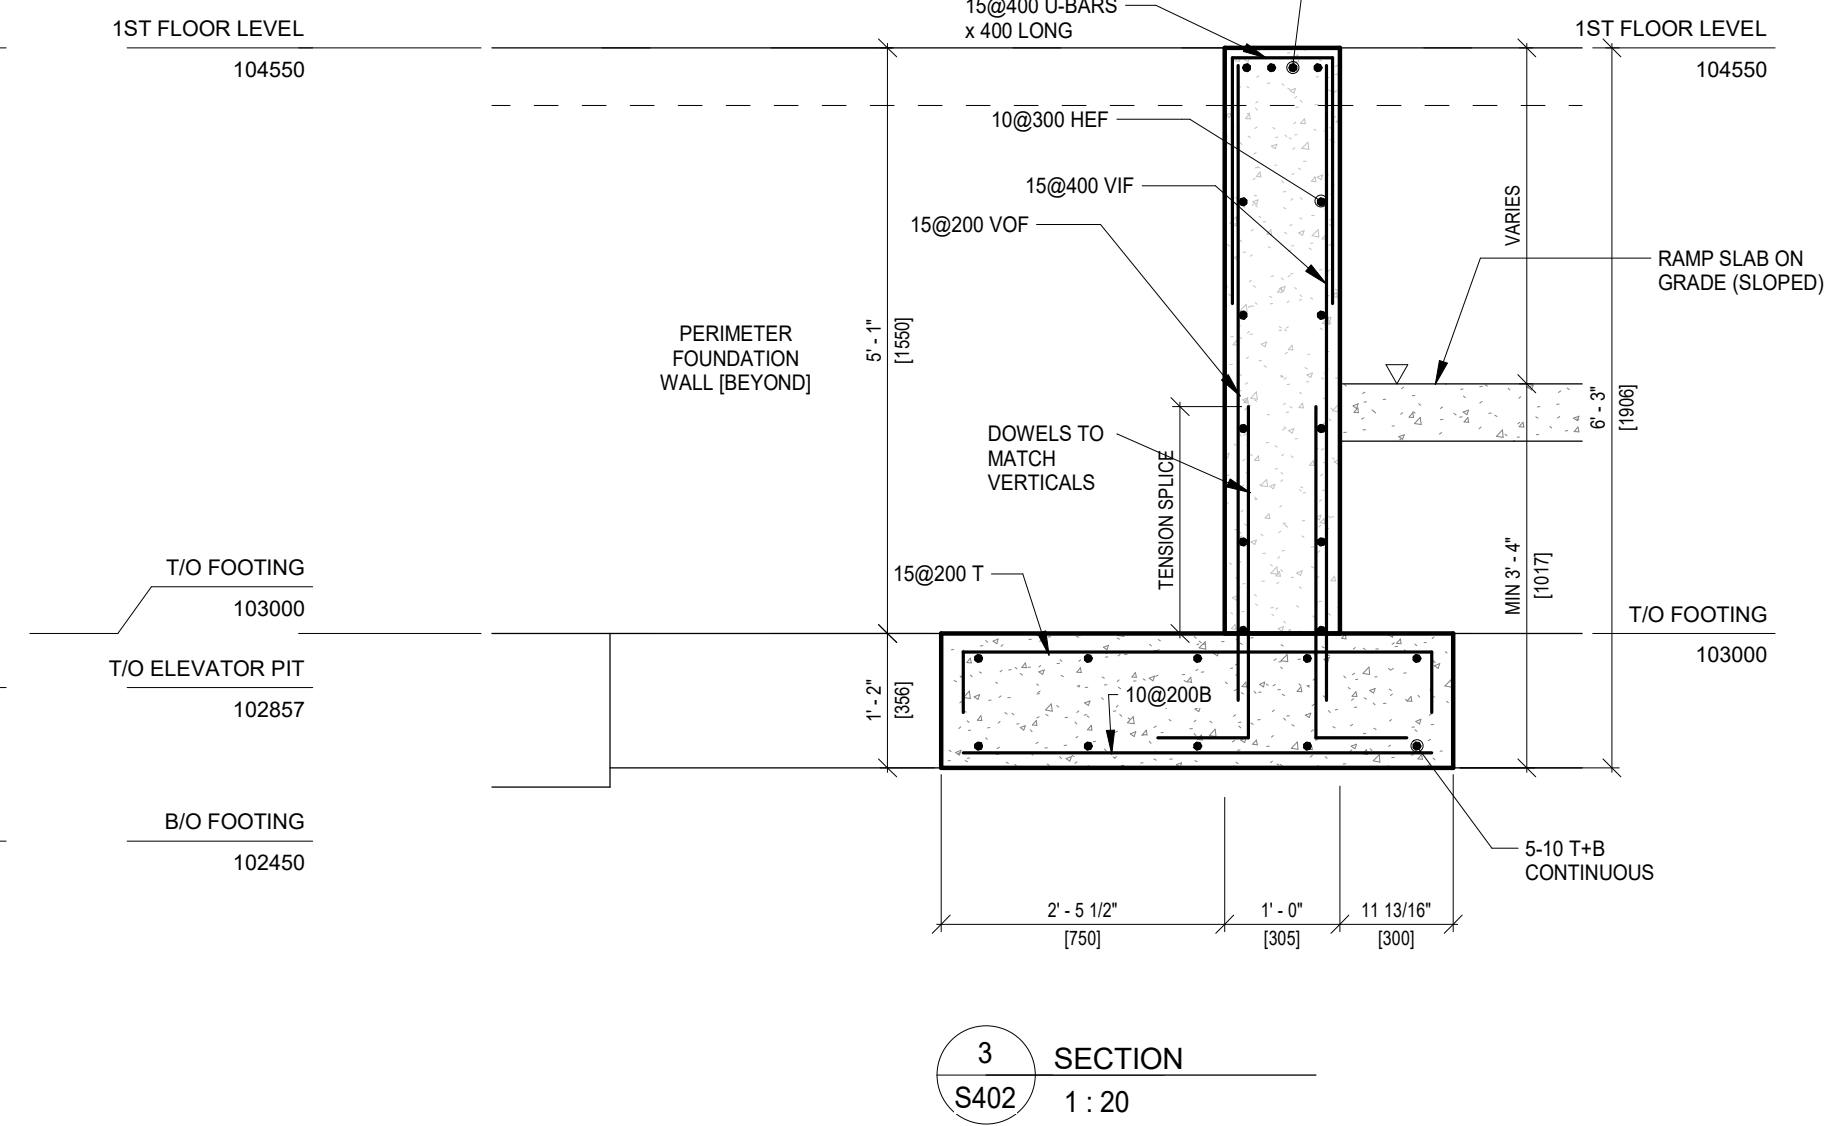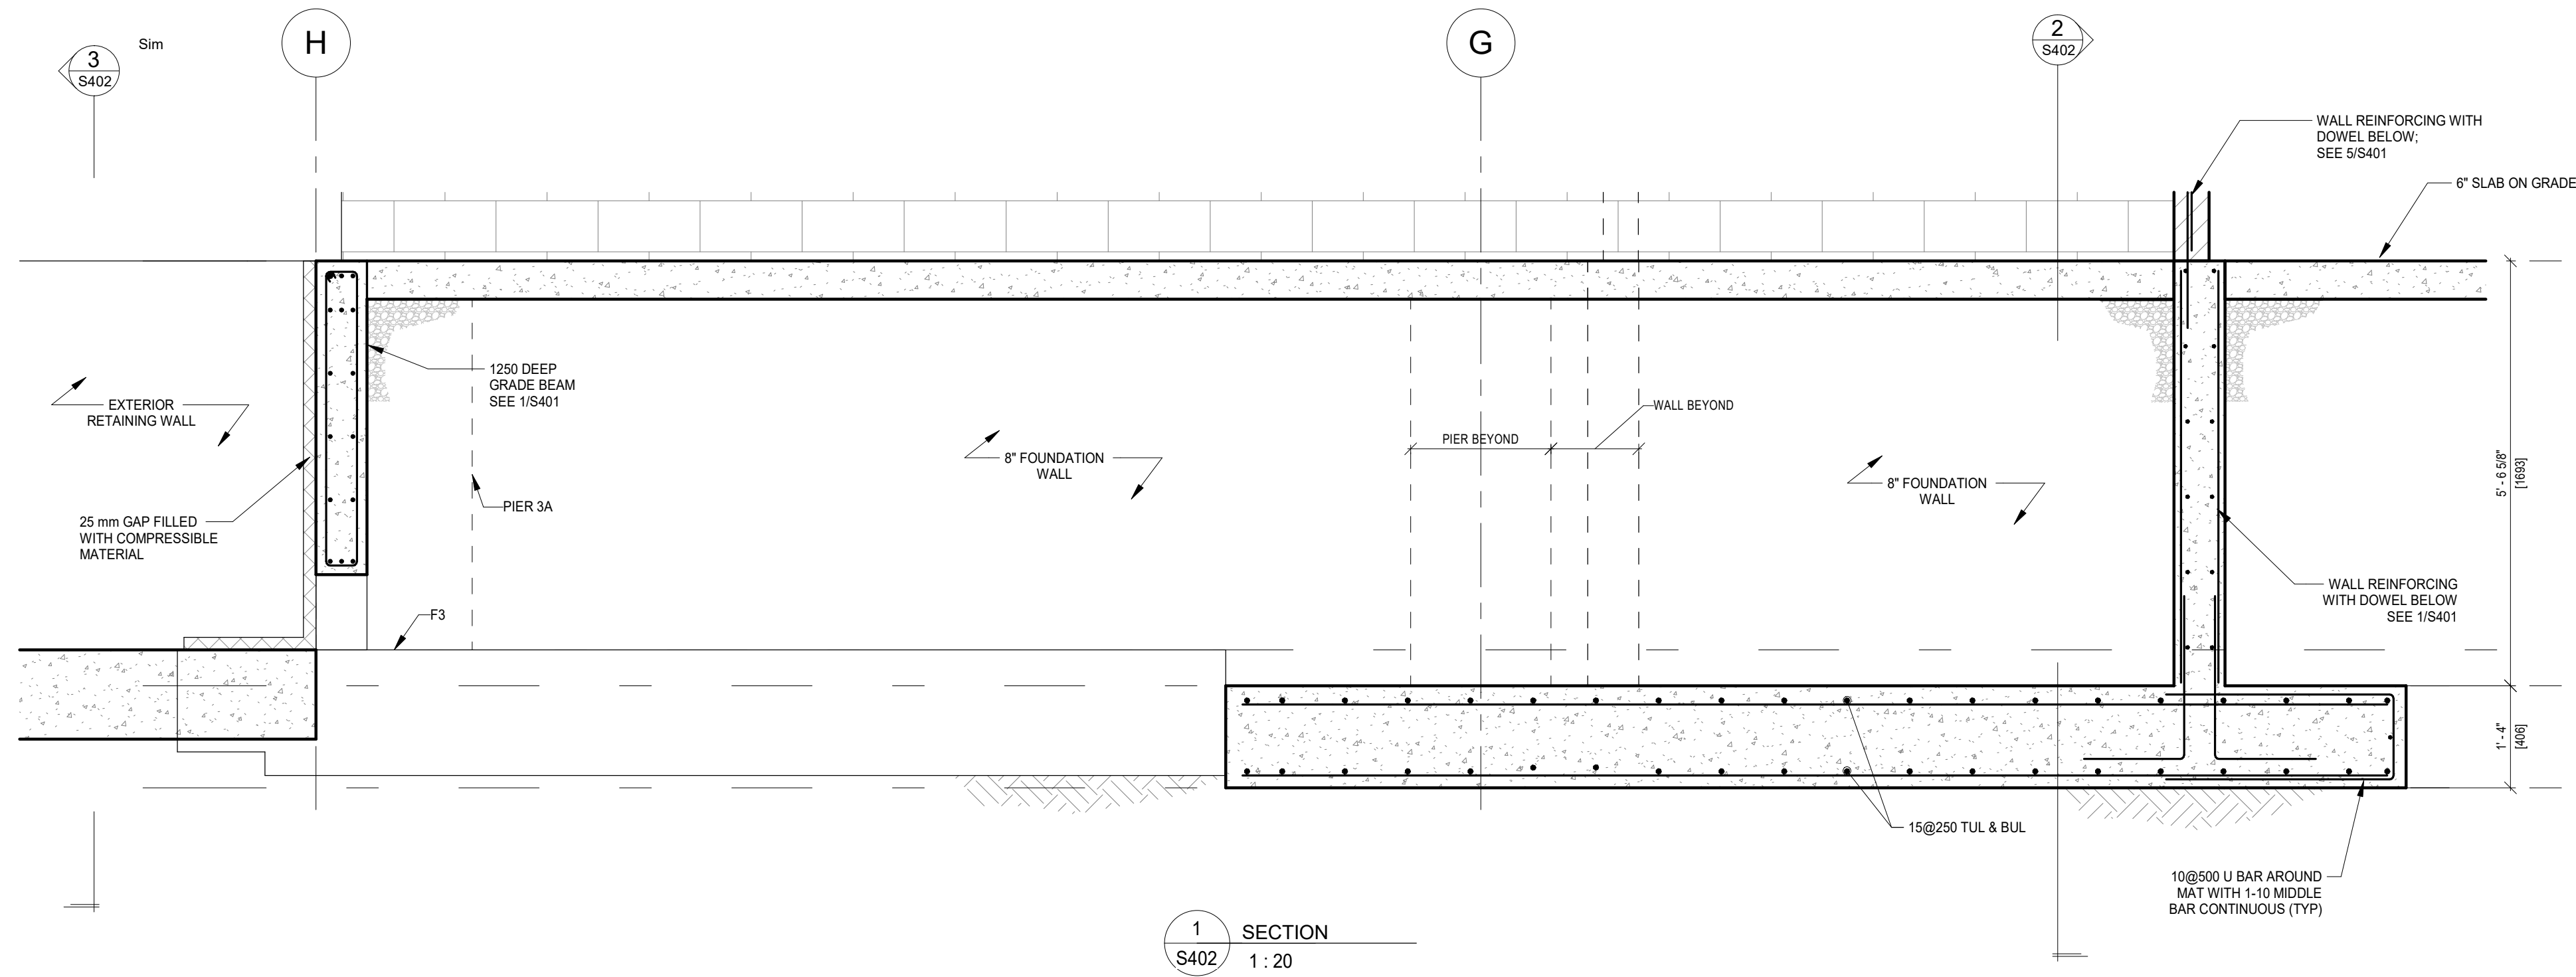

1	Issued for Permit	2024-11-14
2	Issued for Update	2025-01-26
3	Re-issued for Permit	2025-01-29
4	Issued for Construction	2025-03-21
5	Issued for Update	2025-05-23
6	Issued for Update	2025-06-11
7	Issued for Update	2025-06-26
8	Issued for Stairwall Remedial Work	2026-01-07
NO.	REVISIONS	DATE



4687 Queen Street Suite 2,
Niagara Falls, ON, L2E 2L9
T | 905-357-4441
F | 905-357-9203
W | www.raidondoarchitects.com
E | mail@raidondoarchitects.com

CLIENT NAME
1000115729 Ontario Limited
PROJECT NAME
Stanley Self Storage

PROJECT ADDRESS
228 Dunkirk Rd, St. Catharines, ON L2R 7K6
SHEET NAME
SECTIONS - BUILDING 'A'

DRAWN BY: LS
DATE: 2026-01-07 11:03:57 AM
SCALE: 1 : 20
PROJECT NO.: 23-229
CHECKED: RY

DRAWINGS ARE NOT VALID FOR CONSTRUCTION UNTIL SEALED AND SIGNED BY THE ARCHITECT.
DO NOT SCALE DRAWINGS. REPORT ALL DISCREPANCIES TO THE ARCHITECT BEFORE PROCEEDING. ALL DRAWINGS AND DESIGNS REMAIN THE PROPERTY OF THE ARCHITECT, AND ARE PROTECTED UNDER COPYRIGHT.

THESE DESIGN DOCUMENTS ARE PREPARED SOLELY FOR THE USE BY THE PARTY WITH WHOM THE DESIGN PROFESSIONAL HAS ENTERED INTO A CONTRACT AND THERE ARE NO REPRESENTATIONS OF ANY KIND MADE BY THE DESIGN PROFESSIONAL TO ANY PARTY WITH WHOM THE DESIGN PROFESSIONAL HAS NOT ENTERED INTO A CONTRACT.

SHEET #

S402

REV. #