




1 KEY PLAN
S200 1:100

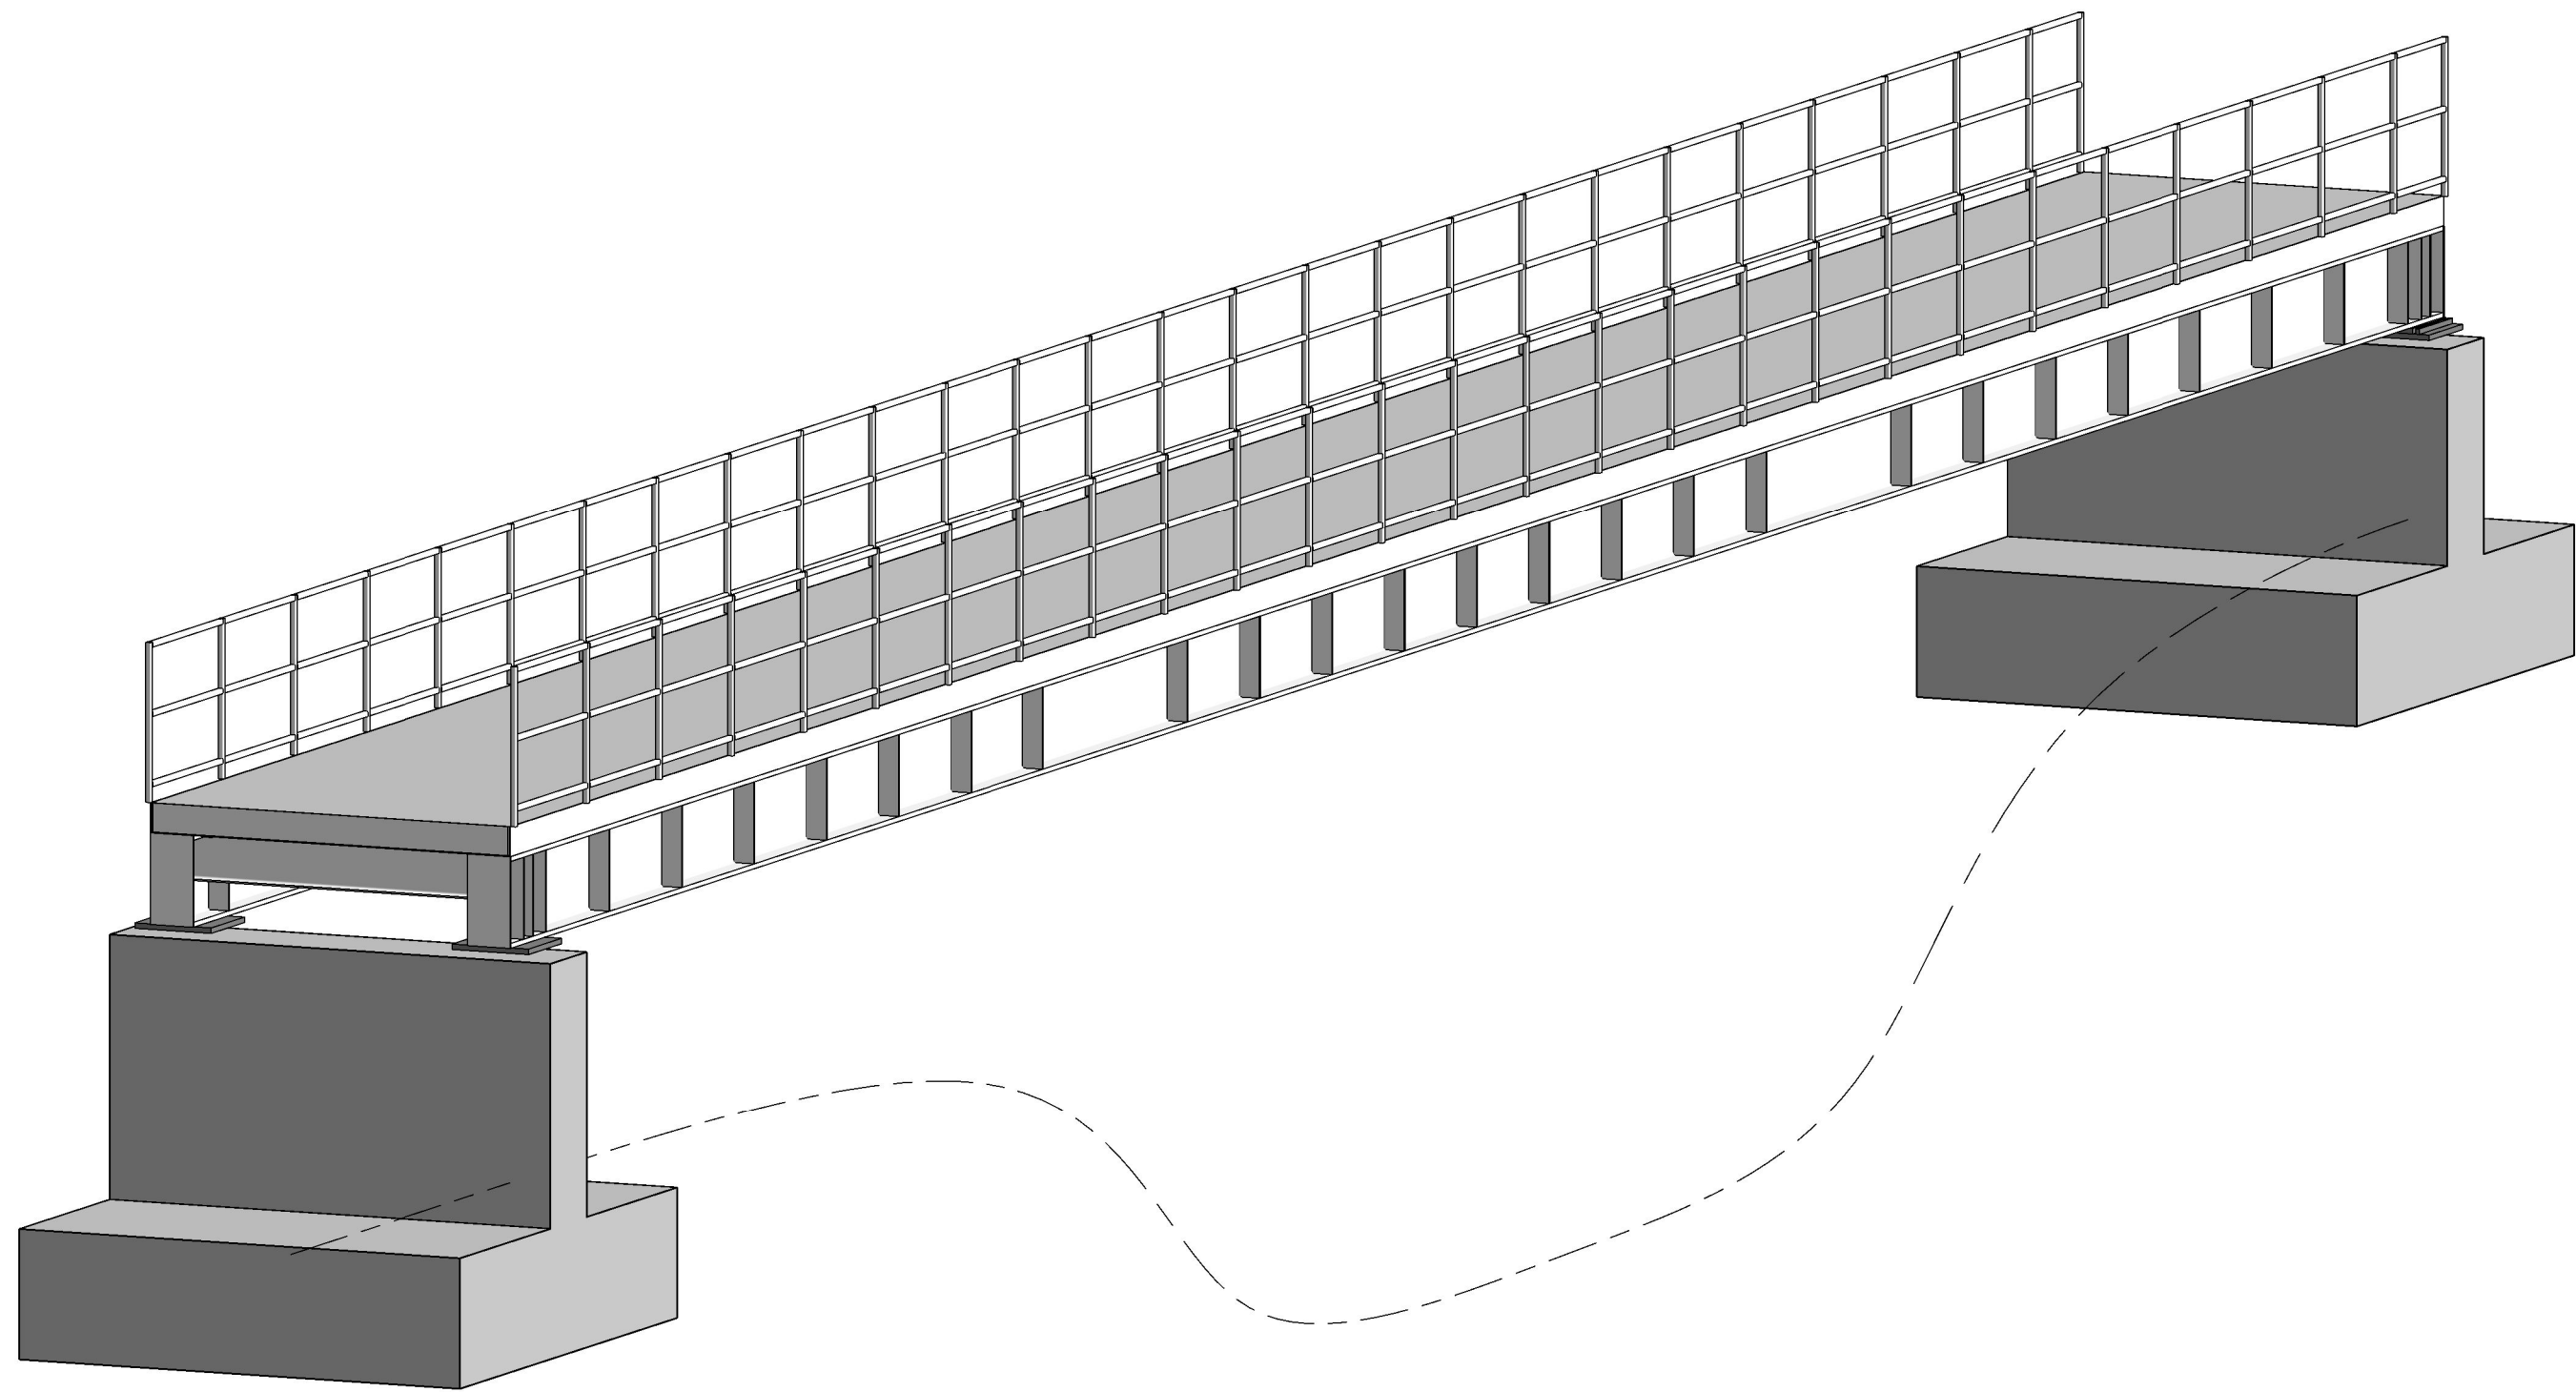

2 PERSPECTIVE
S200

- GENERAL NOTES:**
- A. GENERAL**
- THIS PROJECT SHALL COMPLY WITH THE REQUIREMENTS OF THE ONTARIO STANDARD SPECIFICATIONS FOR BRIDGE CONSTRUCTION, EXCEPT AS MODIFIED BY THE PLANS AND SPECIAL PROVISIONS.
 - THE STRUCTURAL DRAWINGS SHALL BE READ WITH OTHER CONTRACT DOCUMENTS. ONLY DIMENSIONS RELEVANT TO STRUCTURAL ELEMENTS ARE SHOWN ON STRUCTURAL DRAWINGS. FOR OTHER DIMENSIONS AND SIZES NOT SHOWN, REFER TO THE OTHER CONTRACT DRAWINGS.
 - THE CONTRACTOR SHALL BE RESPONSIBLE FOR FULLY UNDERSTANDING THE NATURE OF WORK AND CONDITIONS UNDER WHICH THE WORK WILL BE PERFORMED.
 - REMOVE ALL EXISTING STRUCTURE AND DEBRIS FROM THE OLD BRIDGE PRIOR TO THE COMMENCEMENT OF THE PROPOSED BRIDGE CONSTRUCTION.
- B. STRUCTURE**
- STRUCTURAL STEEL SHALL BE NEW CARBON STRUCTURAL STEEL CSA G40 21 GRADE 300W.
 - STRUCTURAL STEEL SHALL BE GALVANIZED INCLUDING ANCHOR ROD, WASHER, AND NUT.
 - USE NELSON HEADED FOR SHEAR STUDS AND F1654 GRADE 65 FOR ANCHOR RODS.
 - DESIGN AND PERFORM WELDING IN ACCORDANCE WITH CSA W59.1.
 - PROVIDE DECK CLOSURE PLATES AT ALL EDGES.

RESERVED FOR AUTHORITY STAMP

ISSUED FOR RECORD
DATE

Client:



245 Markland Drive, Toronto, Ontario M6C 1R1
marklandwood.com | (416) 621-0200

Structural Consultants:



891 Yonge Street, Suite 303, Toronto, Ontario, Canada M4Y 3P4
T: 416.961.8256 | F: 416.961.7434
e: qdres@quindressel.com | www.quindressel.com

CONTRACTOR SHALL CHECK ALL DIMENSIONS ON THE WORK AND REPORT ANY DISCREPANCY TO THE CONSULTANT BEFORE PROCEEDING. THIS DRAWING IS NOT TO BE USED FOR CONSTRUCTION UNTIL AUTHORIZED IN WRITING BY CONSULTANT.

3 2026-02-11 ISSUED FOR RECORD
1 2025-02-24 ISSUED FOR CLIENTS REVIEW
DATE PREVISION

NOT FOR
CONSTRUCTION

MARKLAND WOOD GOLF CLUB-ELEVATED PATHWAY

PROJECT ADDRESS:
245 MARKLAND DRIVE, TORONTO, ONTARIO M6C 1R1

PROJECT CLIENT:
MARKLAND WOOD GOLF CLUB

SCALE 1:100
DRAWN BY JC
REVIEWED BY RY
PROJECT NUMBER 24-172
PLOT DATE 2026-02-11 2:07:53 PM

PROPOSED BRIDGE DETAIL

DRAWING NUMBER
S200

NOTE: ALL EXTERIOR STRUCTURAL STEEL INCLUDING ANCHOR ROD, WASHER AND NUT SHALL BE GALVANIZED.

RESERVED FOR AUTHORITY STAMP

ISSUED FOR RECORD	2025-02-11
DATE	

Client:



245 Markland Drive, Toronto, Ontario M5C 1R1
markland@aol.com, 1 (416) 621-2280

Structural Consultants



890 Yonge Street, Suite 300, Toronto, Ontario, Canada M4W 3P4
t: 416.961.8294 | f: 416.961.7434
e: drawings@quindressel.com | www.quindressel.com

CONTRACTOR SHALL CHECK ALL DIMENSIONS ON THE WORK AND REPORT ANY DISCREPANCY TO THE CONSULTANT BEFORE PROCEEDING. THIS DRAWING IS NOT TO BE USED FOR CONSTRUCTION UNTIL AUTHORIZED IN WRITING BY CONSULTANT.

3	2026-02-11	ISSUED FOR RECORD
2	2025-01-26	ISSUED FOR UPDATE
1	2025-01-24	ISSUED FOR CLIENTS REVIEW
#	DATE	REVISION


NOT FOR
CONSTRUCTION

MARKLAND WOOD GOLF CLUB-ELEVATED PATHWAY


SCALE	As Indicated
DRAWN BY	JC
REVIEWED BY	RY
PROJECT NUMBER	24-172
PLOT DATE	2025/02/11 3:17:05 PM

PROPOSED ELEVATED PATHWAY


DRAWING NUMBER **S201**

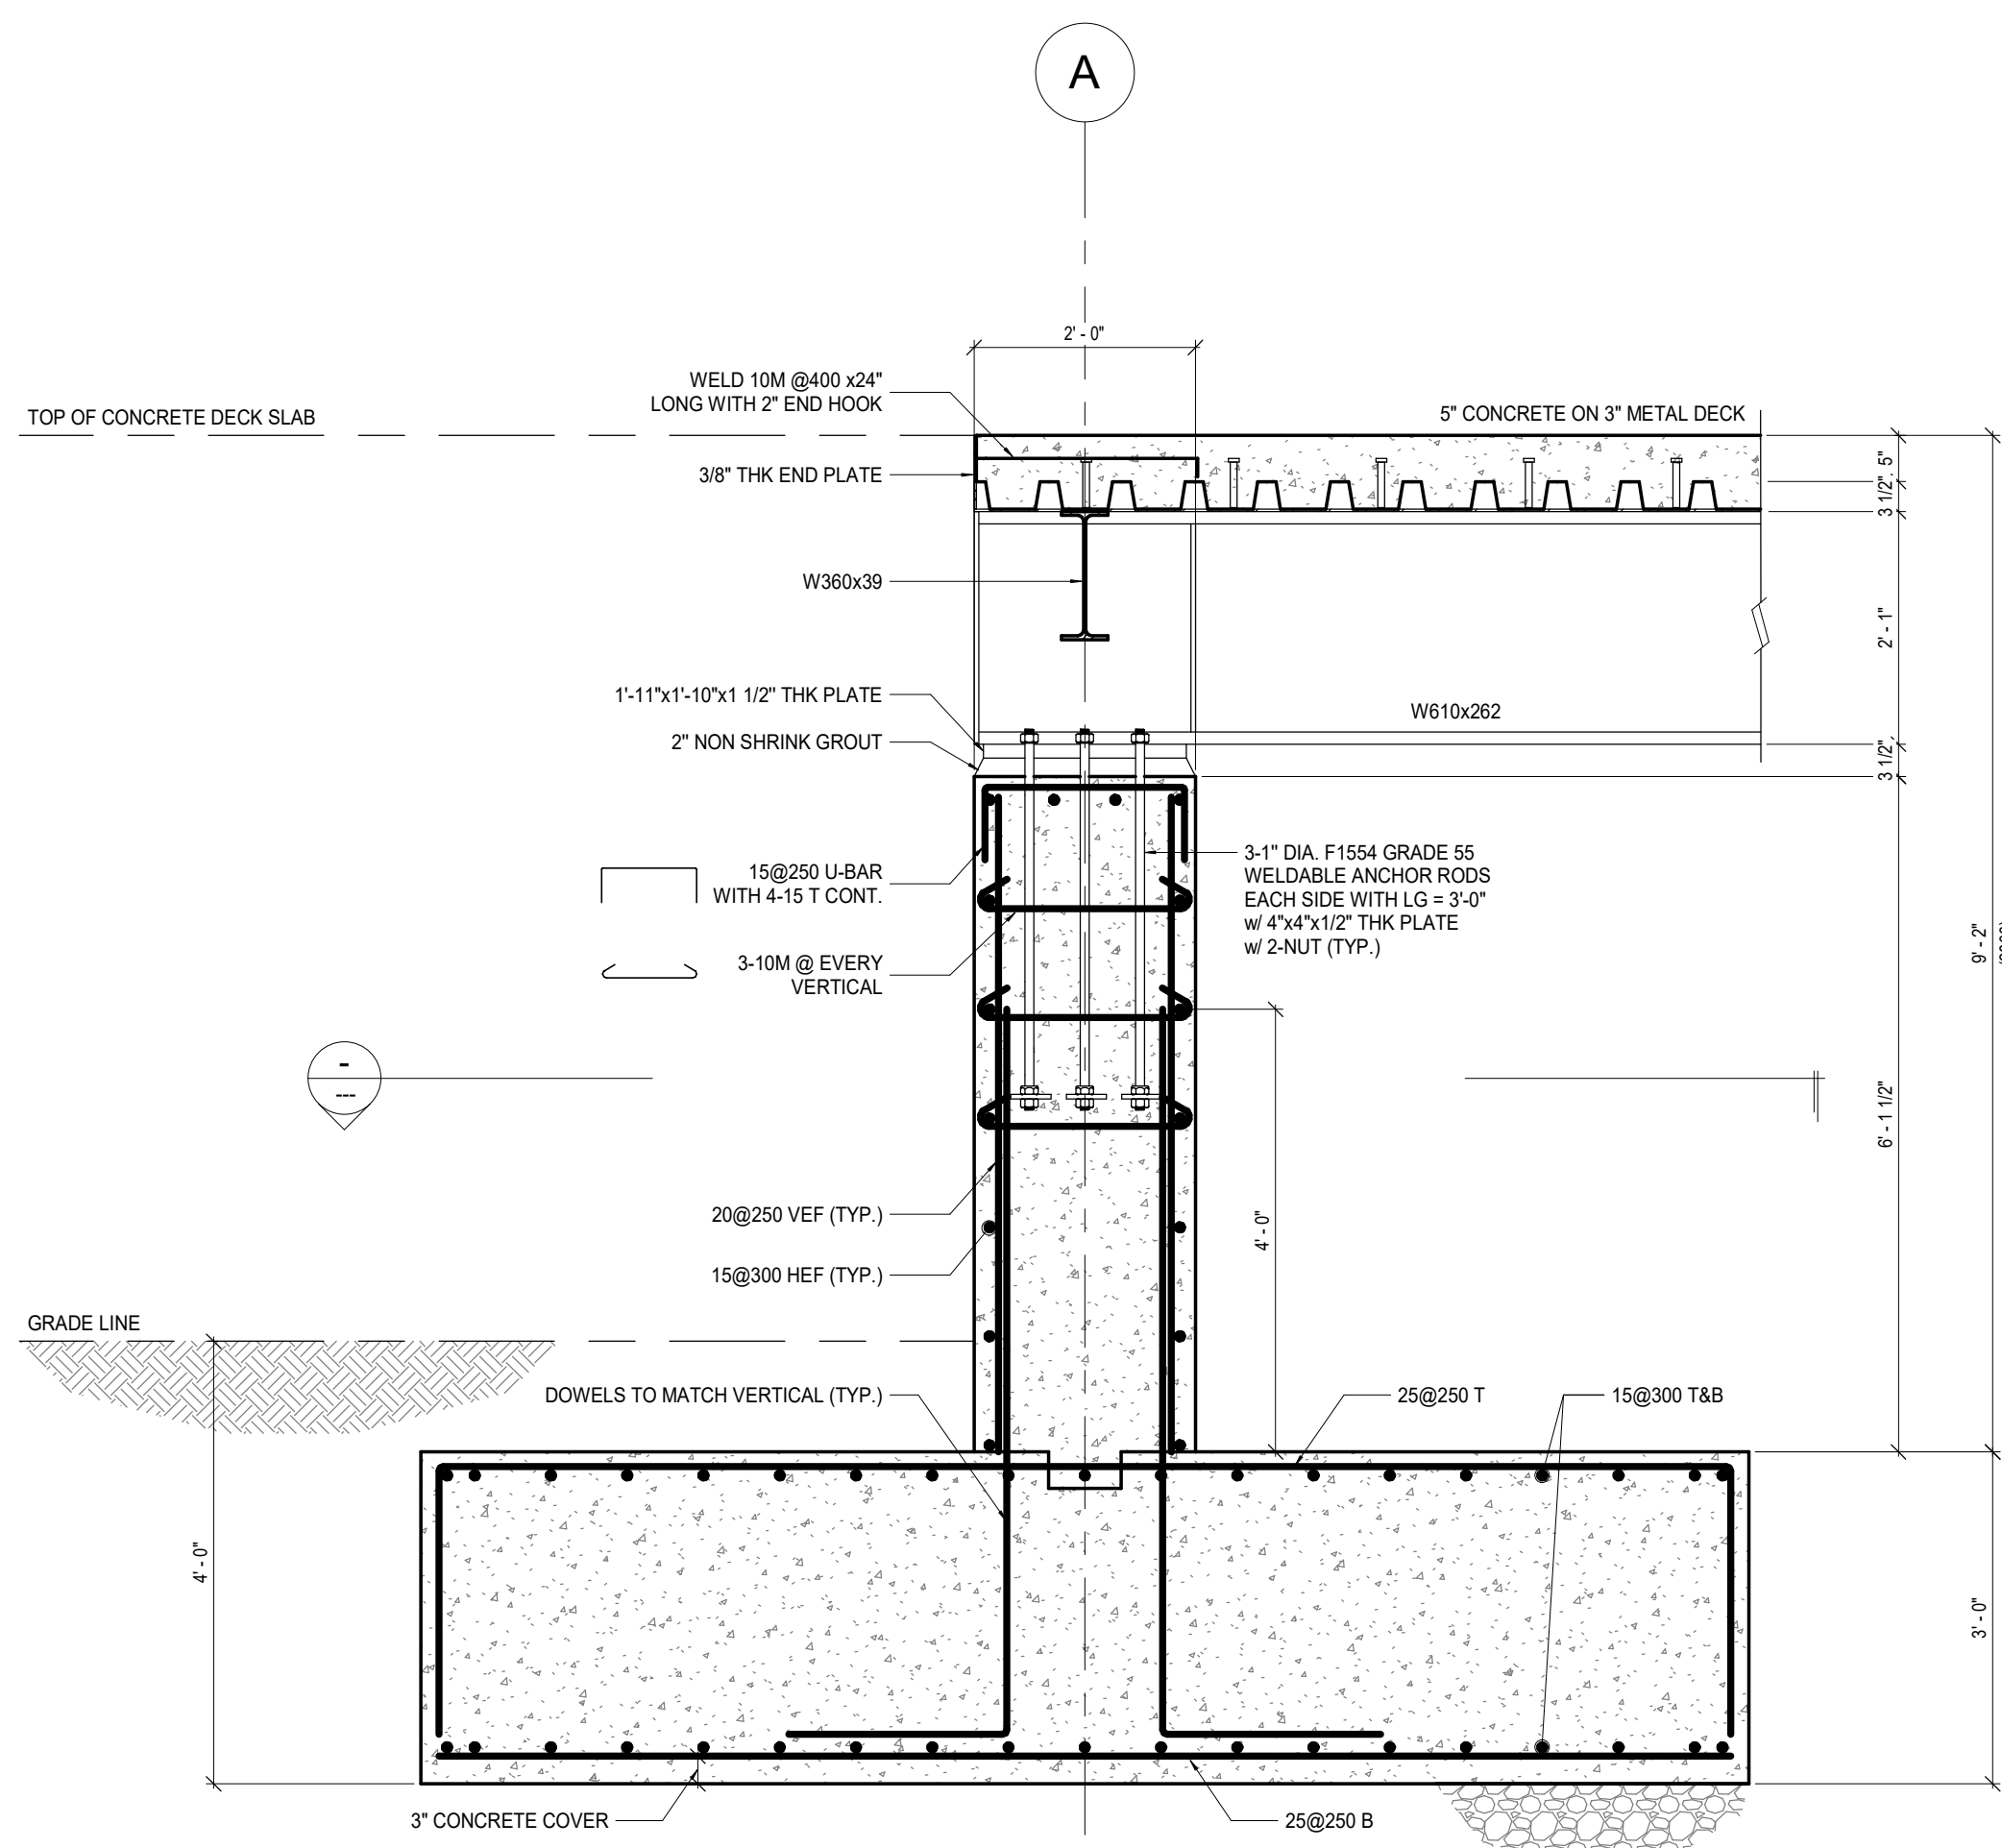


1 FIXED END CONNECTION
S301 1:20

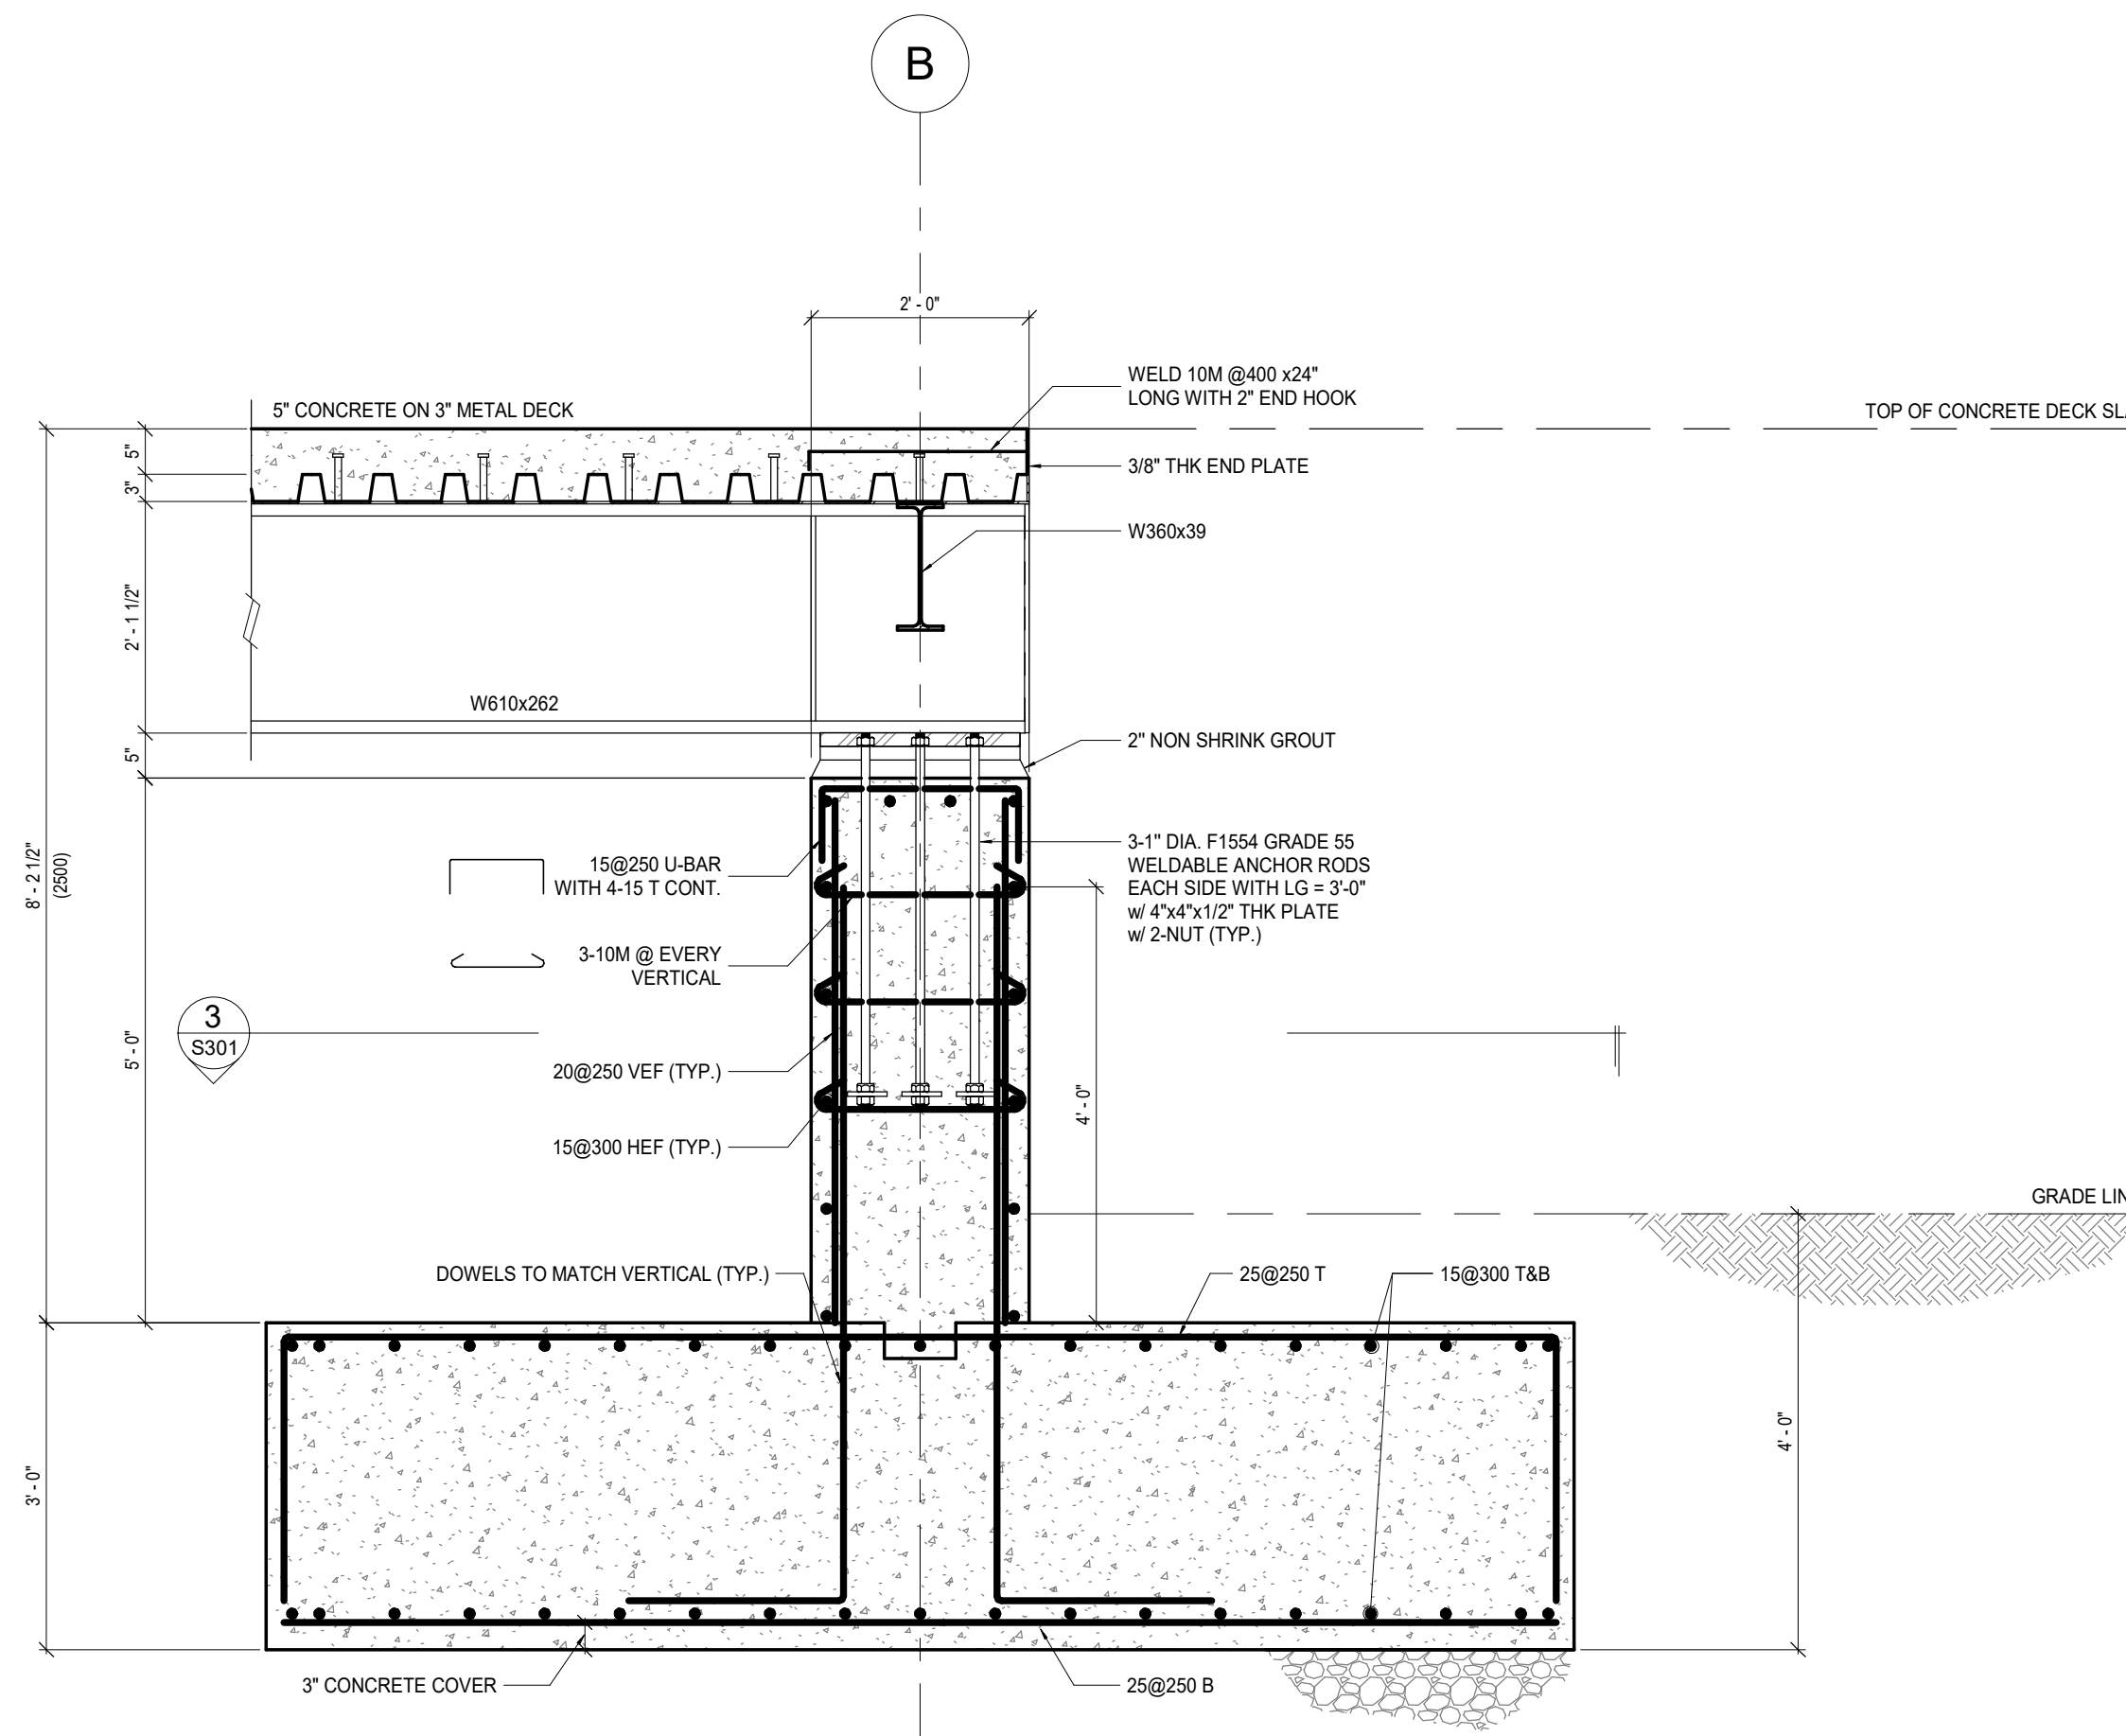


2 SLIDING END CONNECTION
S301 1:20

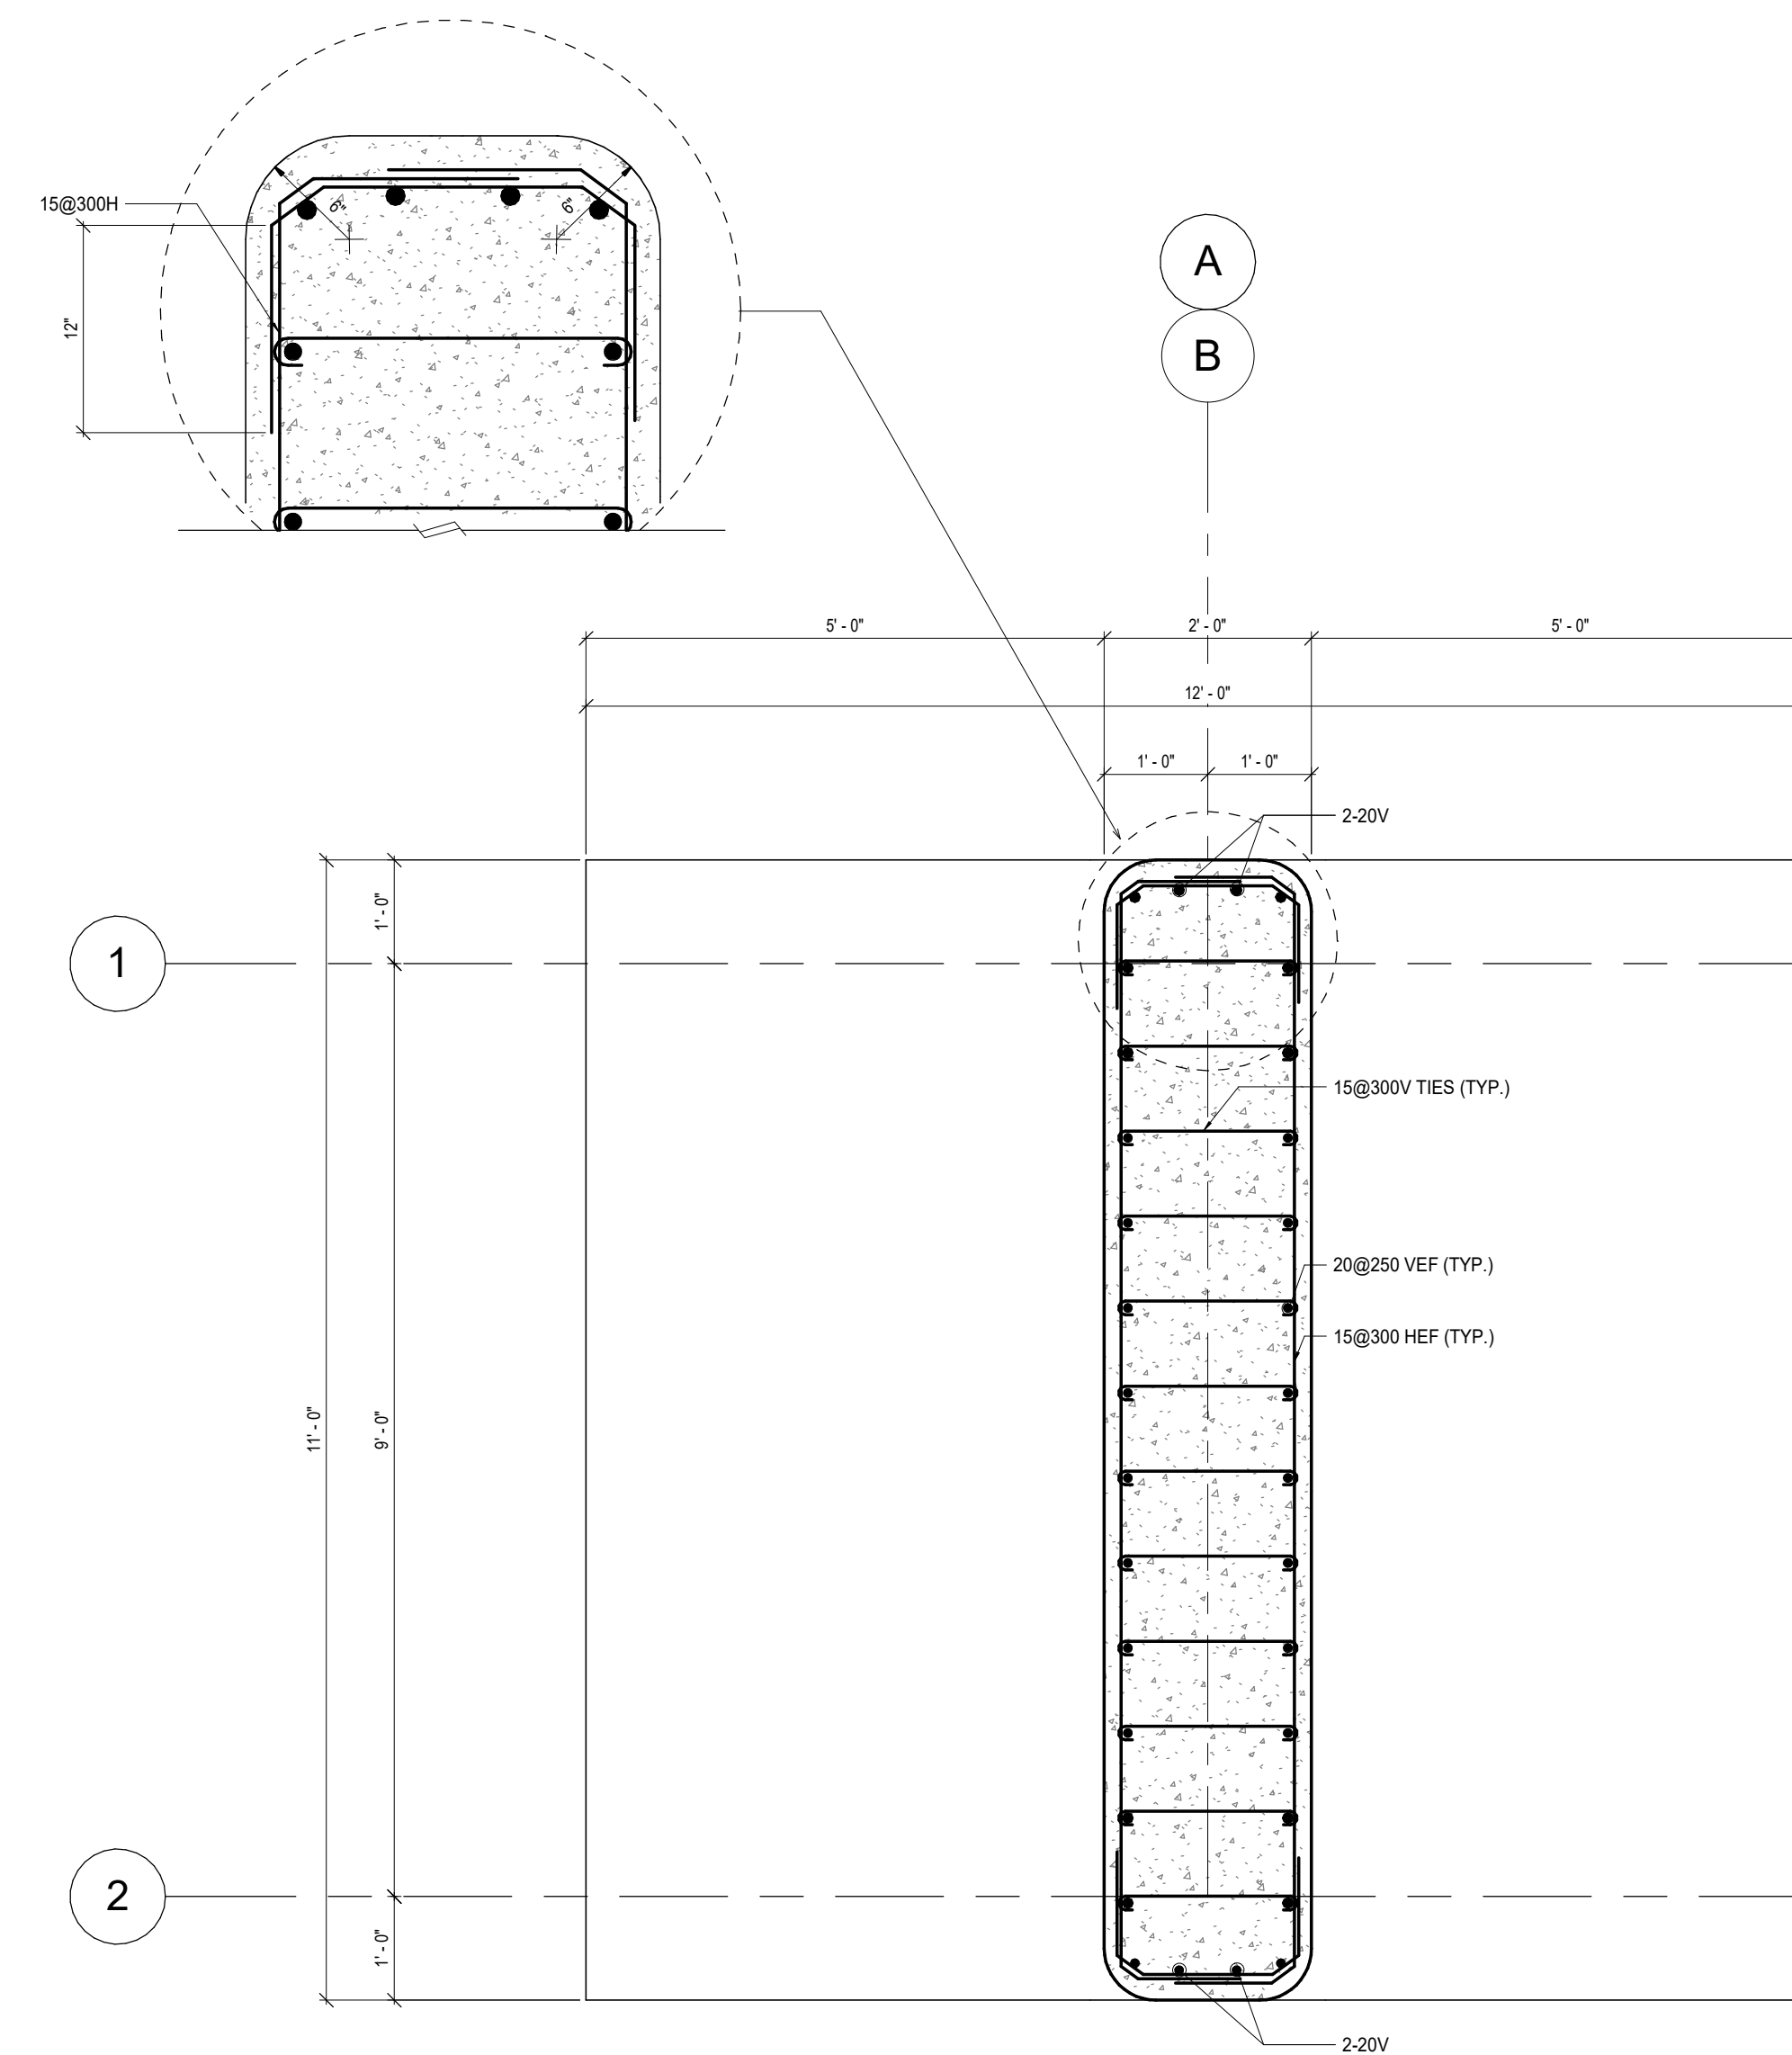

3 SECTION
S301 1:20

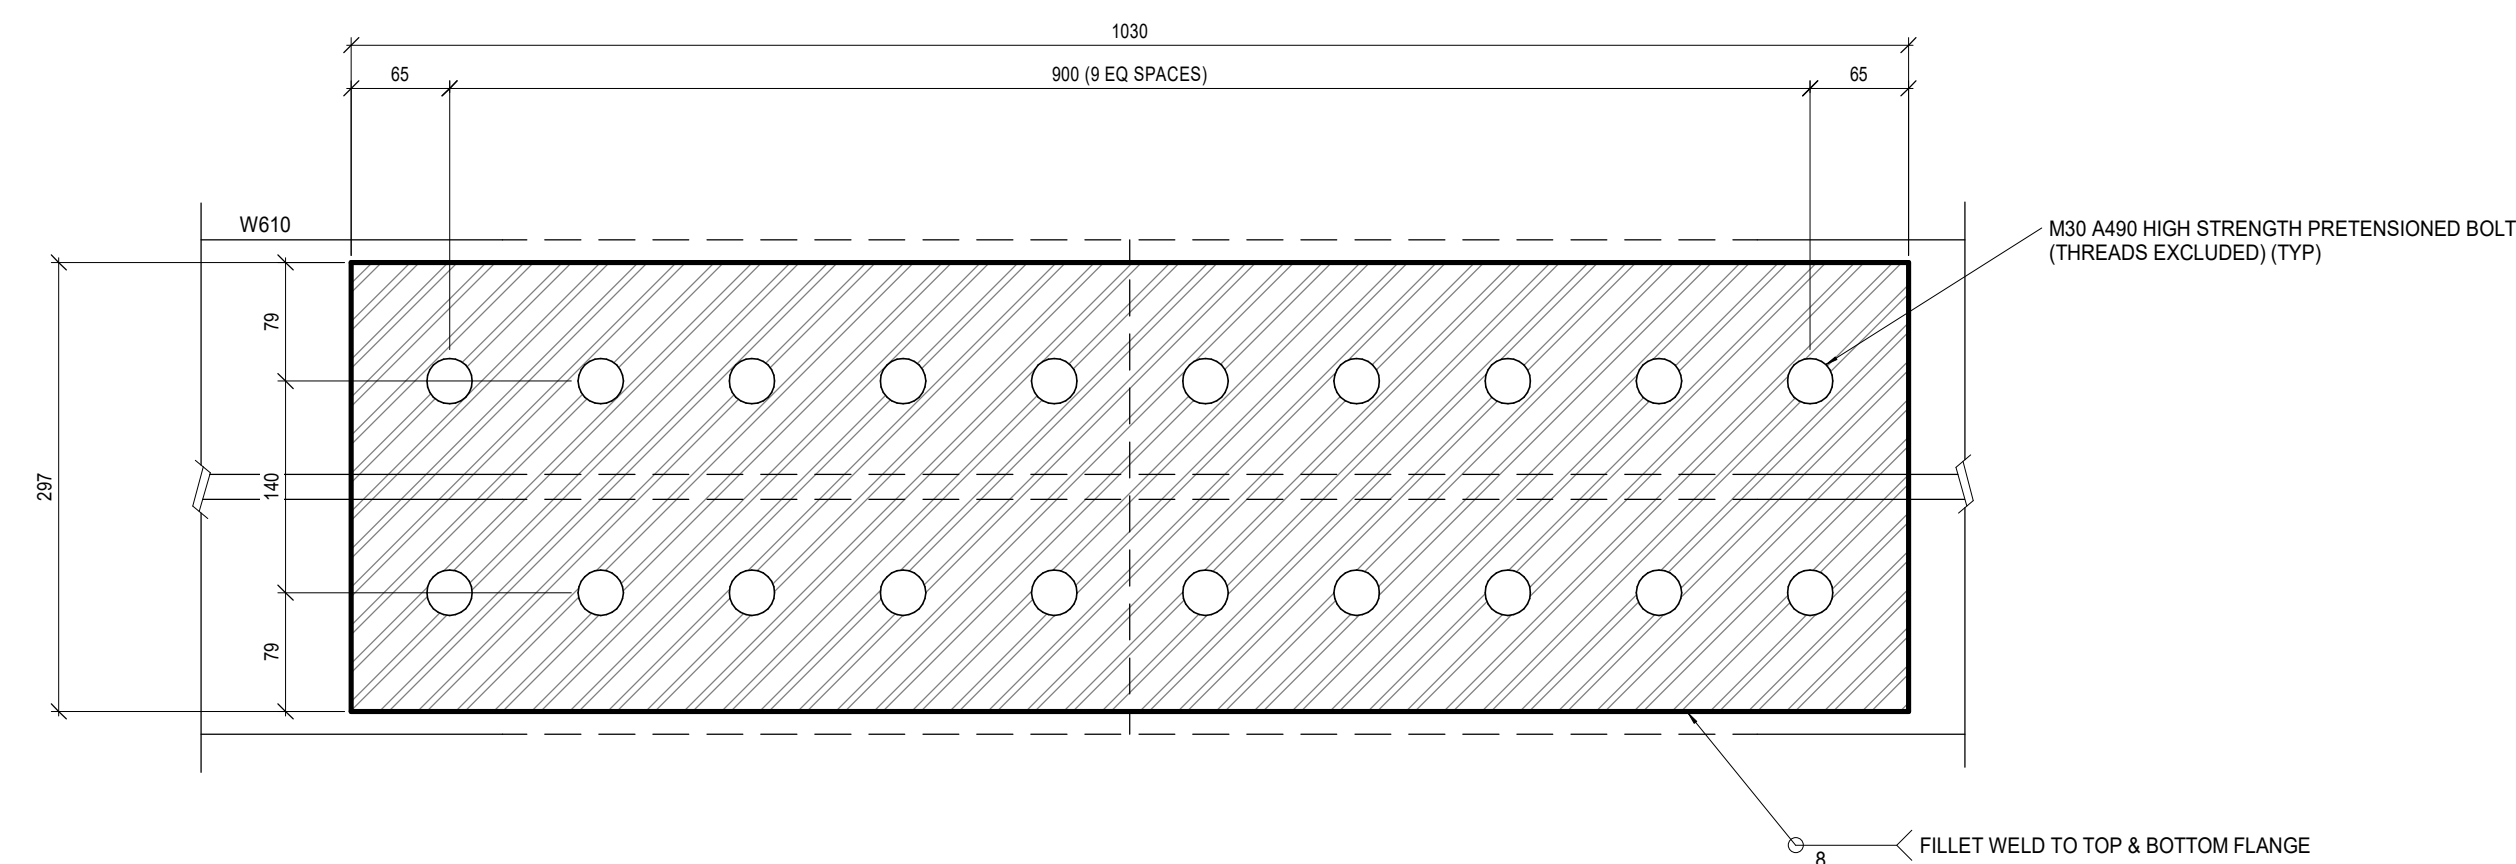


TOP AND BOTTOM PLATE
PL 307x20x1030 (Fy = 50 MPa)

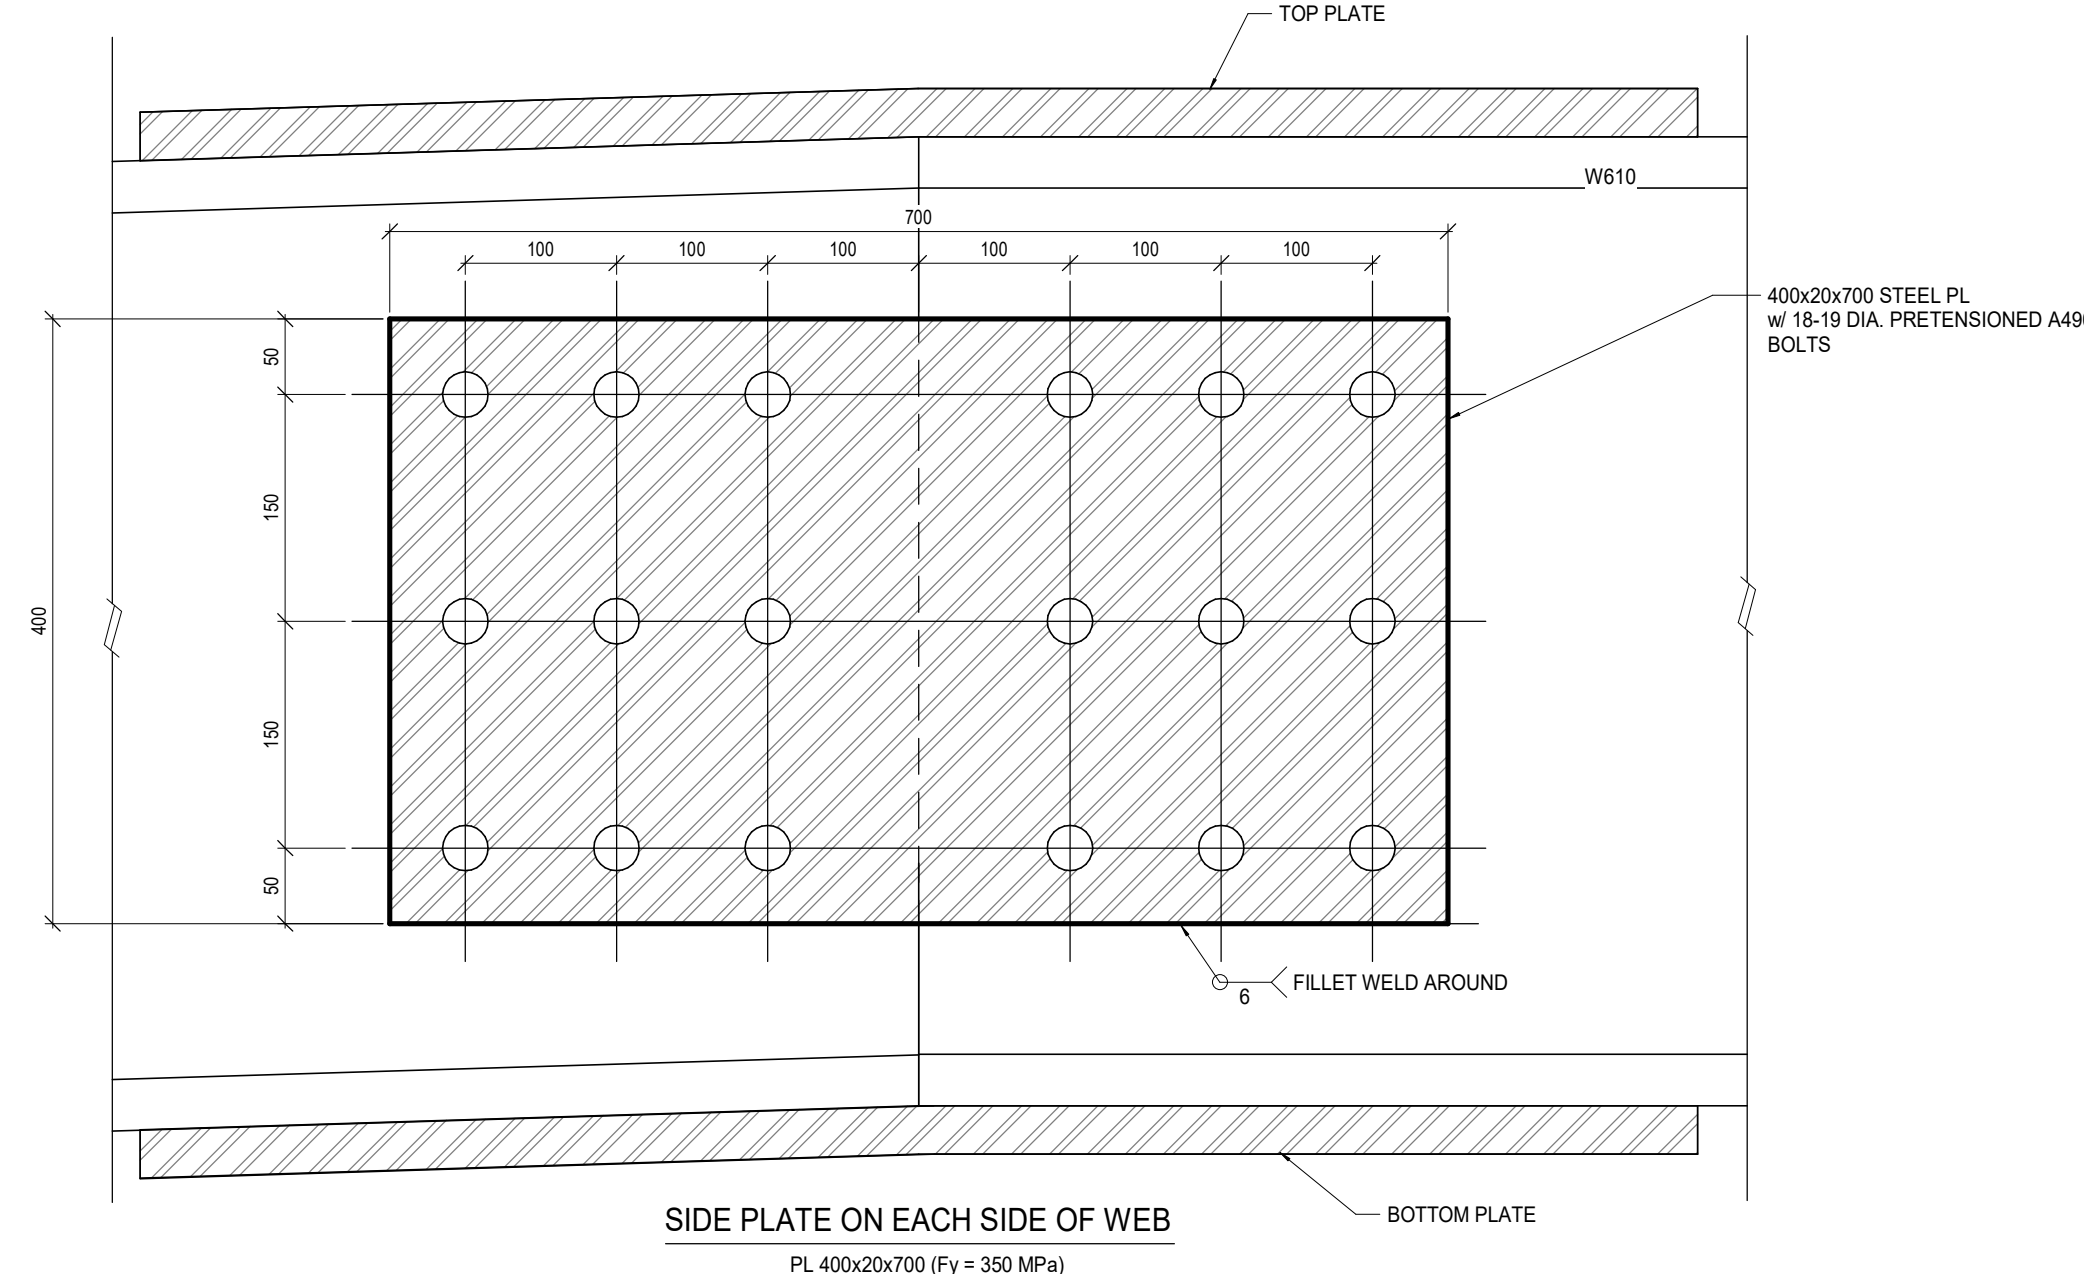


6 SPLICE CONNECTION PLATE DETAILS
S301 1:5

NOTES:
1. A990 BOLTS SHALL BE PROVIDED WITH WEATHERING STEEL FINISH OR COATING.
2. ALL STRUCTURAL STEEL SHALL BE GALVANIZED.

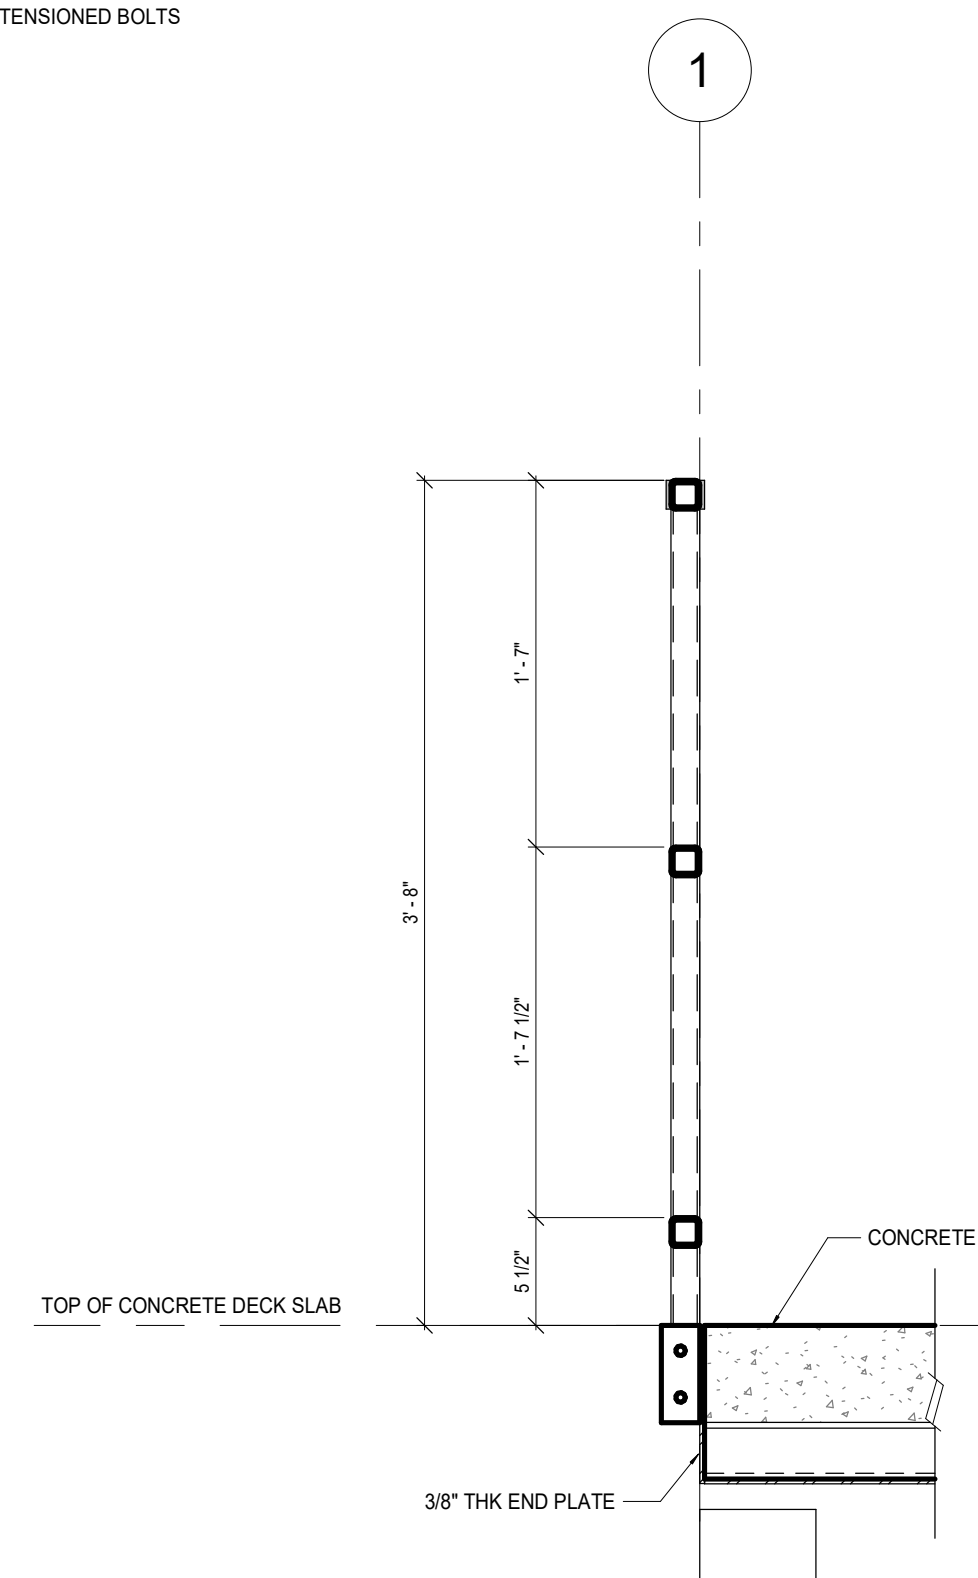

4 SECTION
S301 1:10

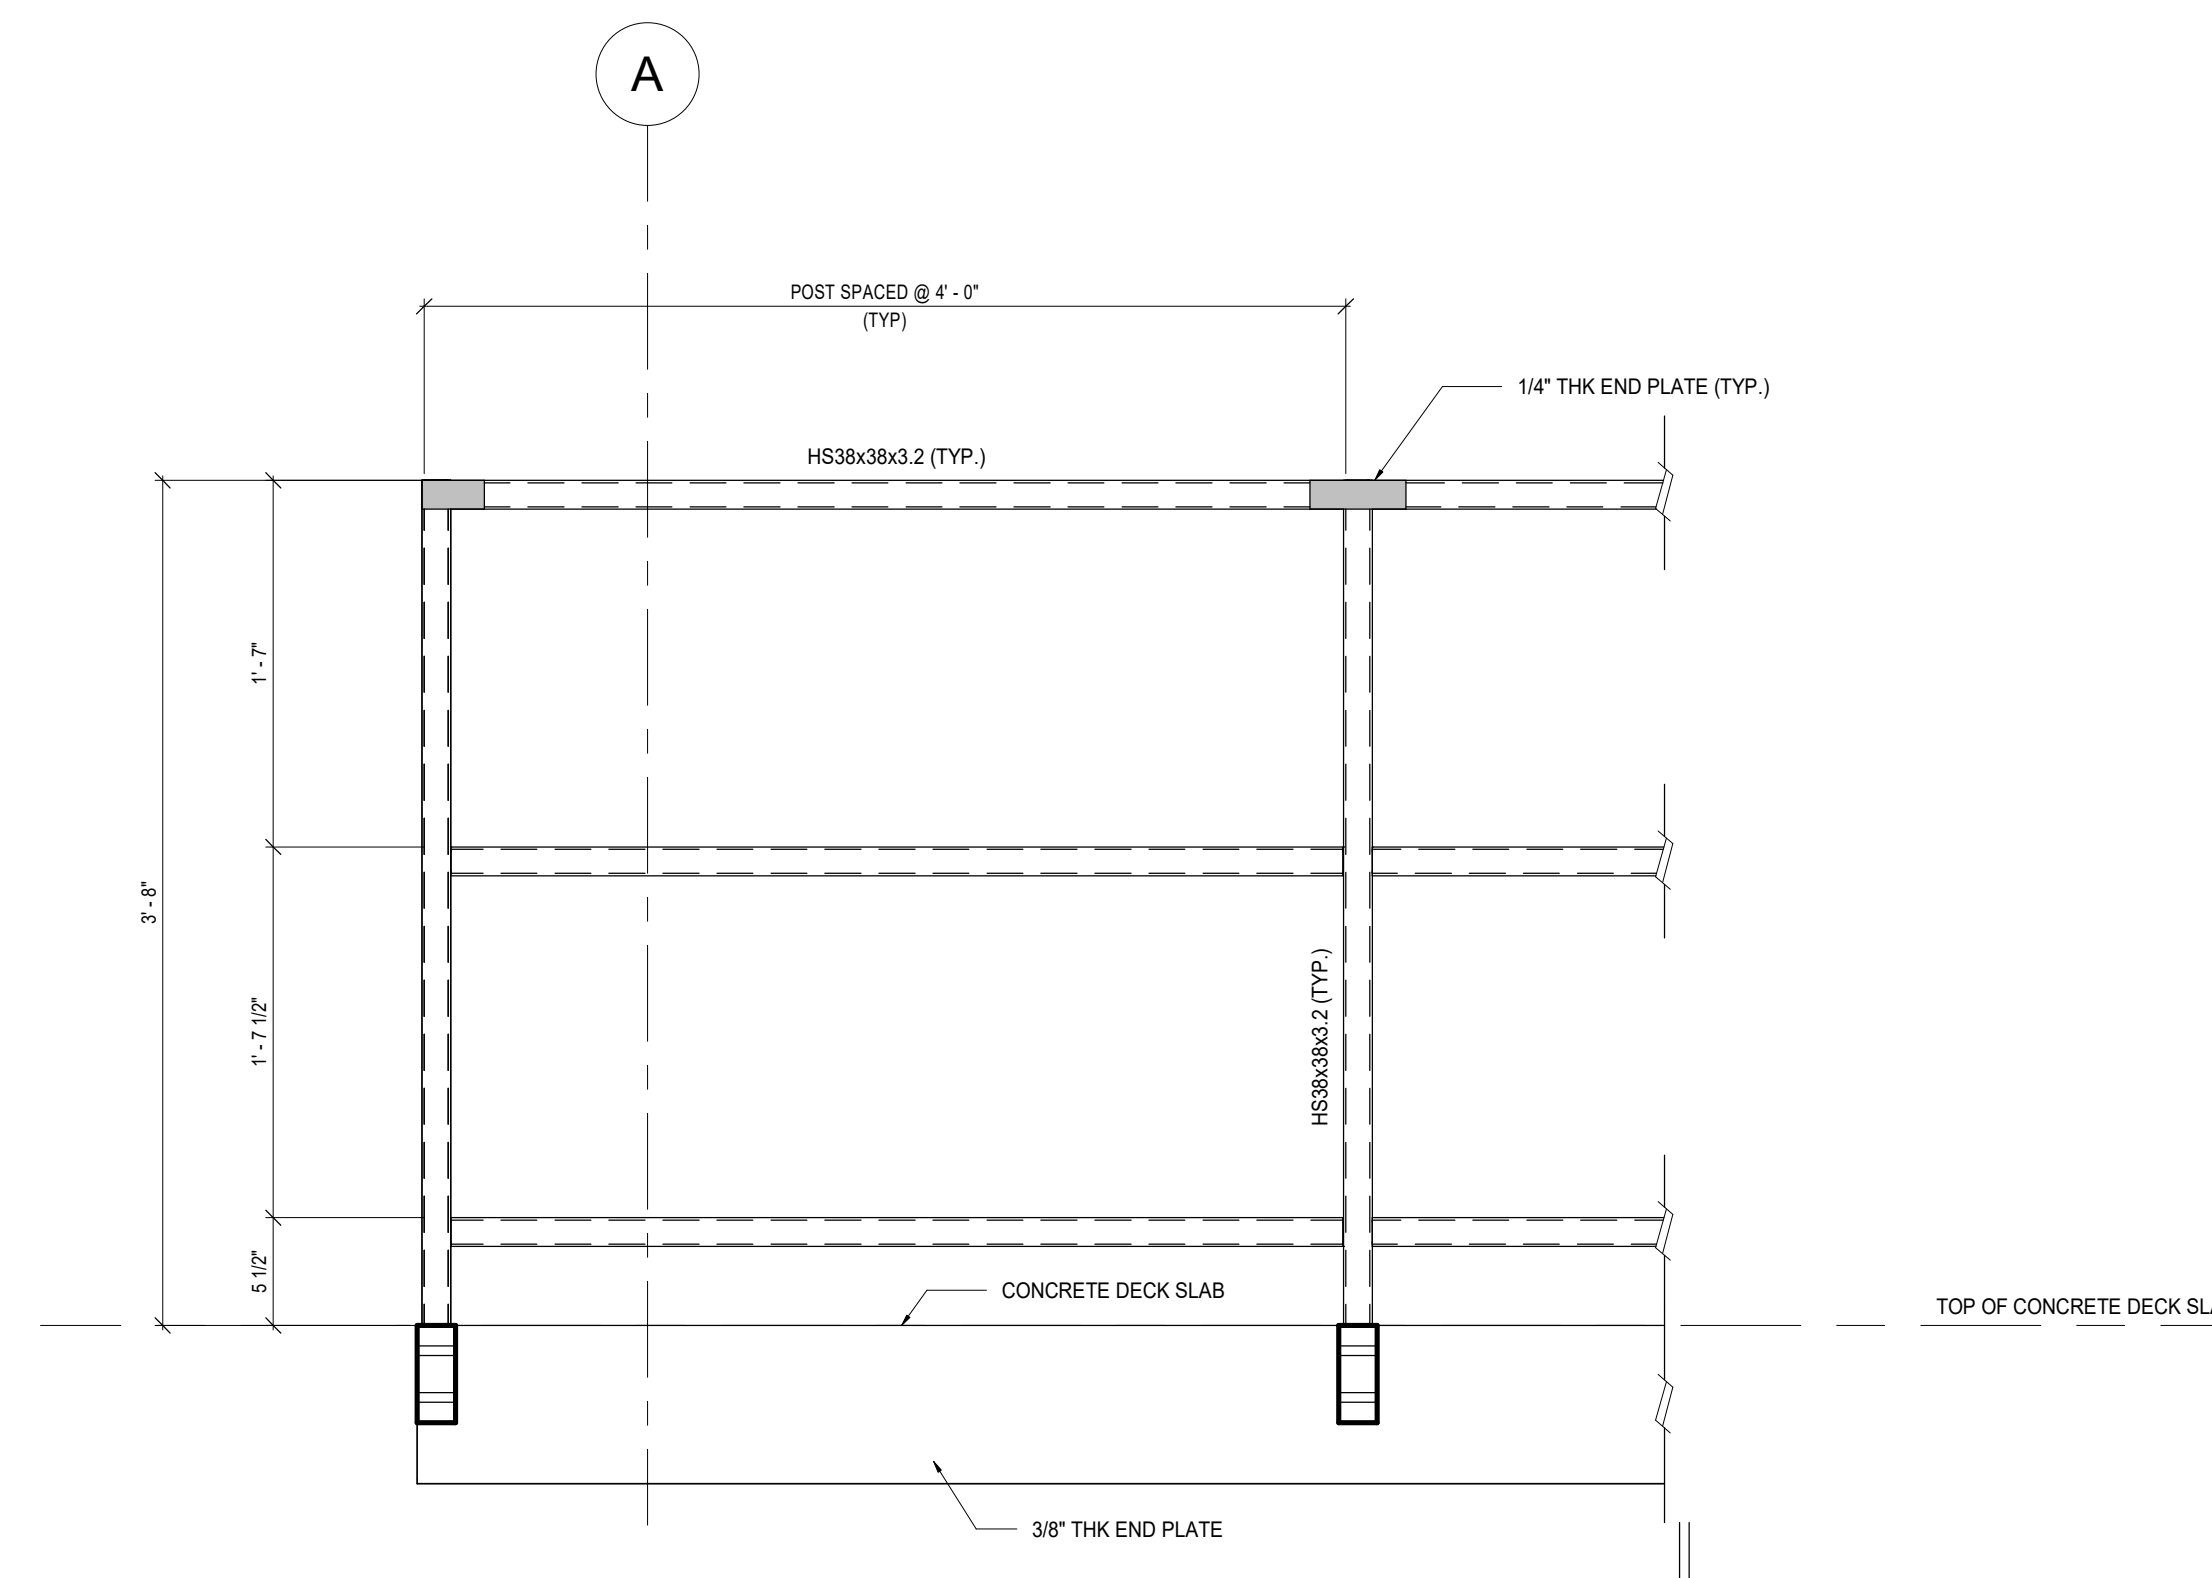

5 STEEL RAILING DETAILS
S301 1:10

NOTES:
1. ALL EXTERIOR STRUCTURAL STEEL INCLUDING ANCHOR ROD, WASHER AND NUT SHALL BE GALVANIZED.
2. THE FOOTING SHALL BE FOUND ON UNDISTURBED SOIL WITH ALLOWABLE BEARING PRESSURE = 75 KPa; SEE THE GEOTECHNICAL INVESTIGATION REPORT PREPARED BY GEOTERRE LIMITED ON APRIL 05, 2016 WITH FILE # TG15-007.

RESERVED FOR AUTHORITY STAMP

ISSUED FOR RECORD 2026-02-11
DATE

Client:



245 Markland Drive, Toronto, Ontario M6C 1R1
marklandwood.com | (416) 621-2255

Structural Consultants:



897 Yonge Street, Suite 300, Toronto, Ontario, Canada M4W 3P4
1-416-961-8256 | 1-416-961-7434
q.dressel@quinn-dressel.com | www.quinn-dressel.com

CONTRACTOR SHALL CHECK ALL DIMENSIONS ON THE WORK AND REPORT ANY DISCREPANCIES TO THE CONSULTANT BEFORE PROCEEDING. THIS DRAWING IS NOT TO BE USED FOR CONSTRUCTION UNTIL AUTHORIZED IN WRITING BY CONSULTANT.

NO.	DATE	REVISION
3	2026-02-11	ISSUED FOR RECORD
2	2025-04-28	ISSUED FOR UPDATE
1	2025-02-24	ISSUED FOR CLIENTS REVIEW
#	DATE	REVISION

NOT FOR
CONSTRUCTION

MARKLAND WOOD GOLF CLUB-ELEVATED PATHWAY

PROJECT ADDRESS:
245 MARKLAND DRIVE, TORONTO, ONTARIO M6C 1R1
PROJECT CLIENT:
MARKLAND WOOD GOLF CLUB

SCALE: As Indicated
DRAWN BY: JC
REVIEWED BY: RT
PROJECT NUMBER: 24-172
PLOT DATE: 2026-02-11 3:27:37 PM


PROPOSED ELEVATED PATHWAY

DRAWING NUMBER

S301




1 PATHWAY GIRDER ELEVATION AND PIECE DRAWING
S302 1:50

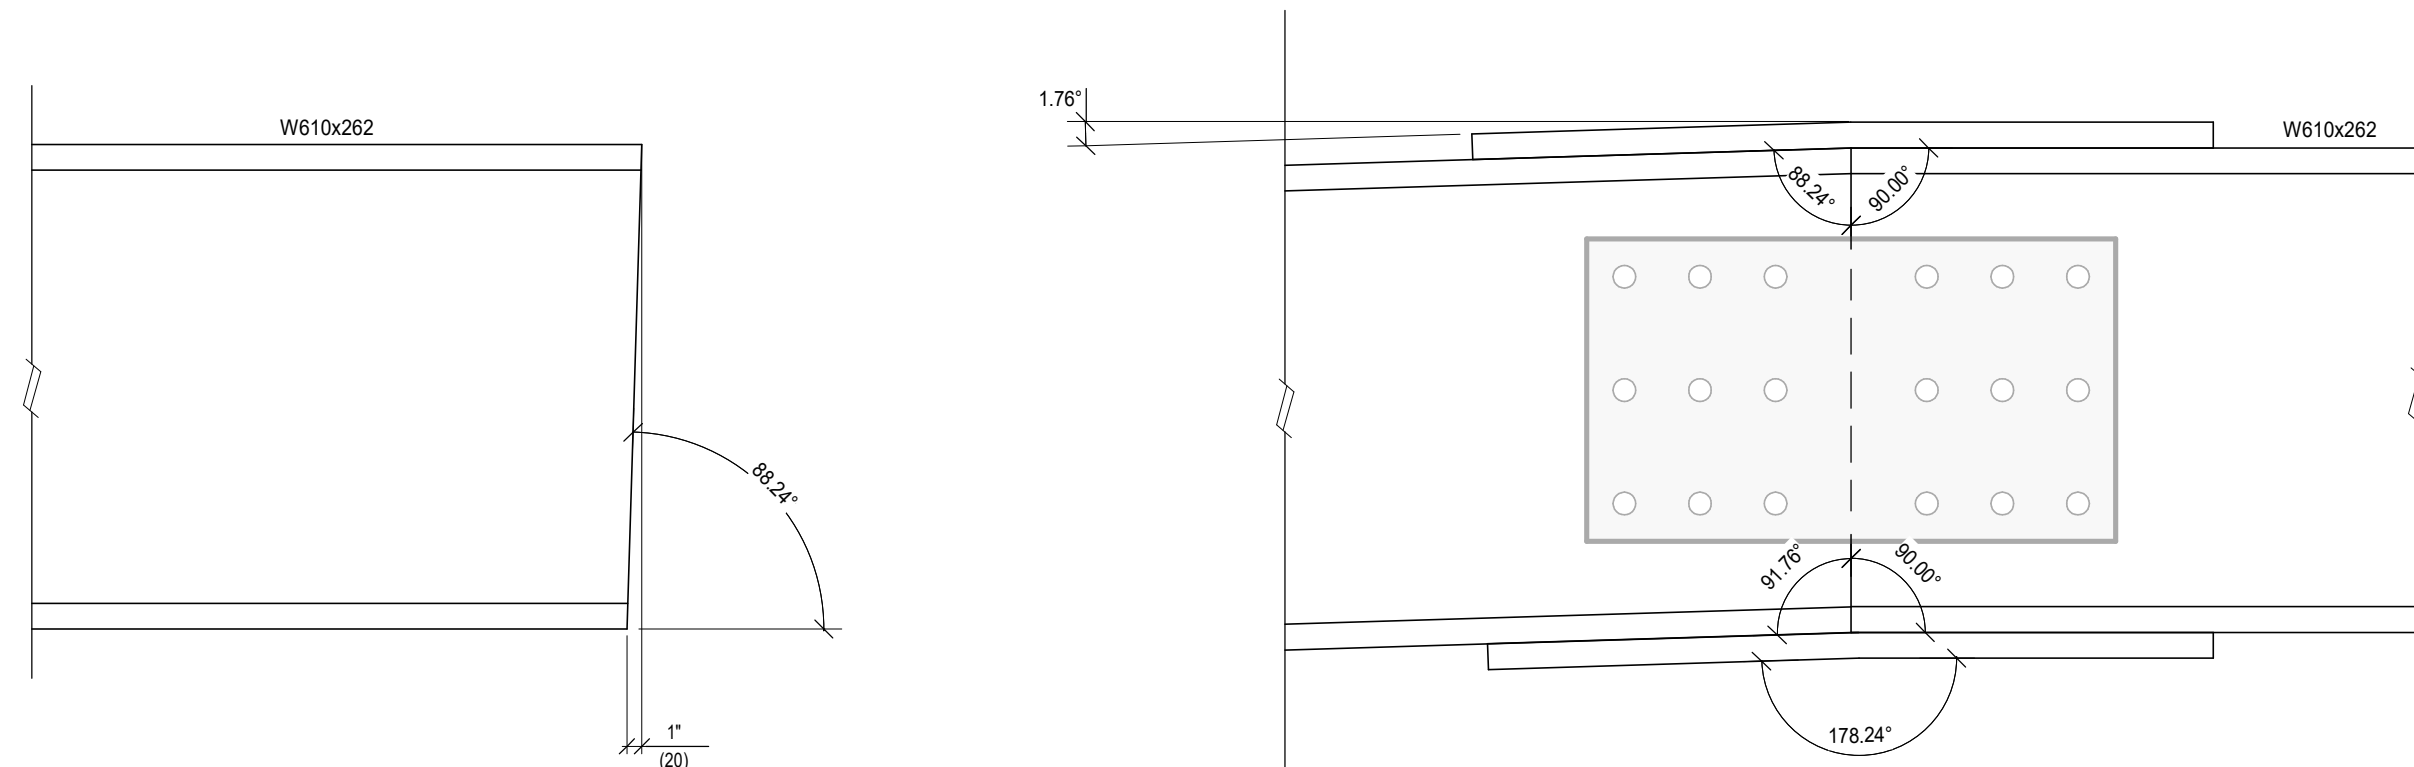

2 CUT DETAIL
S302 1:10

3 SPLICE GEOMETRY
S302 1:10

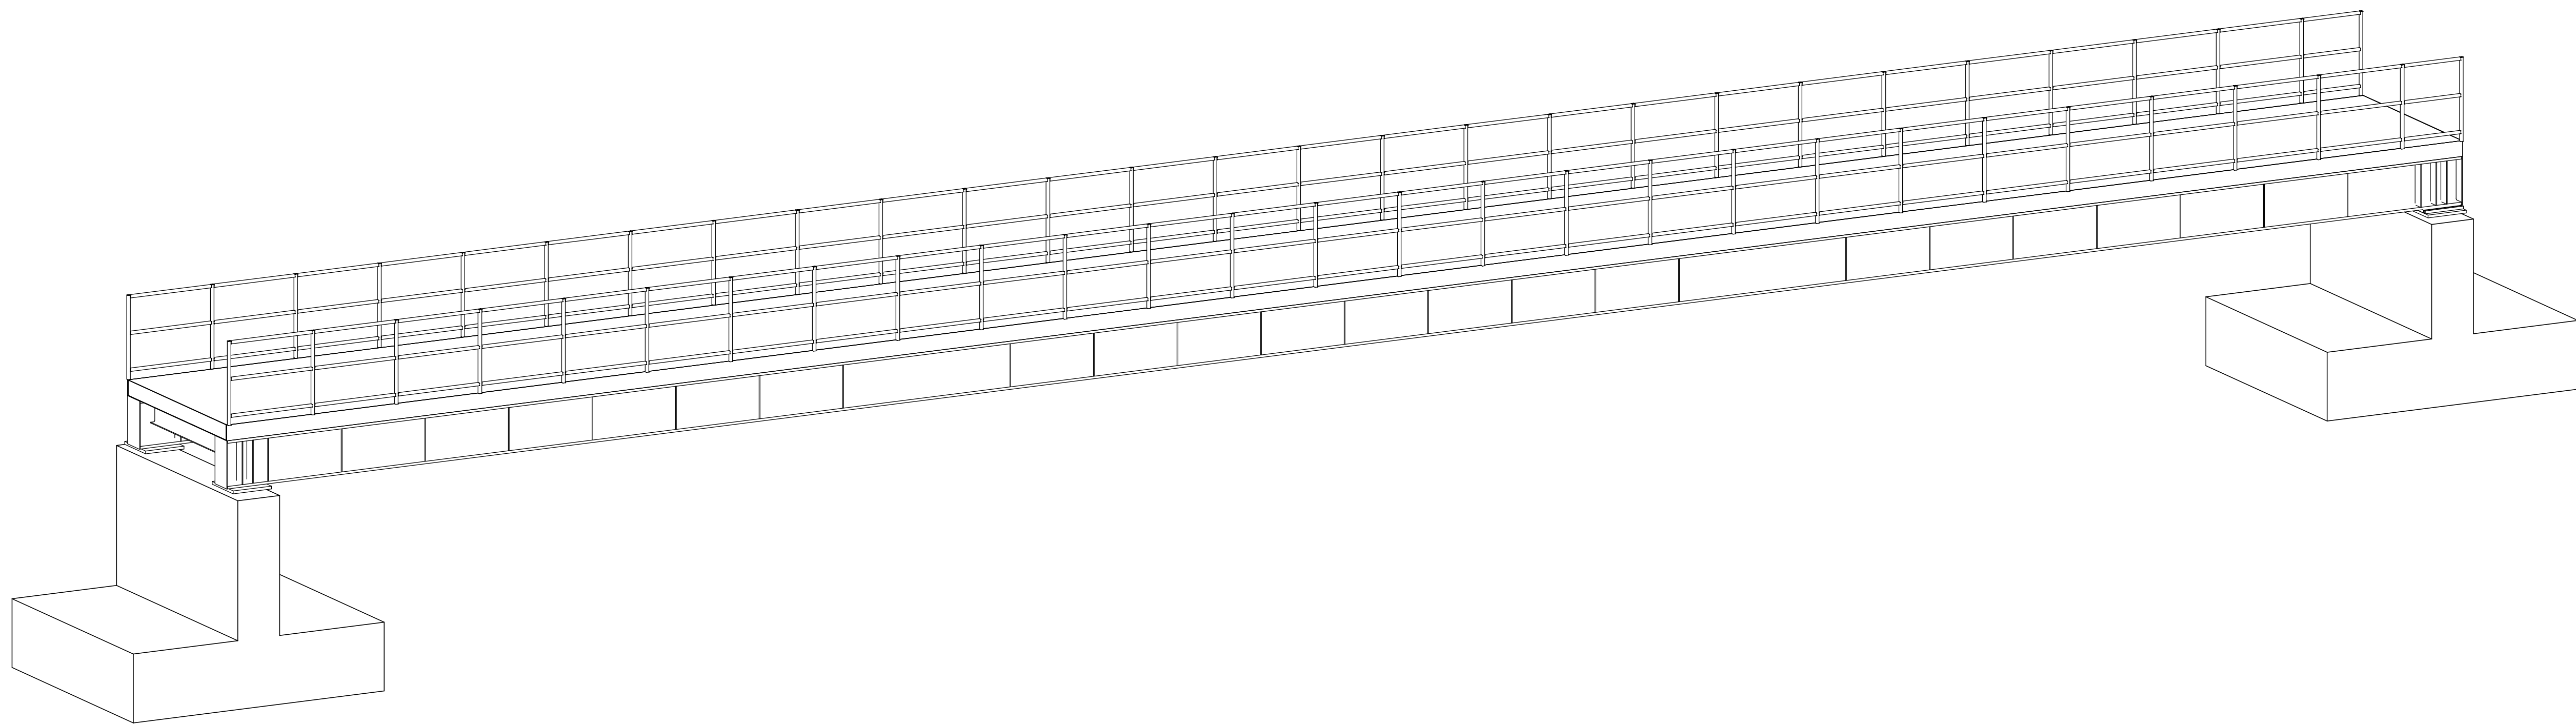

4 Axonometric View
S302

RESERVED FOR AUTHORITY STAMP

ISSUED FOR RECORD 2026-02-11
DATE

Client:



245 Markland Drive, Toronto, Ontario M6C 1R1
marklandwood.com | (416) 621-1200

Structural Consultants:



891 Yonge Street, Suite 300, Toronto, Ontario Canada M4W 3P4
T: 416.961.8256 | F: 416.961.7434
e: qdrew@quinndressel.com | www.quinndressel.com

CONTRACTOR SHALL CHECK ALL DIMENSIONS ON THE WORK AND REPORT ANY DISCREPANCY TO THE CONSULTANT BEFORE PROCEEDING. THIS DRAWING IS NOT TO BE USED FOR CONSTRUCTION UNTIL AUTHORIZED IN WRITING BY CONSULTANT.

#	DATE	REVISION
3	2026-02-11	ISSUED FOR RECORD
2	2026-02-08	ISSUED FOR UPDATE
1	2026-02-24	ISSUED FOR CLIENT'S REVIEW

NOT FOR
CONSTRUCTION

MARKLAND WOOD GOLF CLUB-ELEVATED PATHWAY

PROJECT ADDRESS:
245 MARKLAND DRIVE, TORONTO, ONTARIO M6C 1R1
PROJECT CLIENT:
MARKLAND WOOD GOLF CLUB

SCALE: As Indicated
DRAWN BY: JC
REVIEWED BY: RT
PROJECT NUMBER: 24-172
PLOT DATE: 2026-02-11 3:07:59 PM

PROPOSED ELEVATED PATHWAY

DRAWING NUMBER

S302