




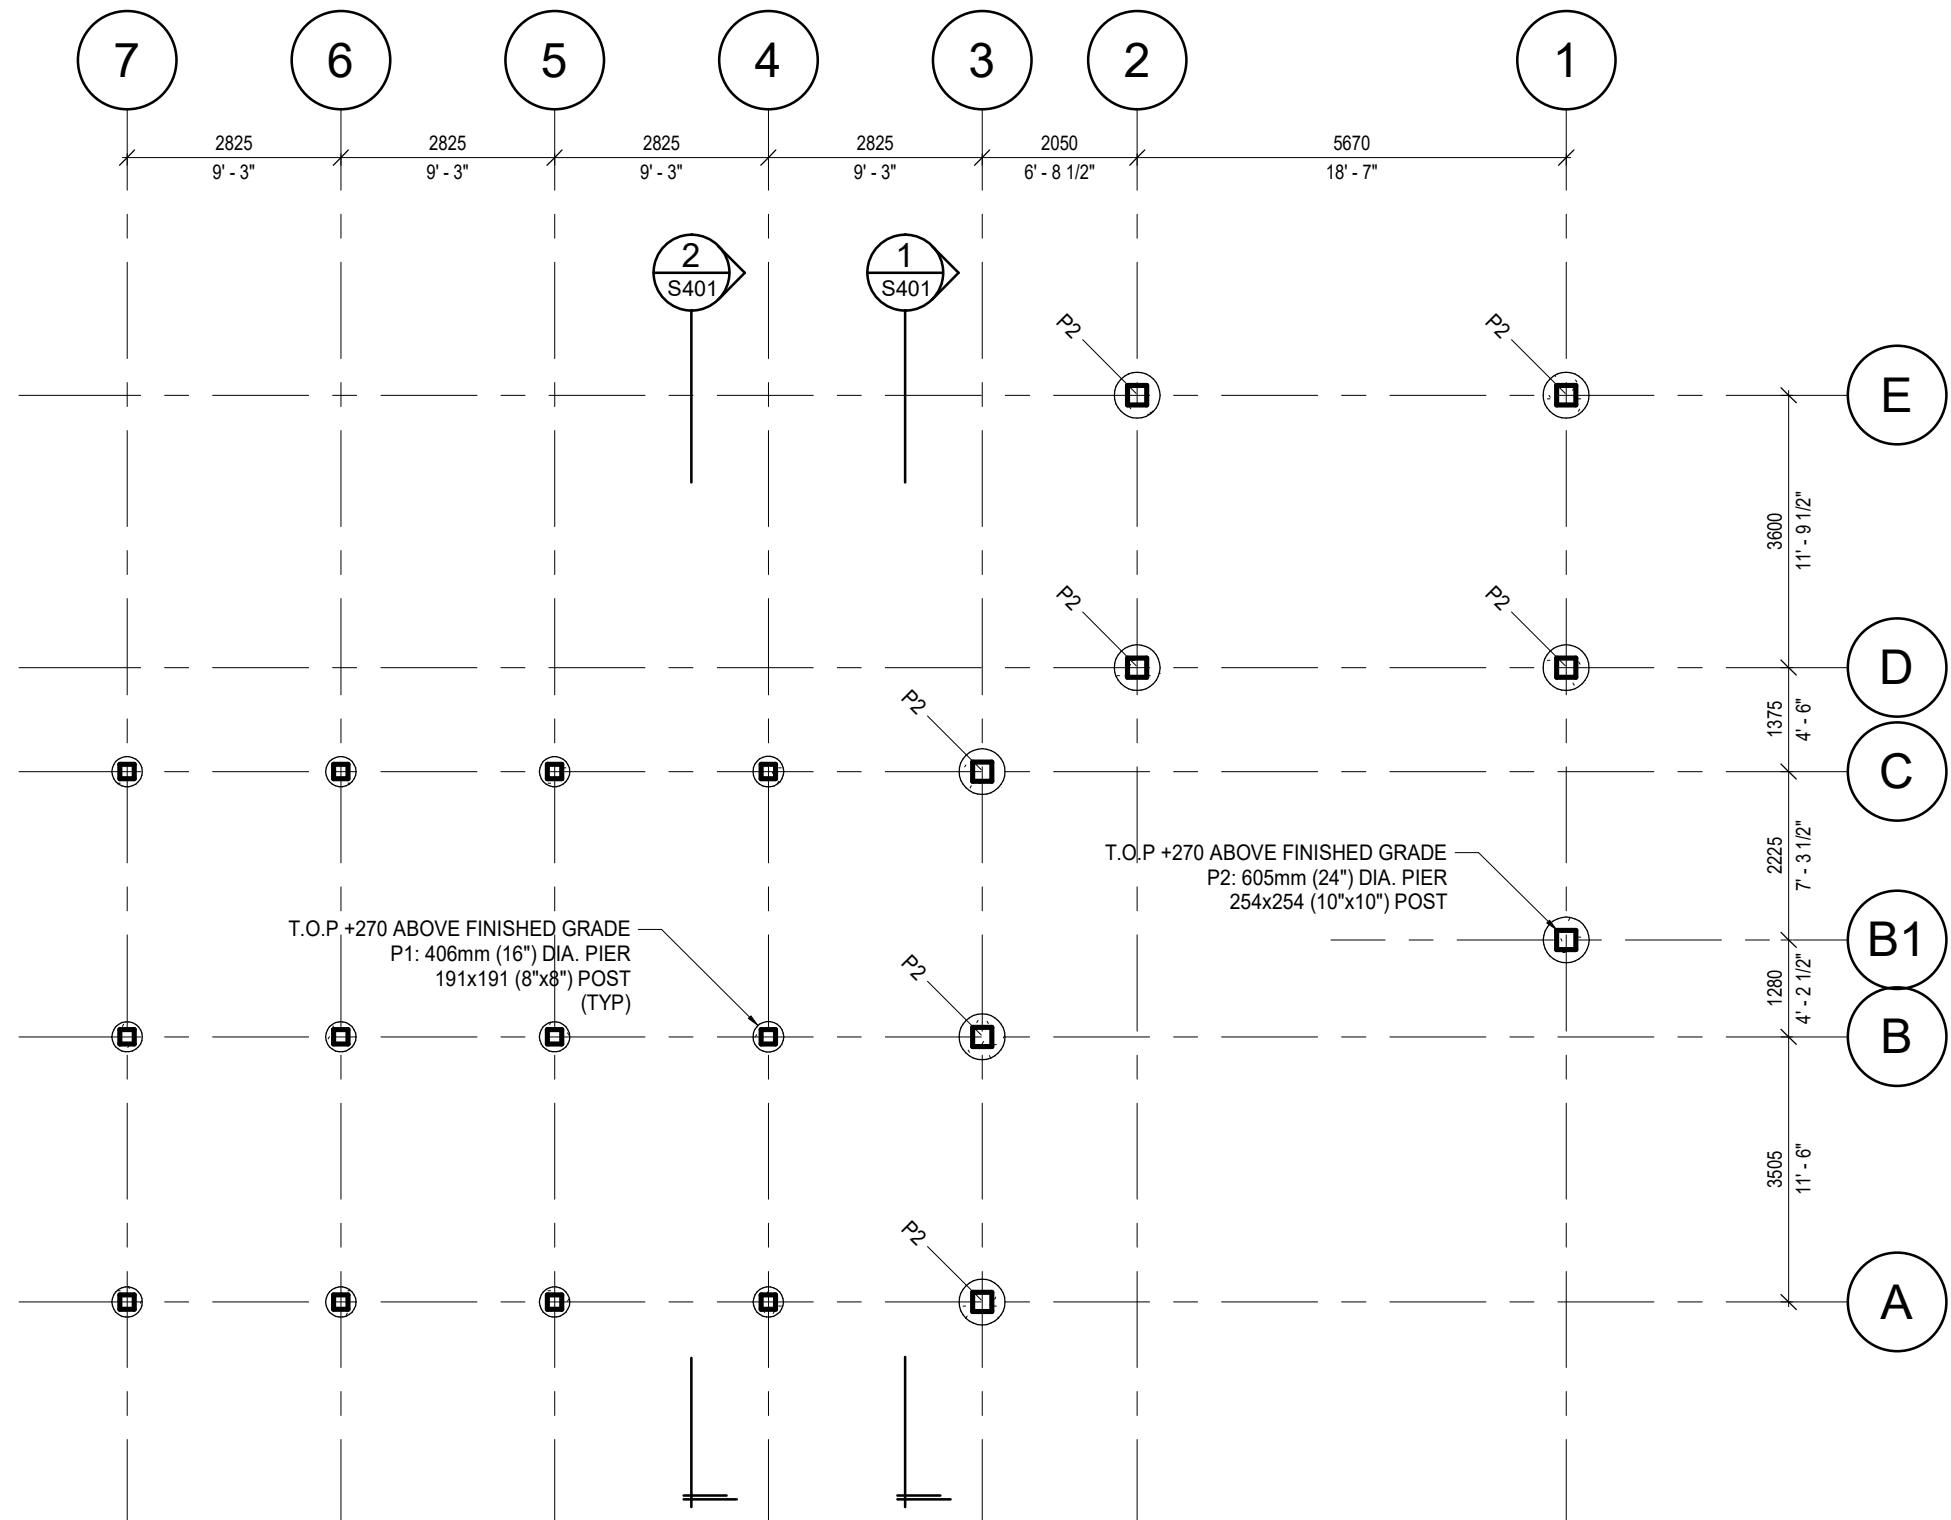


1 GROUND FLOOR CANOPY 1  
S201 1 : 100

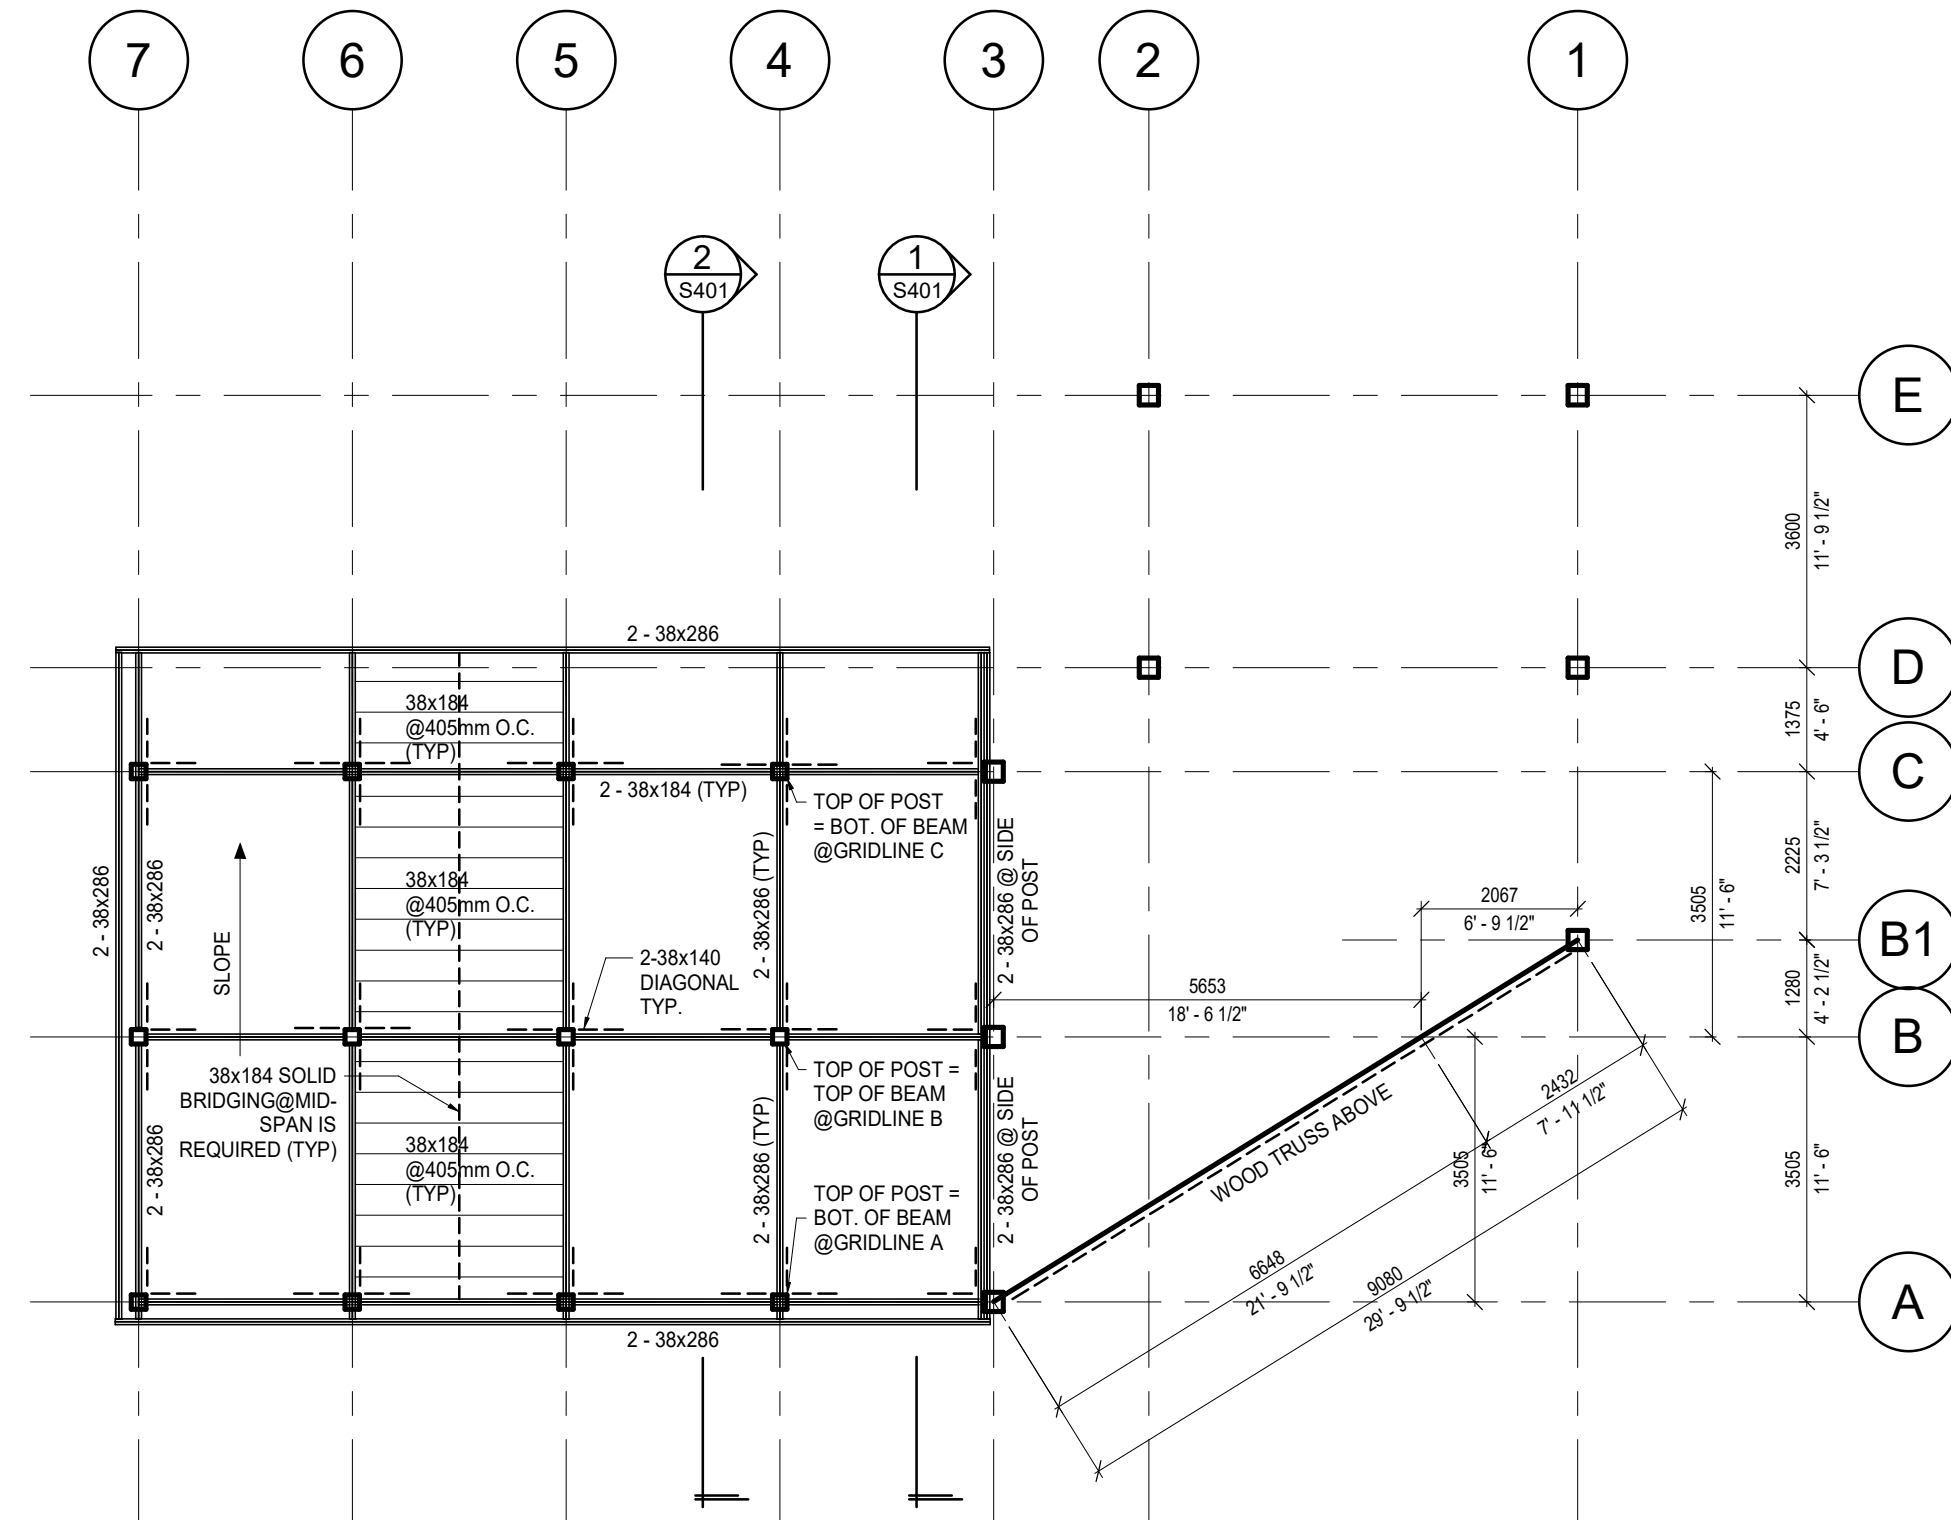


2 LOW ROOF CANOPY 1  
S201 1 : 100

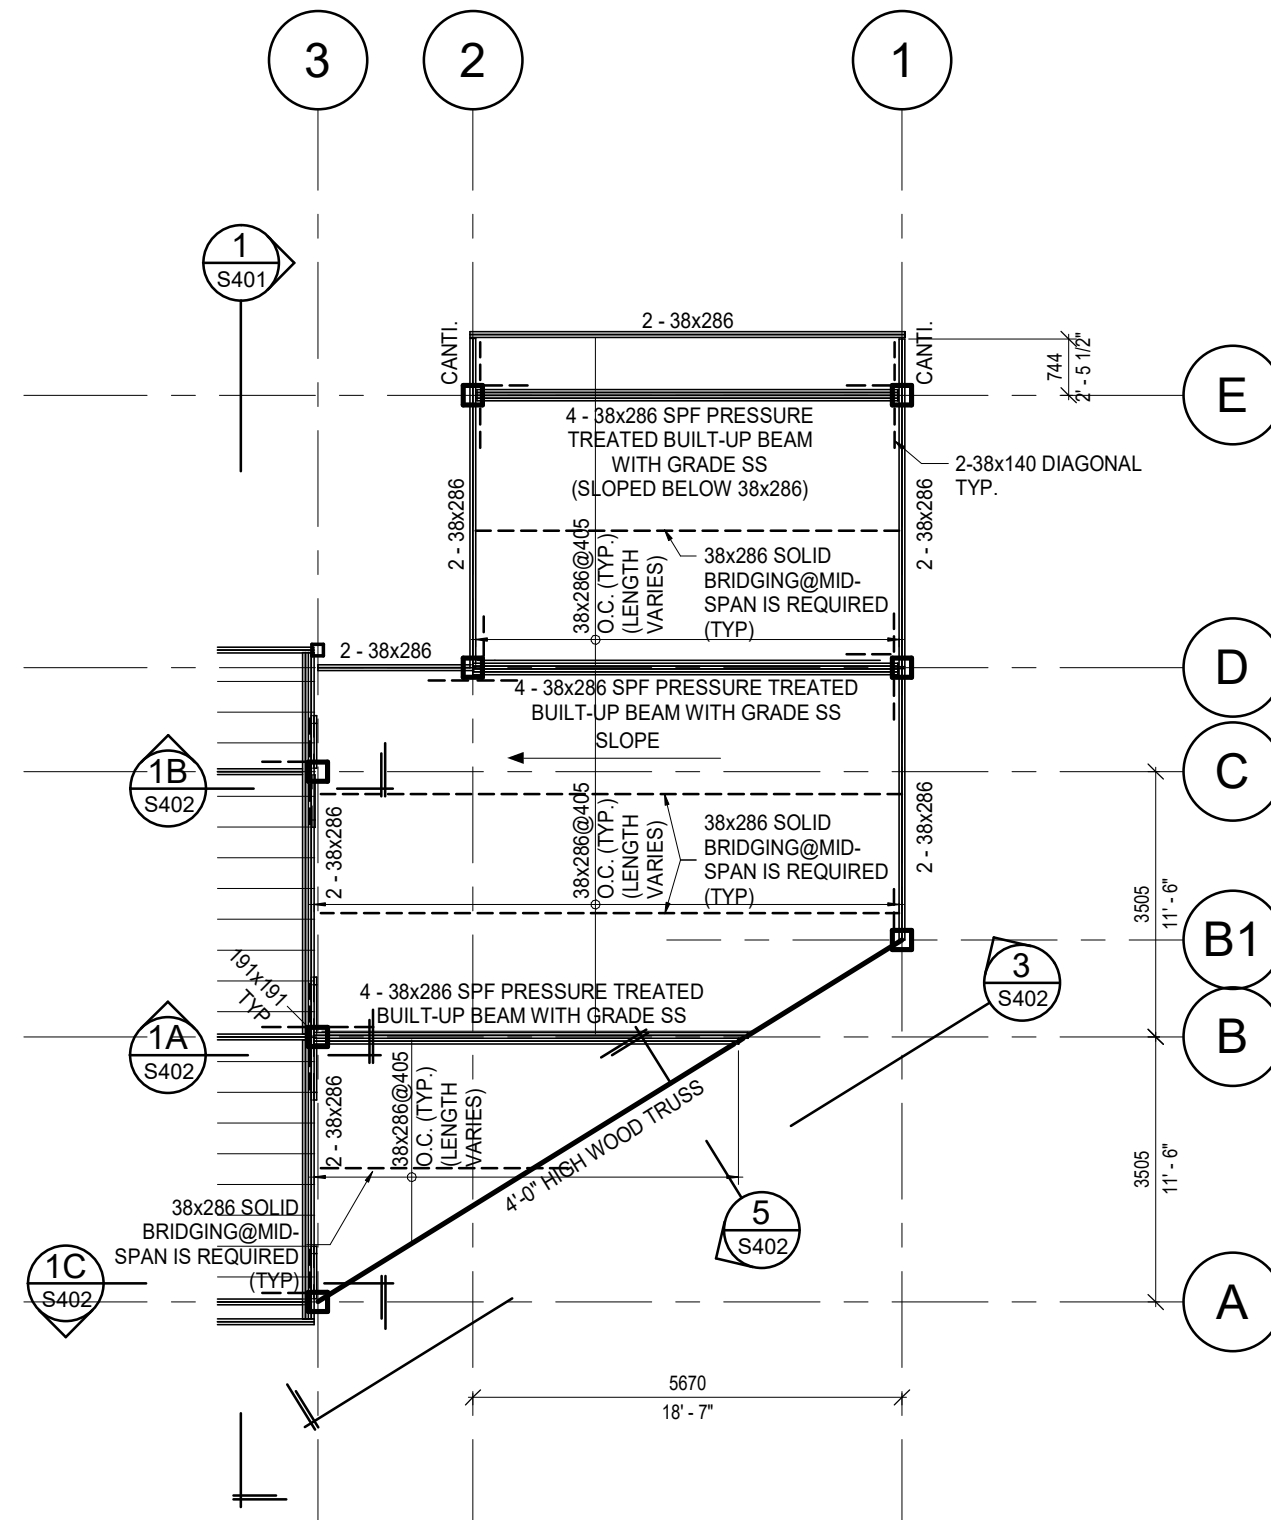

3 HIGH ROOF CANOPY 1  
S201 1 : 100

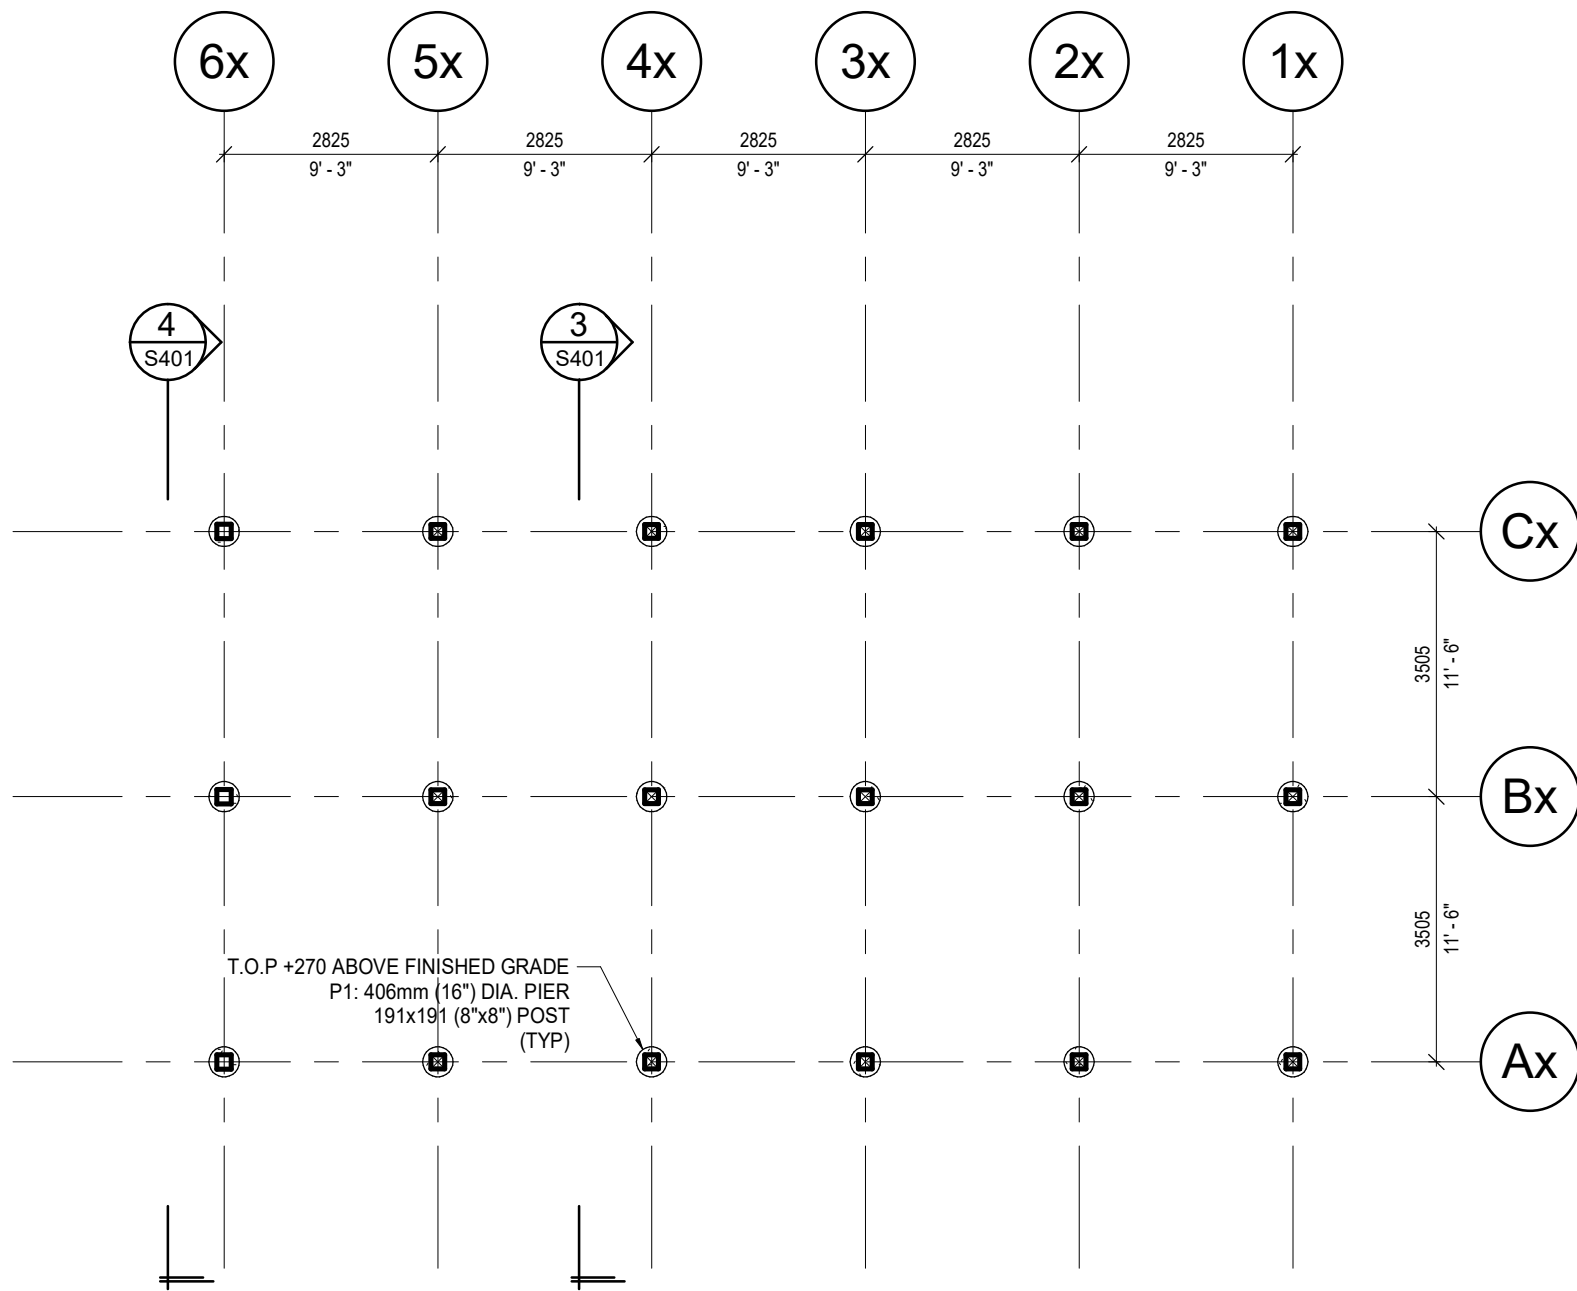

4 GROUND FLOOR CANOPY 2  
S201 1 : 100

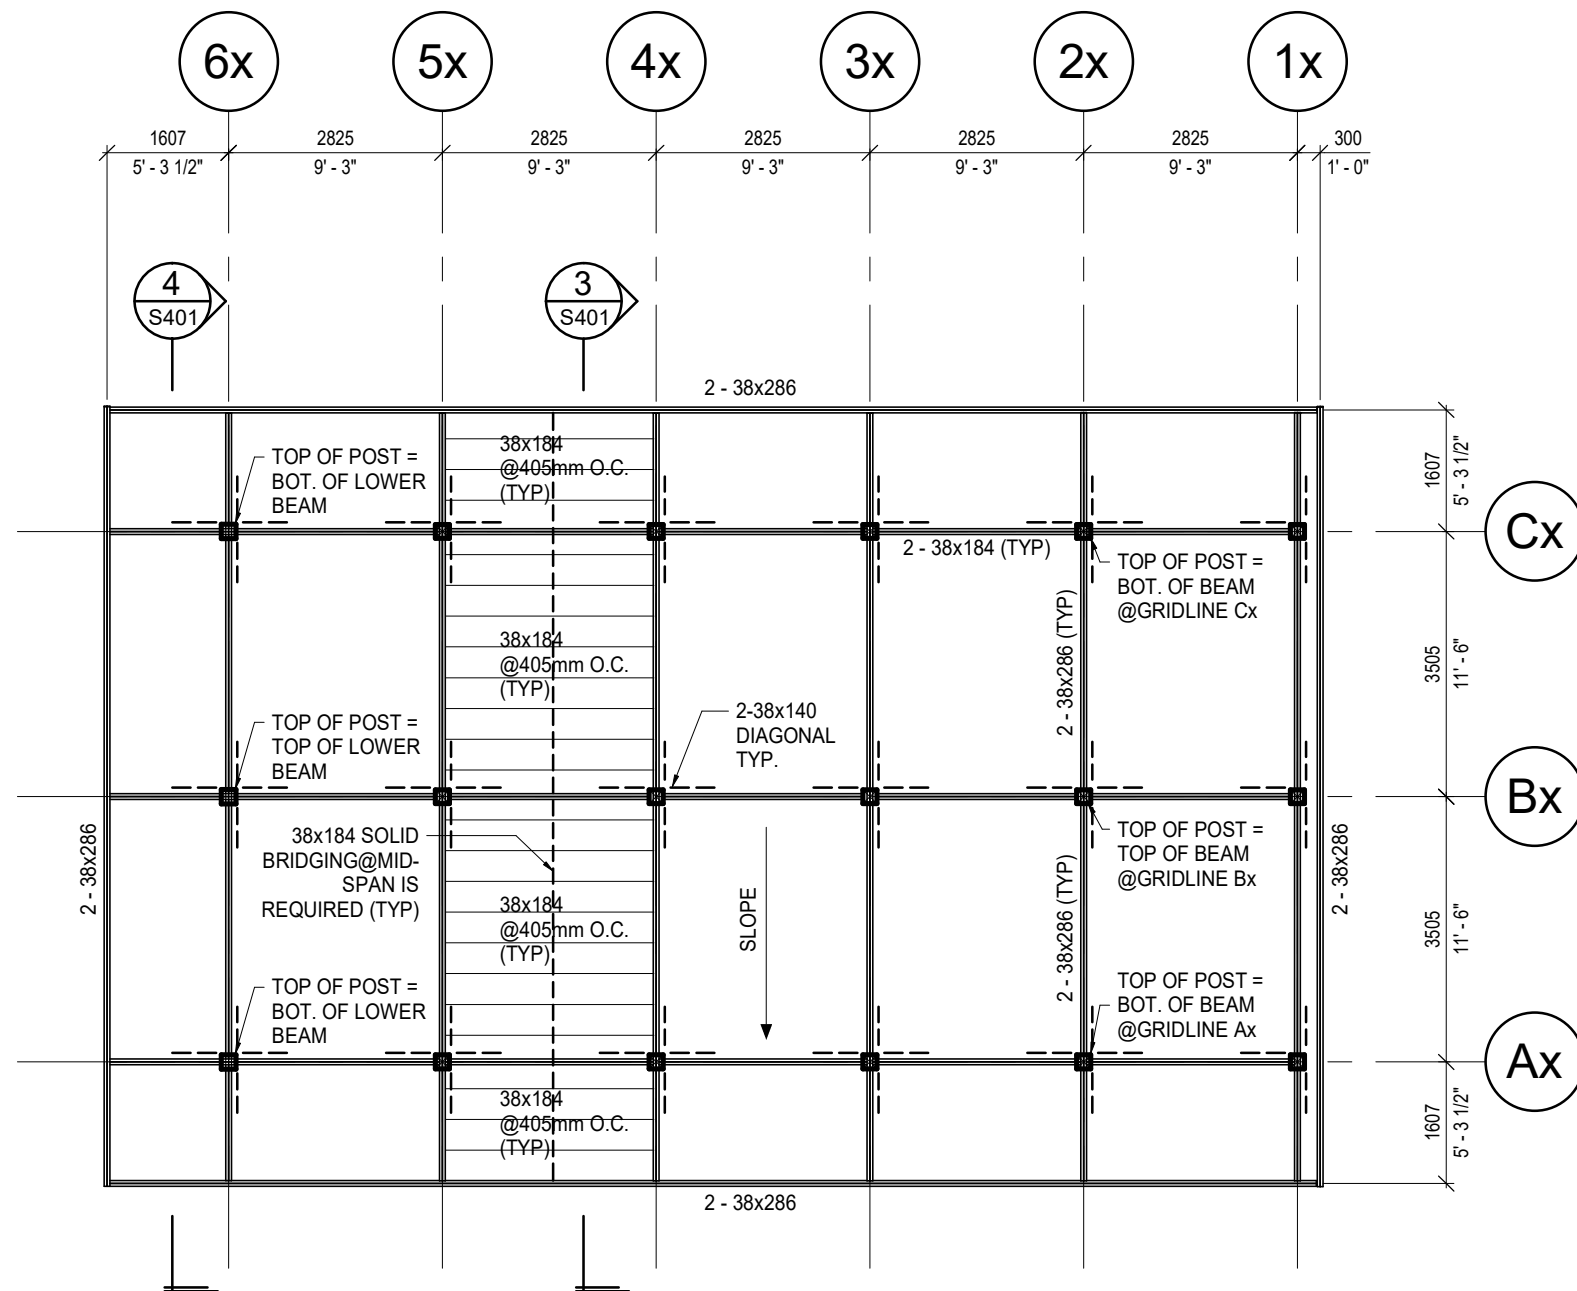

5 ROOF CANOPY 2  
S201 1 : 100

- TIMBER NOTES:
- TIMBER DESIGN SHALL COMPLY WITH CSA 086, CSA 0141 & 2012 ONTARIO BUILDING CODE AT LATEST VERSION.
  - ALL JOISTS, RAFTERS, SHORING, BRACING, BLOCKING, STUDS OR STUD WALL SHALL BE NO 1 OR NO 2 SPF (SPRUCE-PINE-FIR) OR BETTER UNLESS NOTES OTHERWISE. ALL MATERIALS SHALL CONFORM TO CAN2-086 AND CSA 0141, INCLUDING ALL APPENDICES, AND SHALL BE SUPPLIED AS DRY LUMBER (MOISTURE CONTENT 19% MAX). GRADING SHALL CONFORM TO THE RULE OF THE NATIONAL LUMBER GRADES AUTHORITY (NLGA).
  - ROOF PLYWOOD 3/4" TYPICAL AND SHALL CONFORM TO CSA 0121-17 (R2022).
  - CONNECTIONS FOR STUDS, RAFTERS AND JOISTS SHALL COMPLY WITH REQUIREMENTS IN PART 9 OBC, AND TABLE 9.2.3.4, UNLESS NOTED OTHERWISE.
  - ALL FLUSH JOISTS SHALL BE SUPPORTED WITH STEEL JOIST HANGERS MANUFACTURED BY SIMPSON STRONG TIE OR APPROVED EQUAL TO RESIST THE UPLIFT LOAD. ALL CONNECTIONS MUST CONNECT WITH SIMPSON STRONG HURRICANE TIES. CONTRACTORS MUST SUBMIT SHOP DRAWINGS (WITH P. ENG. STAMP) SPECIFYING THE CONNECTOR TYPE AT ALL CONNECTIONS.
  - COLUMNS SHALL BE SECURELY FASTENED TO THE BEAM TO PREVENT LATERAL MOVEMENT.
  - PROVIDE SOLID BLOCKING THE FULL WIDTH OF THE SUPPORTED MEMBER UNDER ALL CONCENTRATED LOADS.
  - NO HOLES ARE TO BE CUT OR DRILLED IN JOISTS EXCEPT AS PERMITTED IN THE BUILDING CODE, OR BY THE WOOD MANUFACTURER. LATEST APPROVED DRAWINGS SUPERSEDES ALL PREVIOUSLY SUBMITTED AND STAMPED DRAWINGS.
  - NO CHORRS IN WOOD TRUSS OR ANY PART OF WEB WITHIN 2" OF THE TOP OR BOTTOM MAY BE CUT OR DRILLED.
  - ALL EXTERIOR/EXPOSED WOOD SHALL BE PRESSURE TREATED PINE. ALL EXTERIOR/EXPOSED FASTENER INCLUDING BOLTS, NAILS, SCREWS, WASHERS, PLATES SHALL BE GALVANIZED.
  - ALL TEMPORARY BRACING SHALL BE SUPPLIED AS NECESSARY TO FACILITATE STABLE INSTALLATION.

- FOUNDATION NOTES:
- TOP OF CONCRETE PIERS IS 270mm ABOVE FINISHED GRADE (SEE ARCHITECTURAL FOR FINISHED GRADE ELEVATIONS) (UNLESS NOTED OTHERWISE).
  - BOTTOM OF PIER MINIMUM IS 1200mm BELOW GRADE, THE PIER IS VARIED IN LENGTH. PIER REINFORCING: 6-10# w/100 TOP END HOOK w/100@300 TIES.
  - CONCRETE f'c=35 MPa TYPE C-2.
  - FOR SHOP DRAWINGS, IT IS UNDERSTOOD AND ACKNOWLEDGED BY ALL THAT THE CO-ORDINATION AND PREPARATION OF THE SHOP DRAWINGS IS THE RESPONSIBILITY OF THE GENERAL CONTRACTOR, CONSTRUCTION MANAGER OR PROJECT MANAGER. QUINN DRESSSEL ASSOCIATES WILL RECEIVE AND REVIEW SHOP DRAWINGS PREPARED BY THE STRUCTURAL TRADES. SUCH REVIEW, IS FOR THE SOLE PURPOSE OF ASCERTAINING CONFORMANCE WITH THE GENERAL DESIGN CONCEPT CRITERIA AND INTENT WHERE DIRECTED BY THE CONTRACT DOCUMENTS. THE ABOVE SUBMISSION REQUIRE THE SEAL AND SIGNATURE OF A PROFESSIONAL ENGINEER, SO REGISTERED IN THE GOVERNING JURISDICTION. IN SUCH INSTANCES, THE SOLE RESPONSIBILITY FOR THE DESIGN OF SUCH ELEMENTS LIES WITH THAT DESIGNER AND IS OUTSIDE OF THE SCOPE OF SERVICES PROVIDED BY QUINN DRESSSEL ASSOCIATES.

- CANOPY ROOF NOTES:
- LOADING  
SUPERIMPOSED DEAD LOAD: 0.5 kPa (10.4 PSF)  
SNOW LOAD (Ss=1.3, Sr=0.4, Is=0.8 (ULS)) / 0.9 (SL): 1.15 kPa (24 PSF)  
SEE ROOF PLAN FOR SNOW ACCUMULATION.  
WIND UPLIFT (W=0.8 (ULS)) / 0.75 (SL): 1.68 kPa (TRIBUTARY AREA ≤ 1m²)  
0.96 kPa (TRIBUTARY AREA = 10m²)
  - SHEATHING-TO-FRAMING CONNECTION ON THE ROOF:  
METAL-TO-WOOD SCREW SPACED@MAX. 300mm O.C. ALONG ROOF JOISTS;  
METAL-TO-WOOD SCREW SPACED@MAX. 150mm O.C. ALONG BUILT-UP BEAM & POST BETWEEN POSTS.

PROJECT  
MOHAWK PARK - STORAGE  
CANOPY

P.O. Box 160, 9430 Guelph Line  
Campbellville, Ontario, L0P 1B0

CLIENT




WOODBINE ENTERTAINMENT GROUP  
MOHAWK PARK  
P.O. Box 160, 9430 Guelph Line  
Campbellville, Ontario, L0P 1B0

ARCHITECT



143 Steeles Ave. Toronto, ON M5H 4B2, Canada  
t 416.961.5157 #pa-architects@outlook.com


CONSULTANT

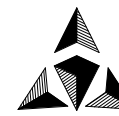

Quinn Dressel  
ASSOCIATES  
CONSULTING STRUCTURAL ENGINEERS  
880 Yonge St. Suite 305 Toronto, Ontario, Canada M4B 1P4  
t 416.961.5254 f 416.961.7434  
e qdressel@quindressel.com www.quindressel.com

THIS DRAWING IS NOT TO BE SCALED.  
REFER TO APPROPRIATE SURVEY, STRUCTURAL, MECHANICAL, ELECTRICAL, LANDSCAPE, ETC. CONSULTANT DRAWINGS BEFORE PROCEEDING WITH THE WORK.  
CONSTRUCTION MUST CONFORM TO ALL APPLICABLE CODES AND REQUIREMENTS OF AUTHORITIES HAVING JURISDICTION.  
THE CONTRACTOR WORKING FROM DRAWINGS NOT SPECIFICALLY MARKED "FOR CONSTRUCTION" MUST ASSUME FULL RESPONSIBILITY AND BEAR COSTS FOR ANY CORRECTIONS OR DAMAGES RESULTING FROM THEIR WORK.  
THIS DRAWING, AS AN INSTRUMENT OF SERVICE IS PROVIDED BY AND IS THE PROPERTY OF THE ARCHITECT.  
THE CONTRACTOR SHALL VERIFY AND ACCEPT RESPONSIBILITY FOR ALL DIMENSIONS AND CONDITIONS ON SITE AND SHALL NOTIFY THE APPROPRIATE CONSULTANT OF ANY VARIATIONS FROM THE SUPPLIED INFORMATION.


KEY PLAN

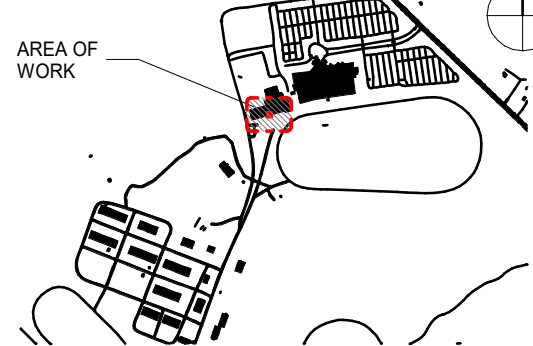

SEAL



NORTH ARROW

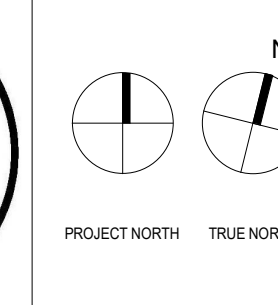

REVISIONS

| No. | Date | Description |
|-----|------|-------------|
|-----|------|-------------|

|   |            |                          |
|---|------------|--------------------------|
| 4 | 2025-04-30 | ISSUED FOR ADDENDUM S01  |
| 3 | 2025-04-28 | ISSUED FOR PERMIT TENDER |
| 2 | 2024-08-21 | ISSUED FOR TENDER ADD 02 |
| 1 | 2024-05-08 | ISSUED FOR COSTING       |

| No.     | Date | Description |
|---------|------|-------------|
| ISSUED: |      |             |

DRAWN BY: XS REVIEWED BY: RY

DATE: Issue Date SCALE: 1 : 100

PROJECT NO.: 24-055

SHEET TITLE

FRAMING PLANS CANOPY


SHEET NUMBER:

S201


REVISION NO.

4


24" x 36" Arch D - SHEET SIZE

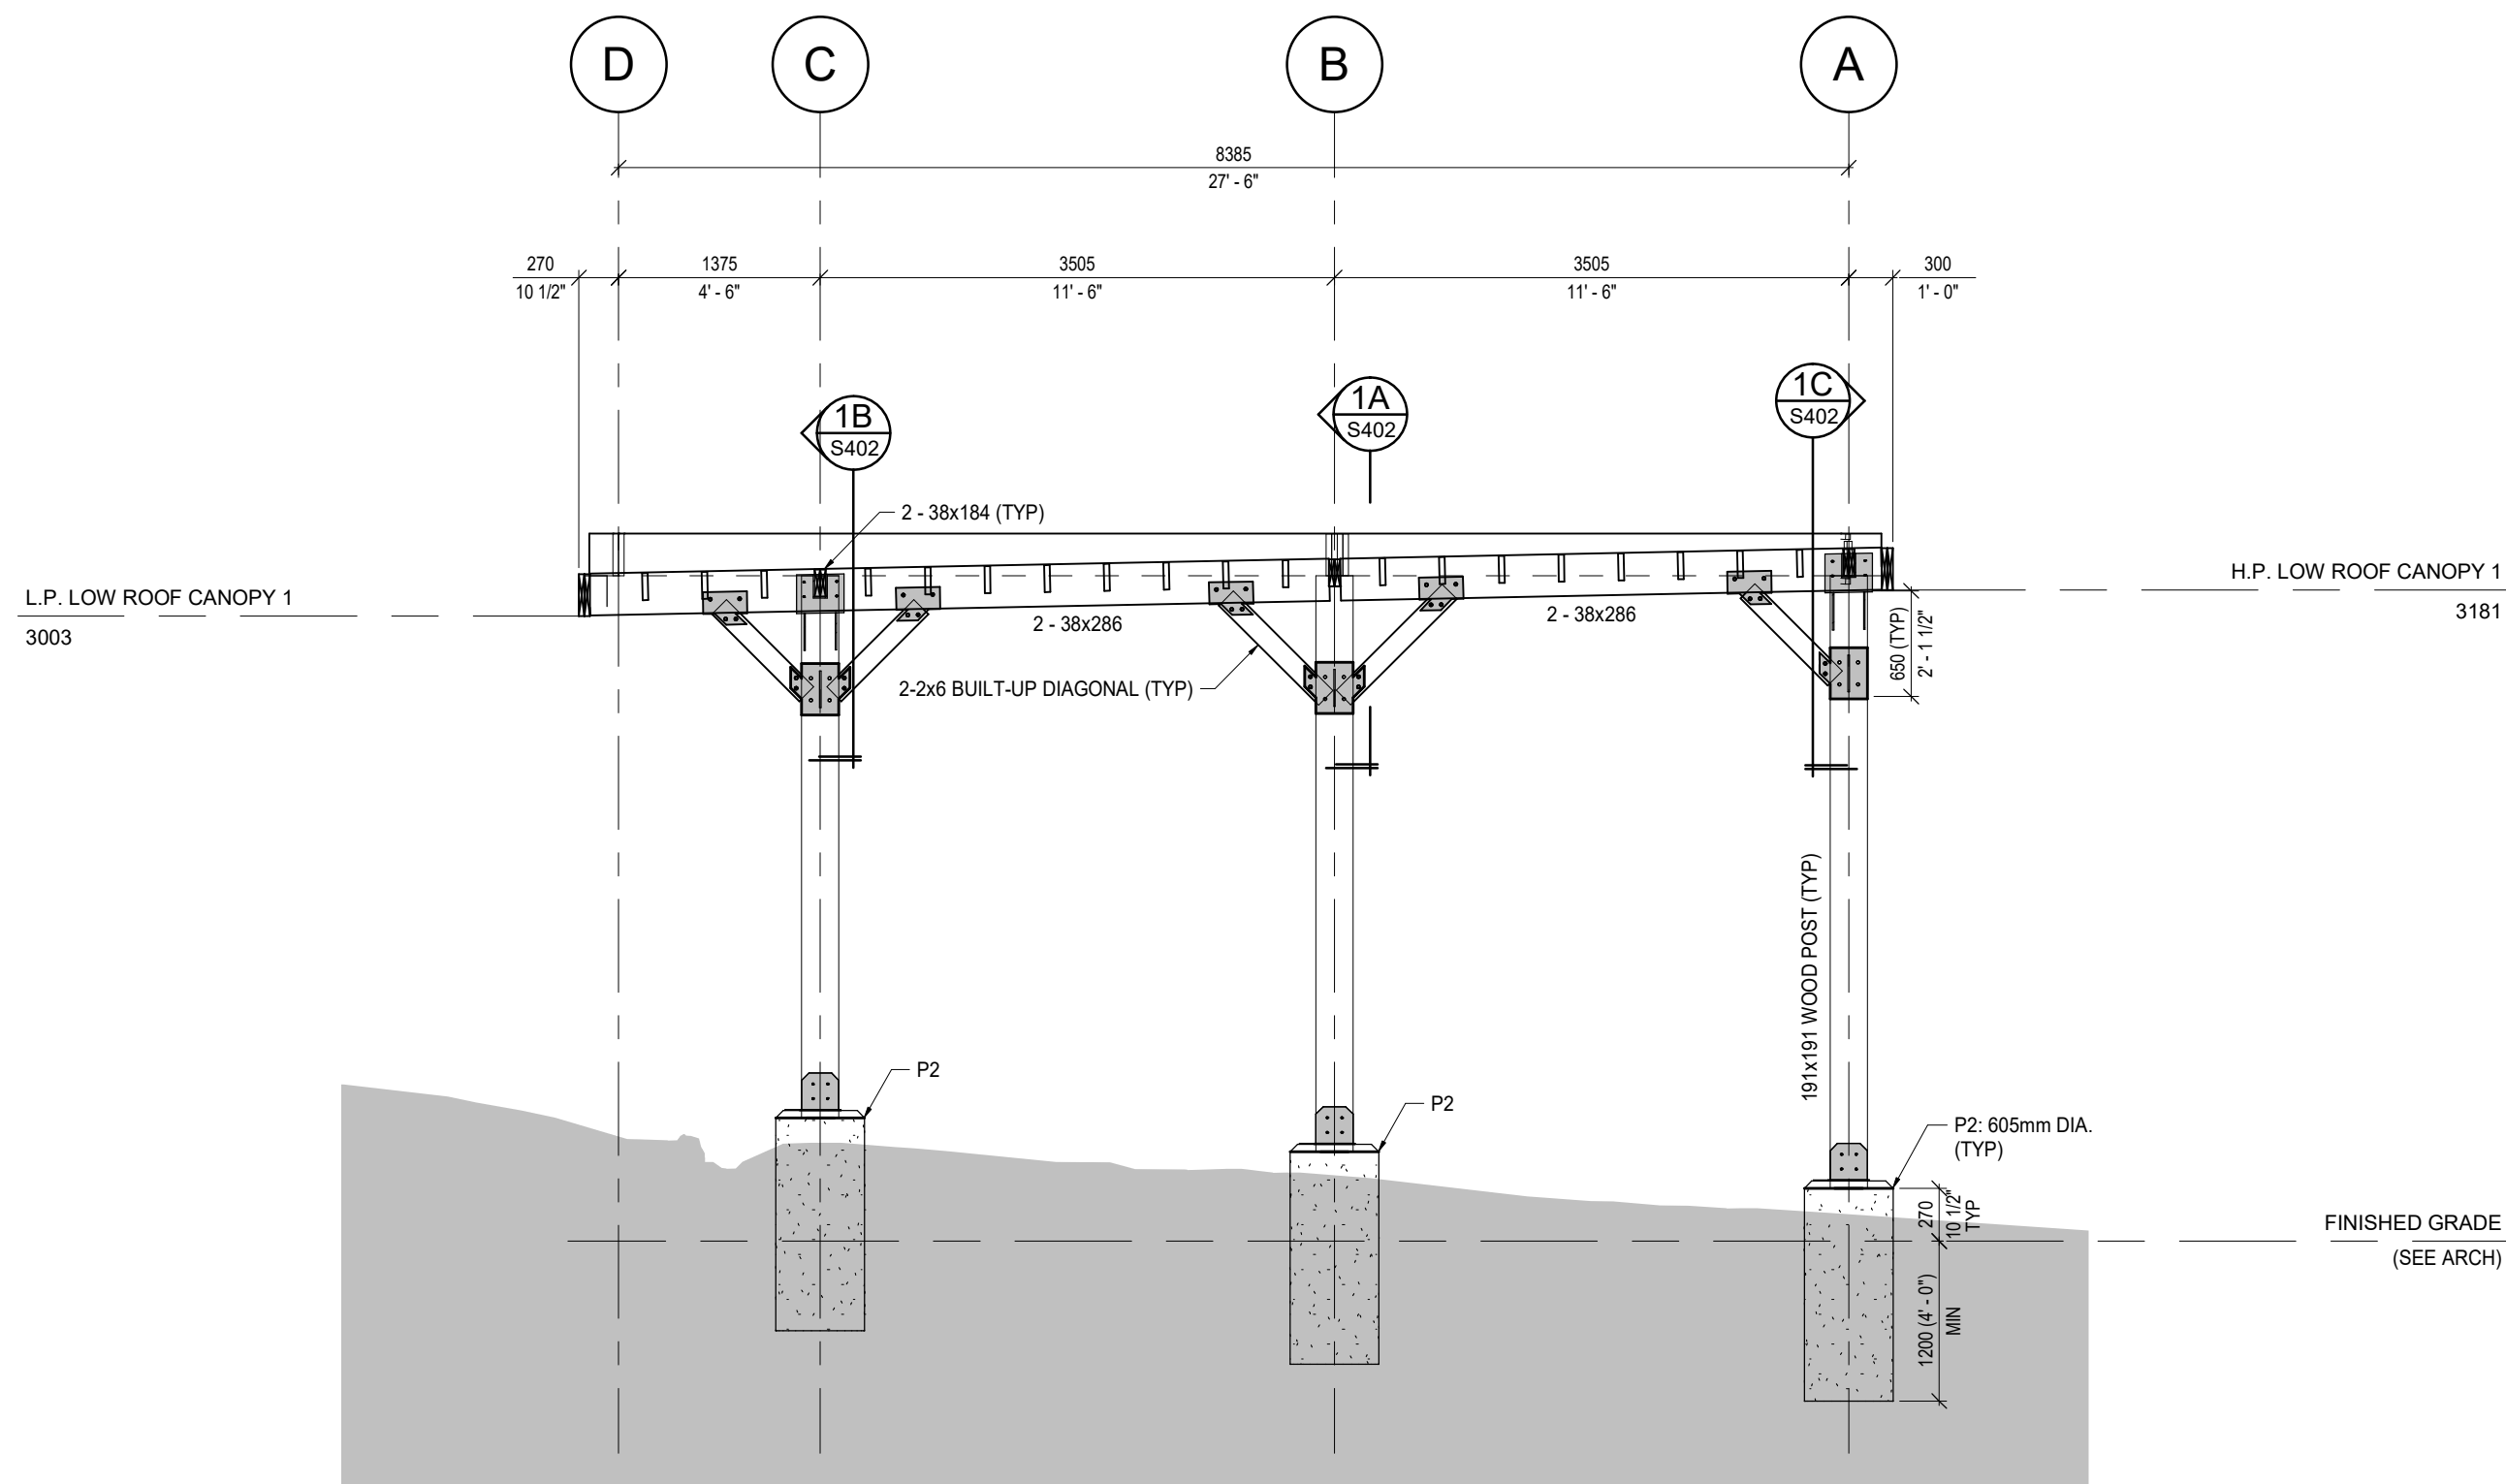


1 SECTION AT G/L 3  
S401 1 : 50

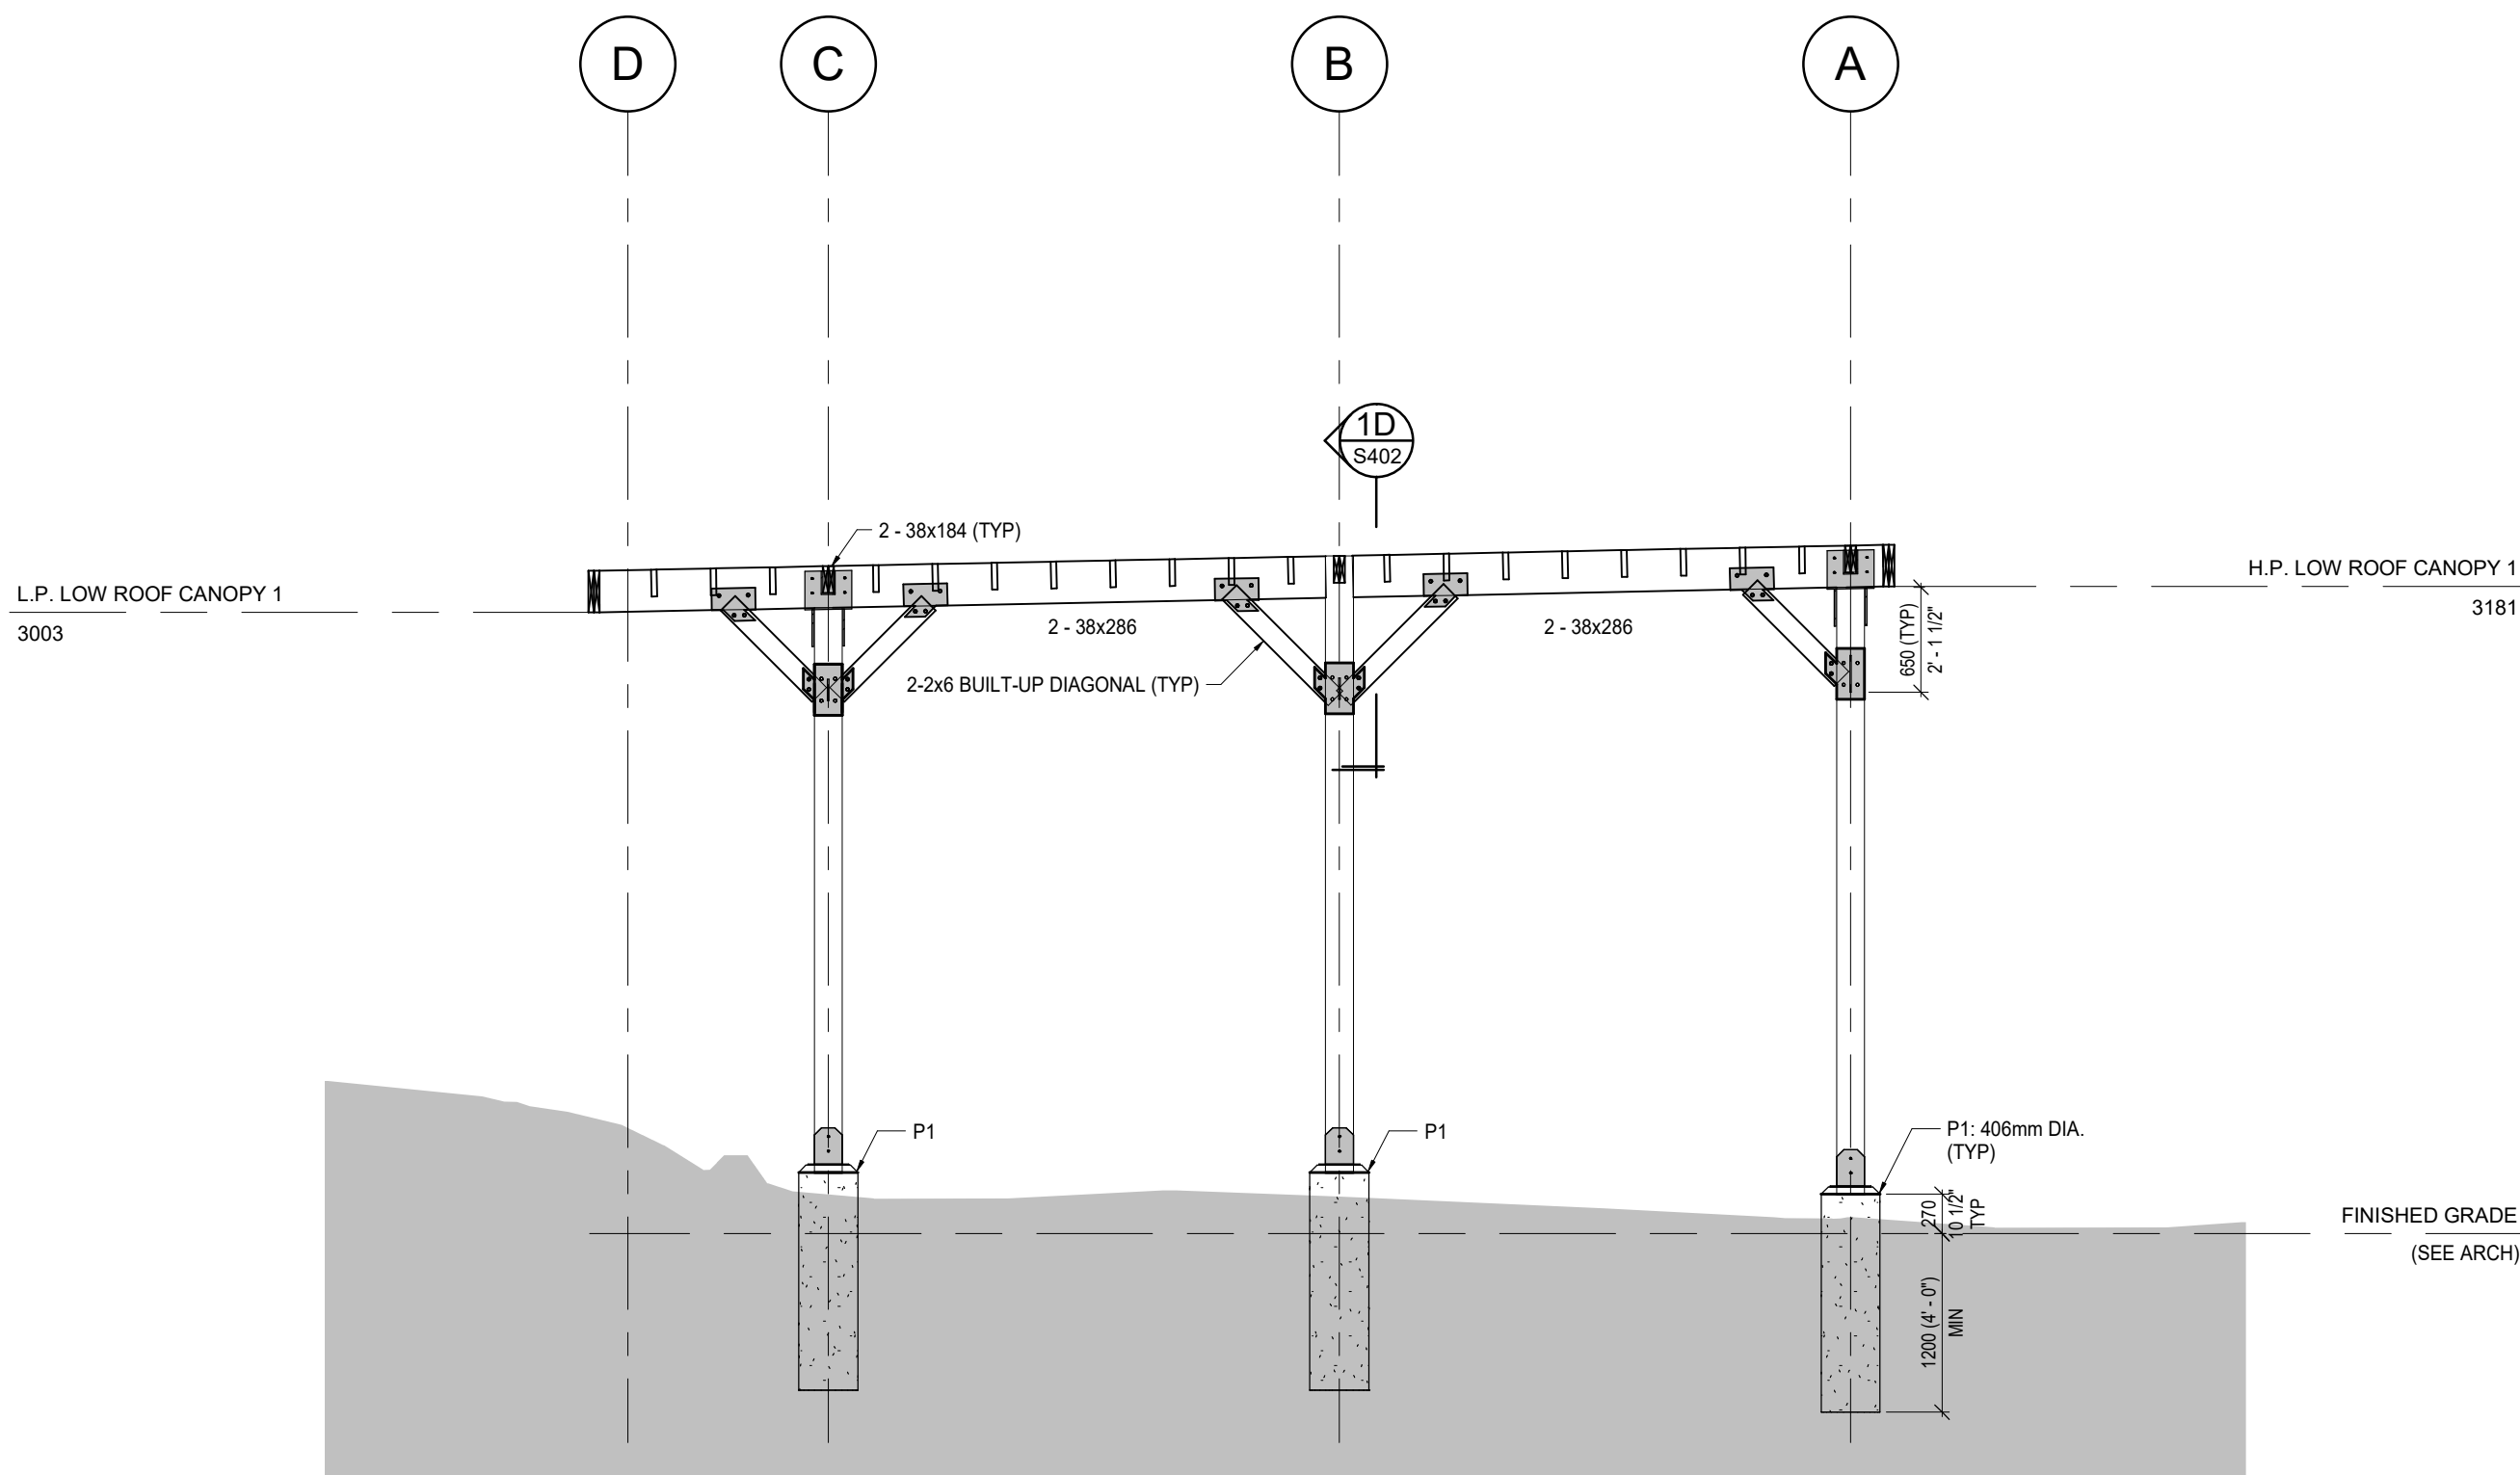

2 SECTION AT G/L 4  
S401 1 : 50

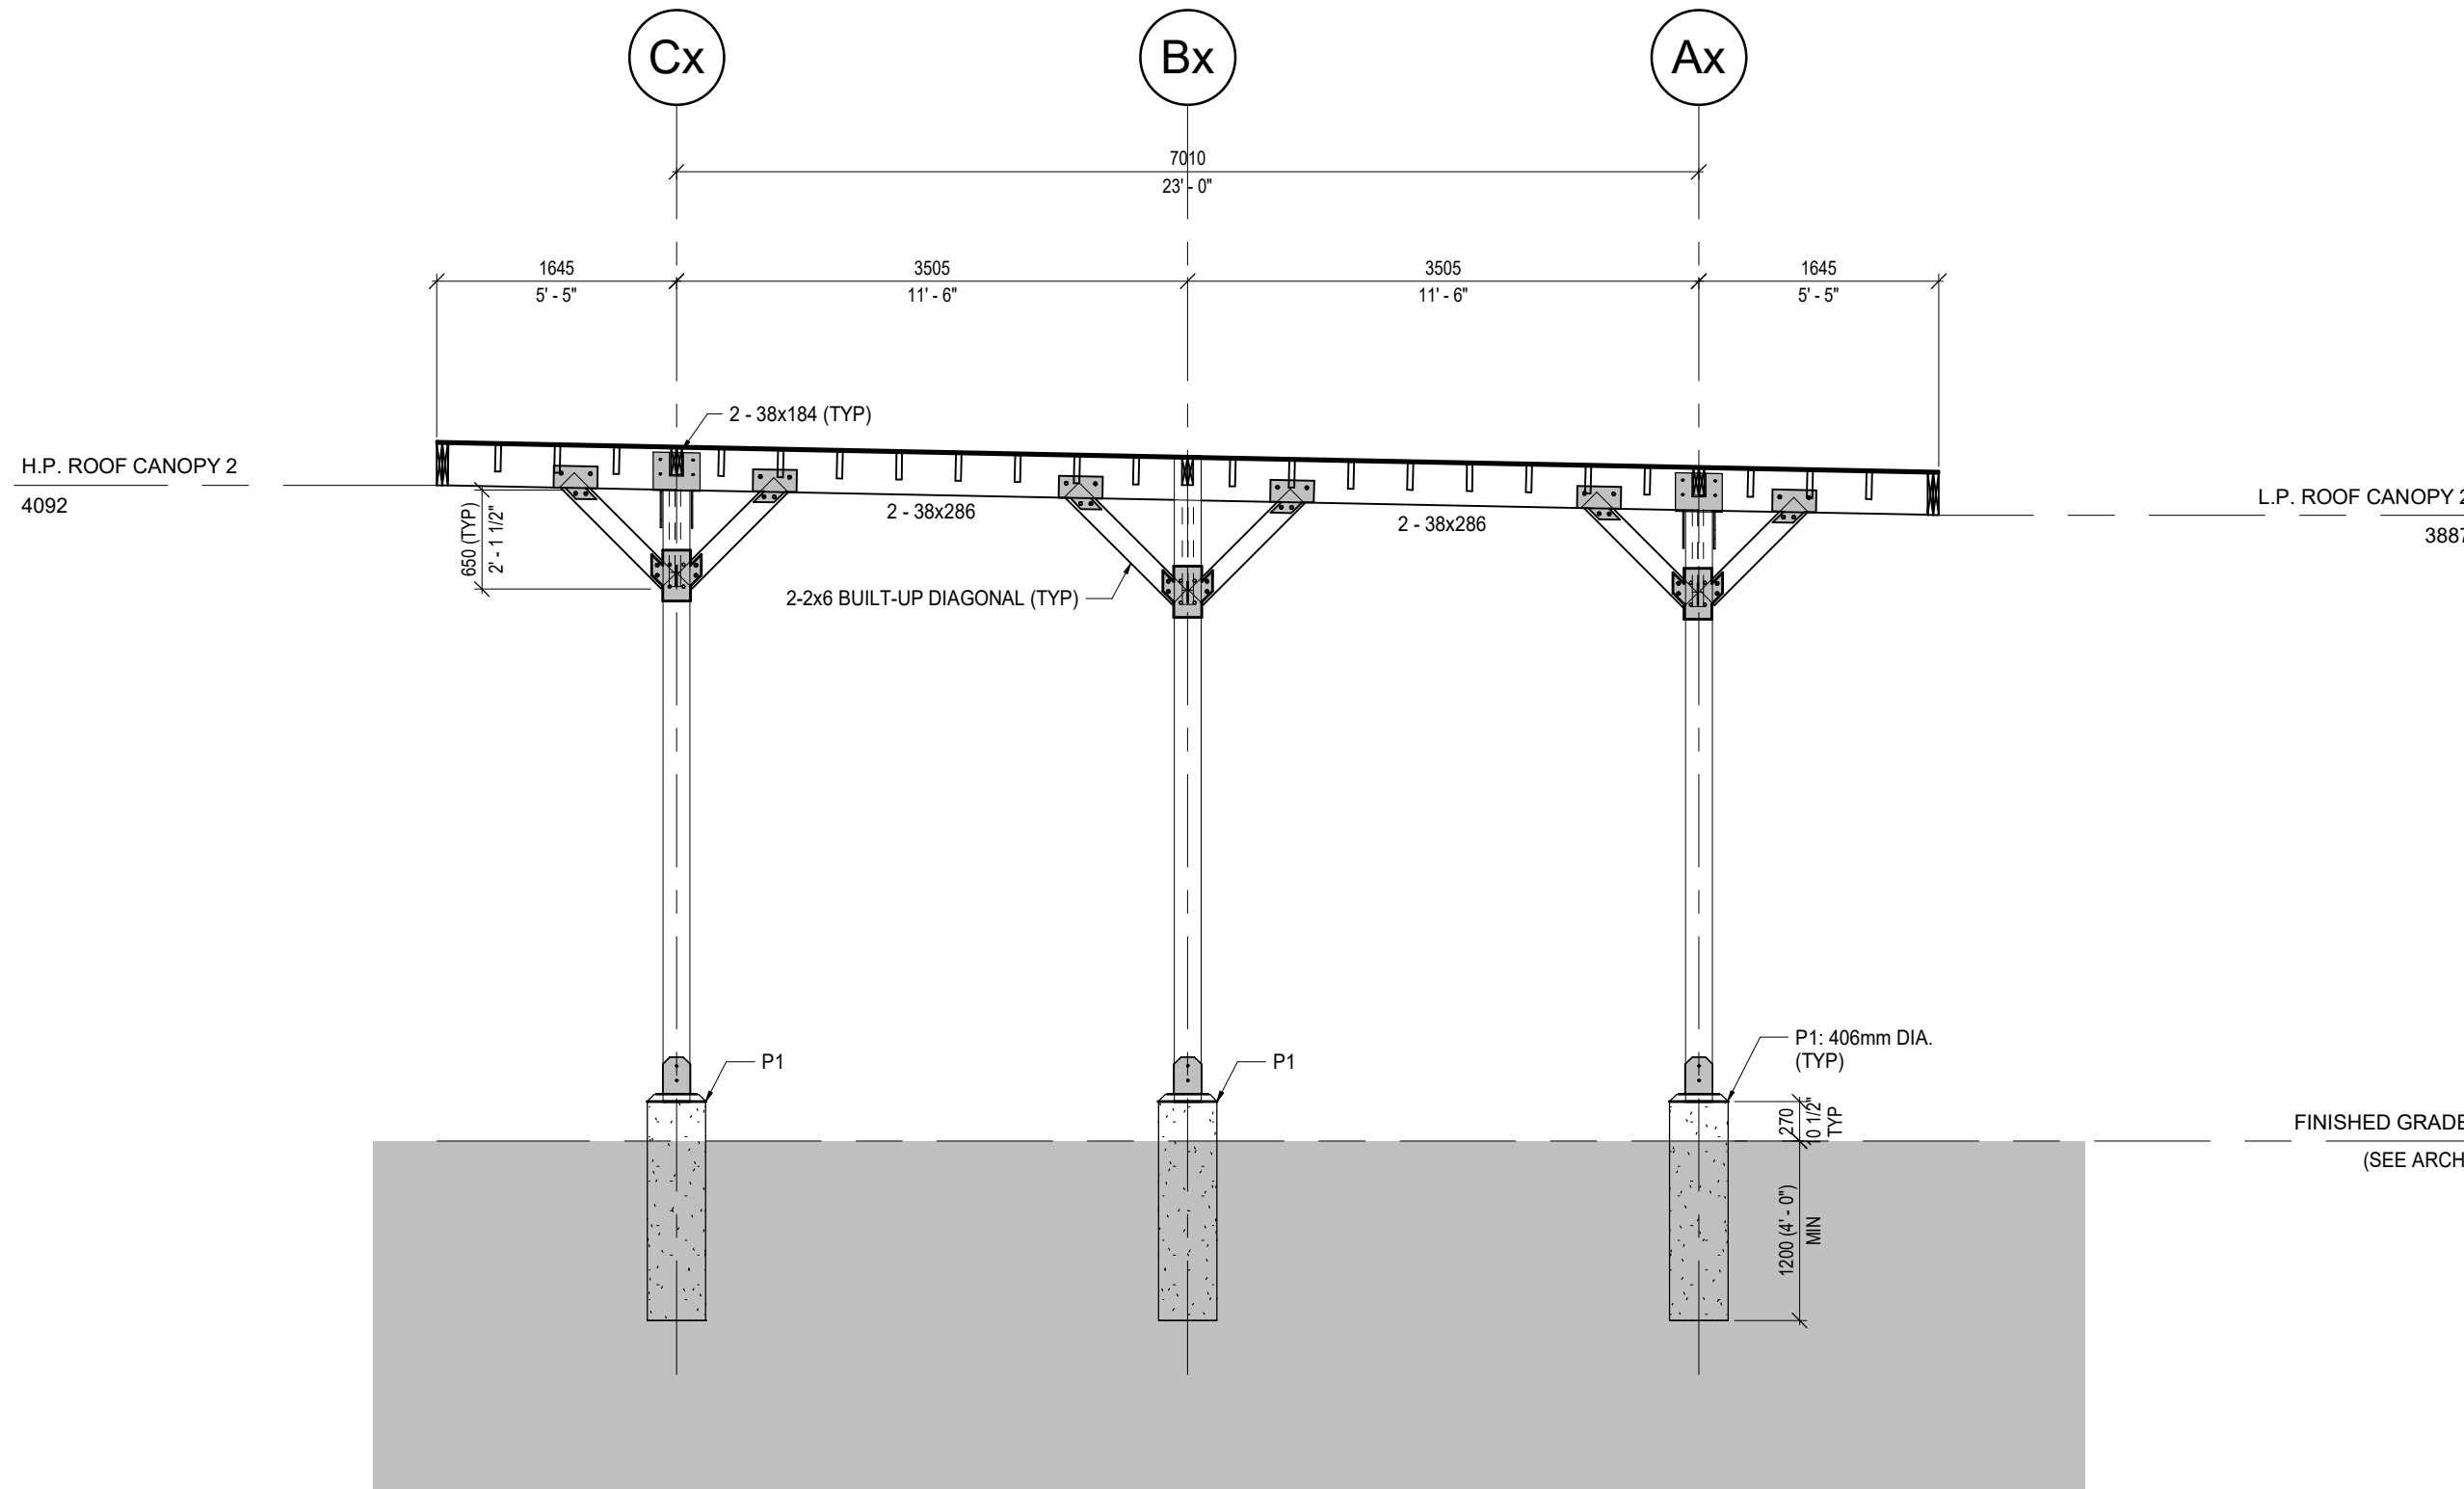

3 SECTION AT G/L 4x  
S401 1 : 50

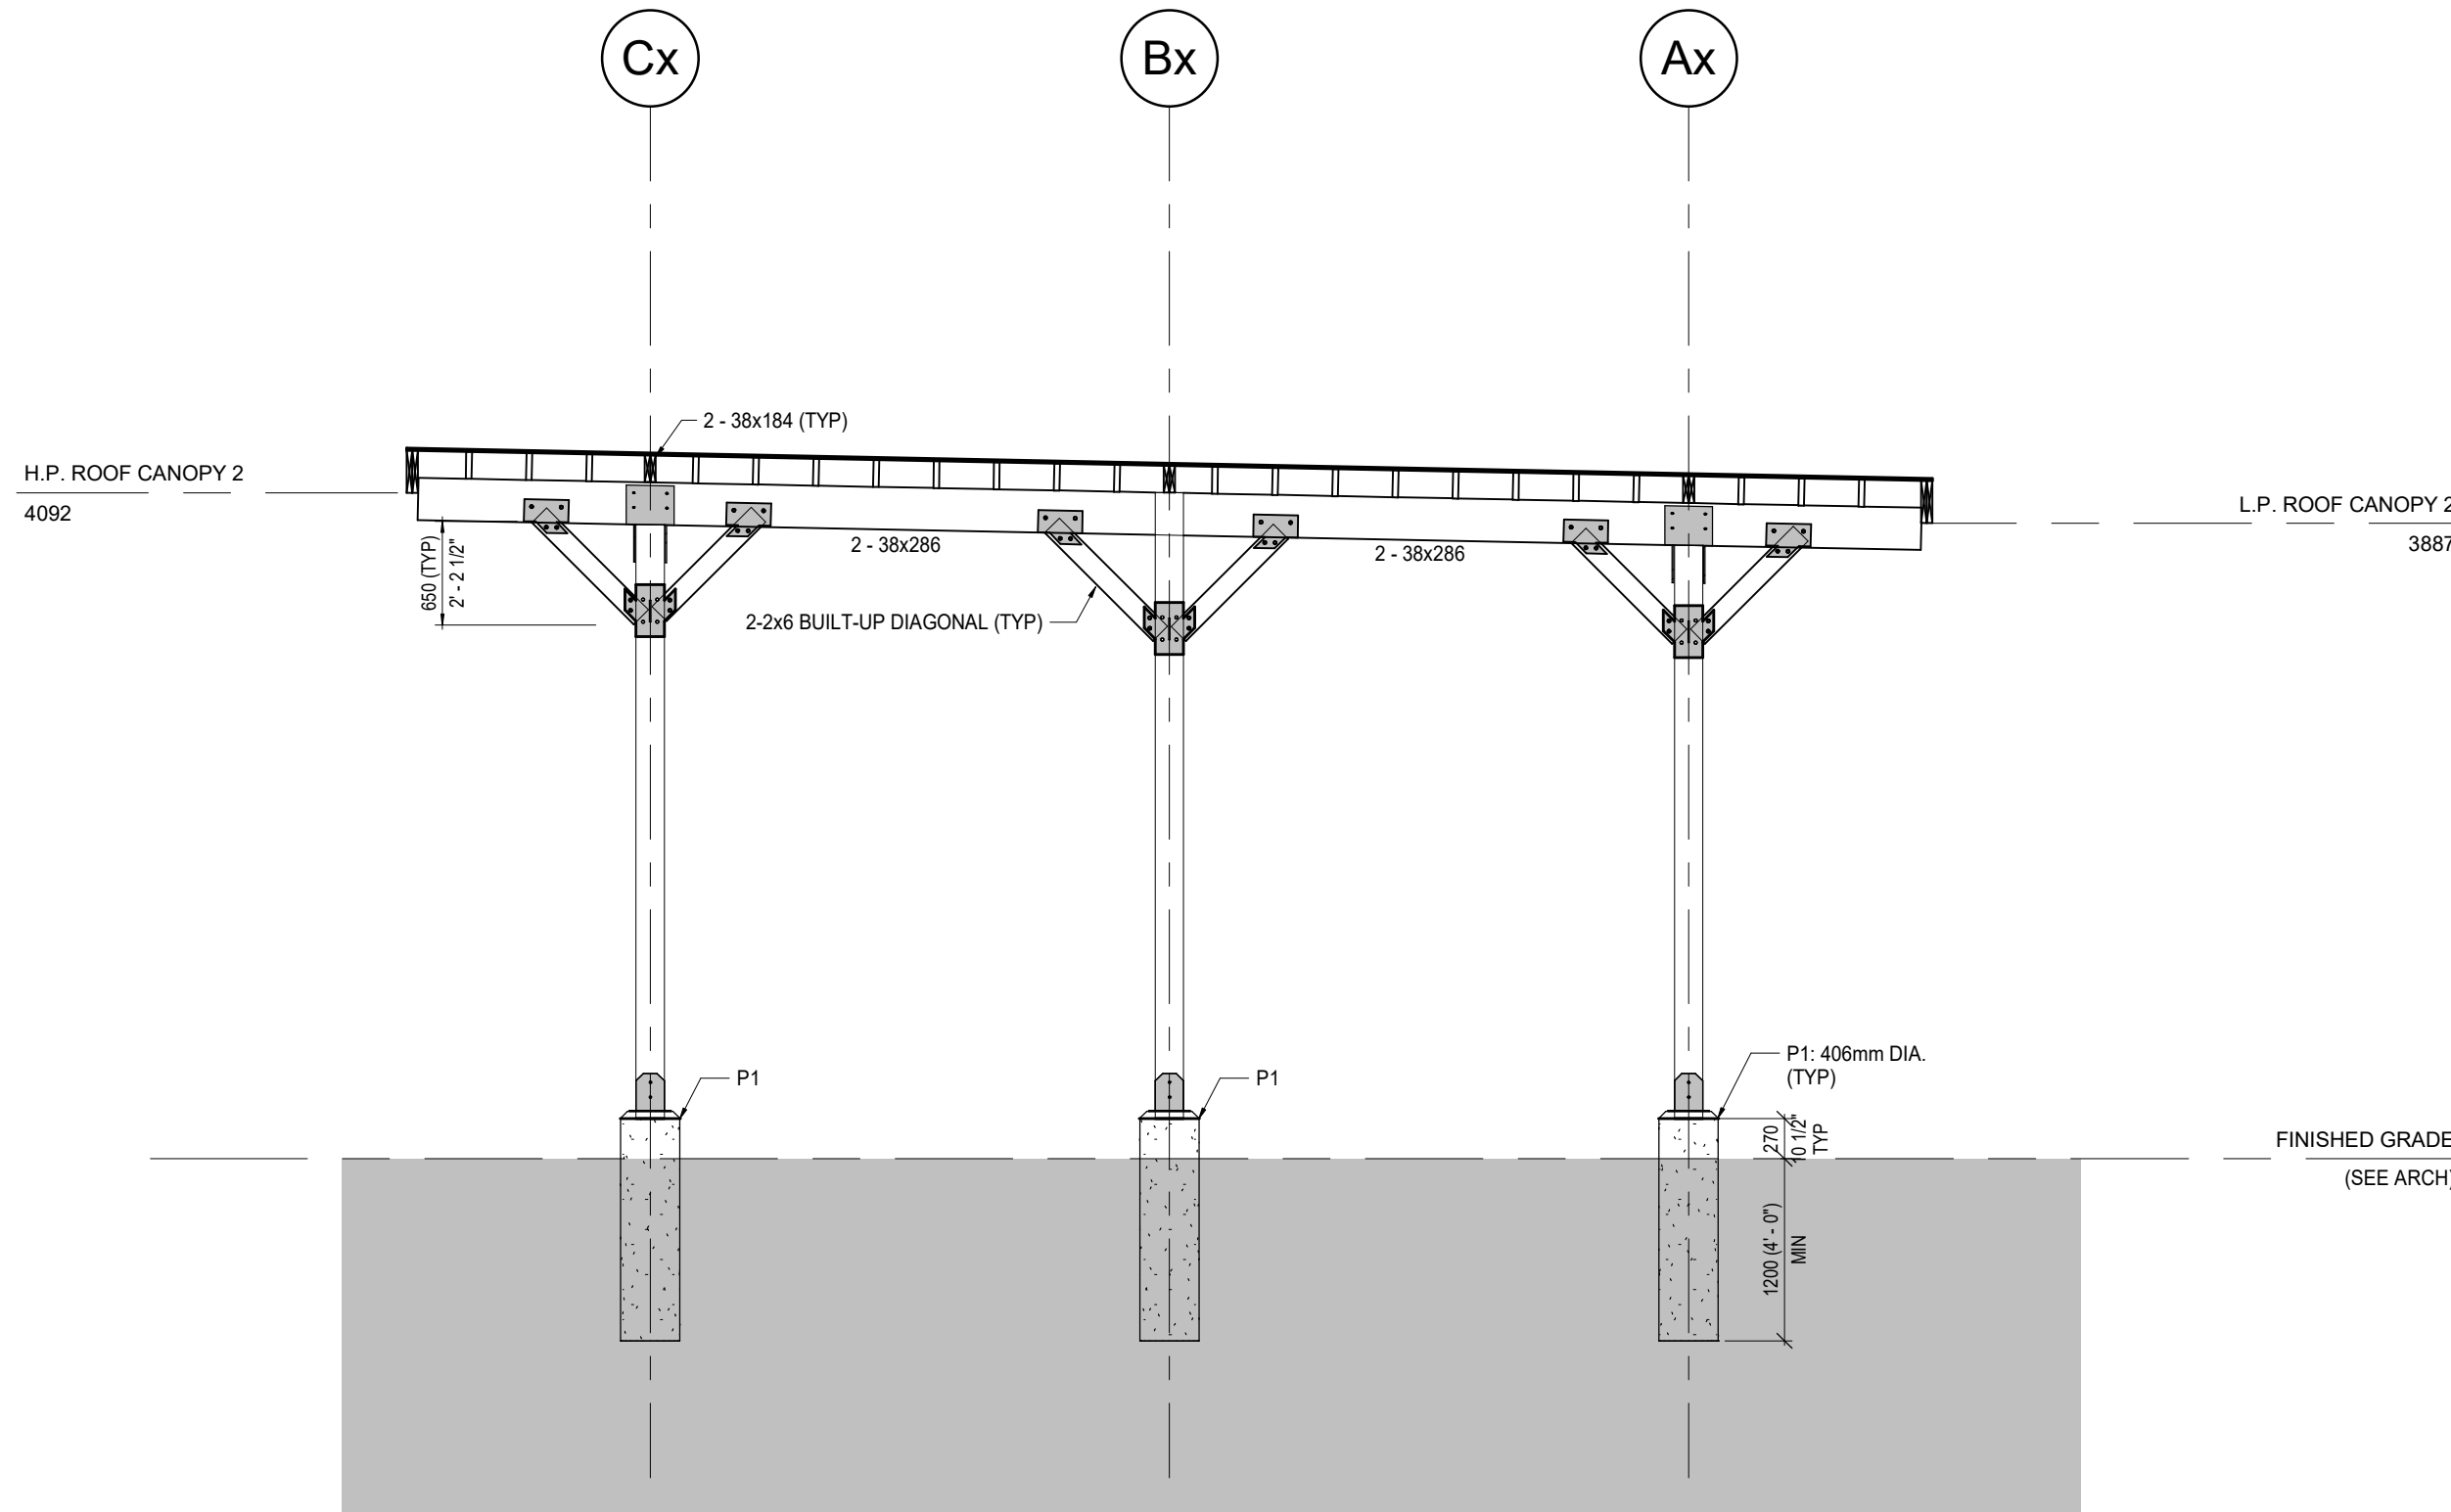

4 SECTION AT G/L 6x  
S401 1 : 50

PLOT DATE: 2025-05-01 8:54:48 AM

PROJECT  
MOHAWK PARK - STORAGE  
CANOPY


P.O. Box 160, 9430 Guelph Line  
Campbellville, Ontario, L0P 1B0

CLIENT  
**WOODBINE™**  
WOODBINE ENTERTAINMENT GROUP  
MOHAWK PARK  
P.O. Box 160, 9430 Guelph Line  
Campbellville, Ontario, L0P 1B0

ARCHITECT  
**PA**  
architects inc.  
143 Seale Ave. Toronto, ON M5H 4B2, Canada  
t 416.961.8254 e pa-architects@outlook.com

CONSULTANT  
**Quinn Dressel**  
ASSOCIATES  
CONSULTING STRUCTURAL ENGINEERS  
885 Yonge St. Suite 305 Toronto, Ontario, Canada M4B 1P4  
t 416.961.8254 e qd@quindressel.com www.quindressel.com

THIS DRAWING IS NOT TO BE SCALED.  
REFER TO APPROPRIATE SURVEY, STRUCTURAL, MECHANICAL,  
ELECTRICAL, LANDSCAPE, ETC. CONSULTANT DRAWINGS BEFORE  
PROCEEDING WITH THE WORK.  
CONSTRUCTION MUST CONFORM TO ALL APPLICABLE CODES AND  
REQUIREMENTS OF AUTHORITIES HAVING JURISDICTION.  
THE CONTRACTOR WORKING FROM DRAWINGS NOT SPECIFICALLY  
MARKED "FOR CONSTRUCTION" MUST ASSUME FULL  
RESPONSIBILITY AND BEAR COSTS FOR ANY CORRECTIONS OR  
DAMAGES RESULTING FROM THEIR WORK.  
THIS DRAWING, AS AN INSTRUMENT OF SERVICE, IS PROVIDED BY  
AND IS THE PROPERTY OF THE ARCHITECT.  
THE CONTRACTOR SHALL VERIFY AND ACCEPT RESPONSIBILITY  
FOR ALL DIMENSIONS AND CONDITIONS ON SITE AND SHALL NOTIFY  
THE APPROPRIATE CONSULTANT OF ANY VARIATIONS FROM THE  
SUPPLIED INFORMATION.

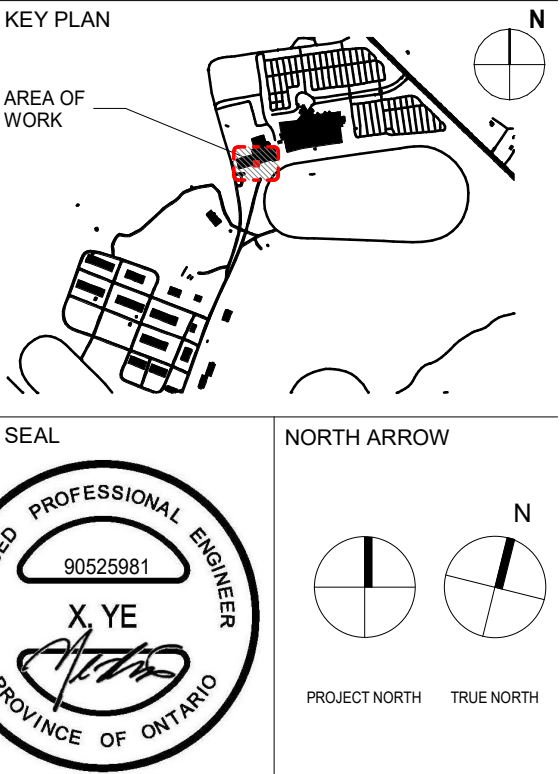

| REVISIONS |      |             |
|-----------|------|-------------|
| No.       | Date | Description |


|   |            |                          |
|---|------------|--------------------------|
| 4 | 2025-04-30 | ISSUED FOR ADDENDUM S01  |
| 3 | 2025-04-28 | ISSUED FOR PERMIT TENDER |
| 2 | 2024-08-21 | ISSUED FOR TENDER ADD 02 |
| 1 | 2024-05-08 | ISSUED FOR COSTING       |

| No.              | Date | Description     |
|------------------|------|-----------------|
| ISSUED:          |      |                 |
| DRAWN BY: XS     |      | REVIEWED BY: RY |
| DATE: Issue Date |      | SCALE: 1 : 50   |
| PROJECT NO.:     |      | 24-055          |
| SHEET TITLE      |      |                 |


SECTIONS

| SHEET NUMBER: | REVISION NO. |
|---------------|--------------|
| S401          | 4            |


PA ARCHITECTS INC. 2024©

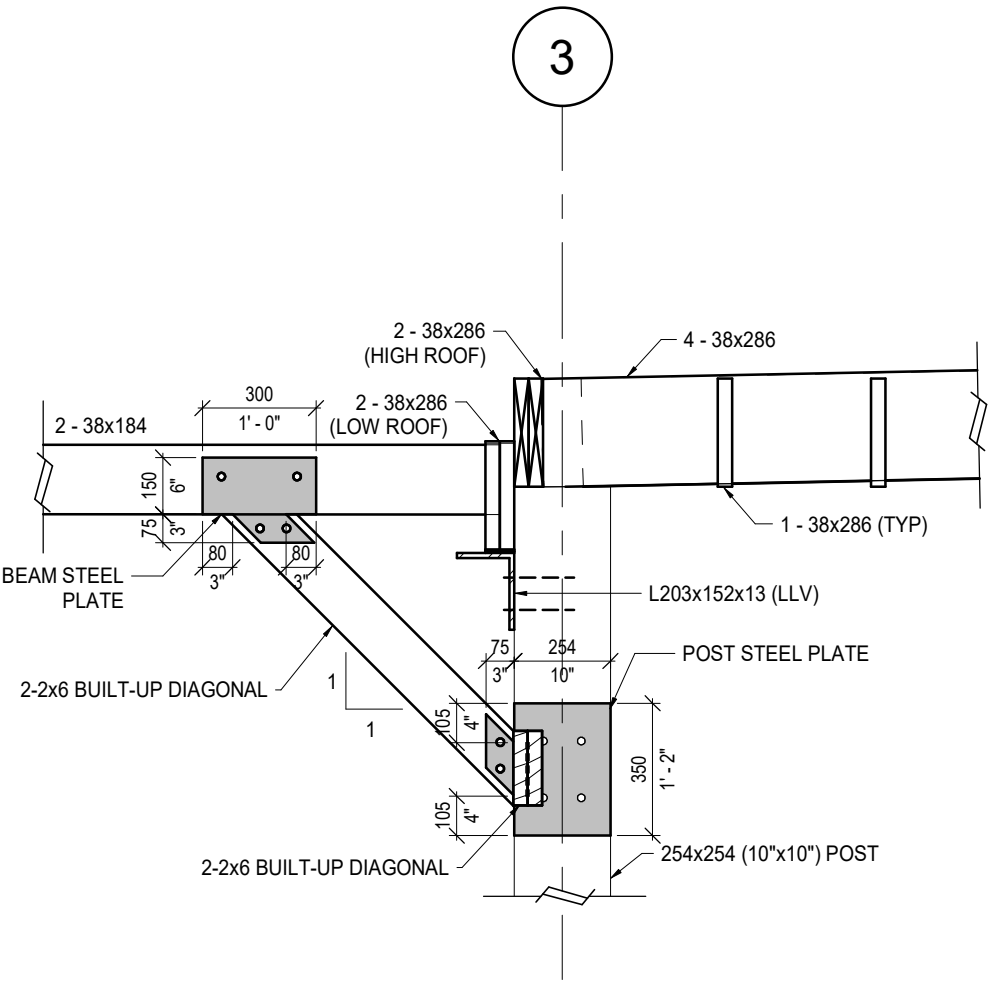


1A SECTION  
S402 1 : 20

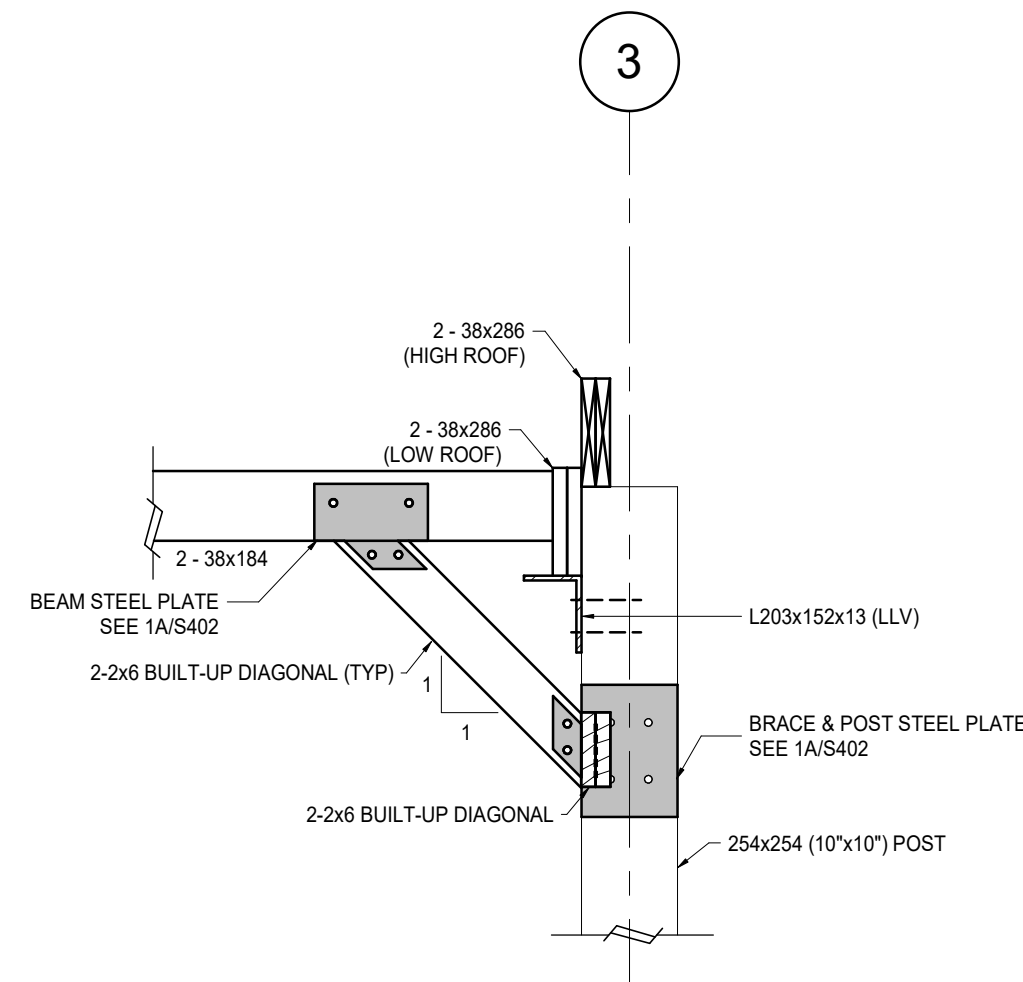


1B SECTION  
S402 1 : 20

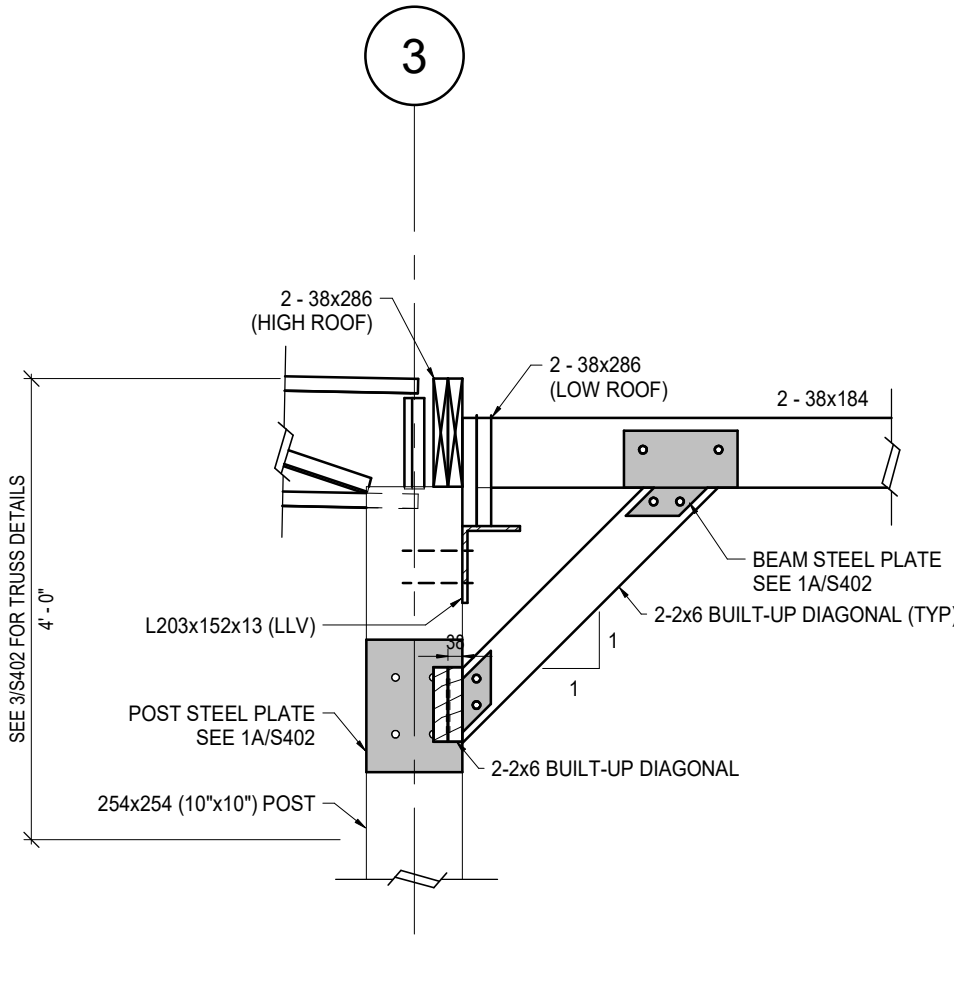


1C SECTION  
S402 1 : 20

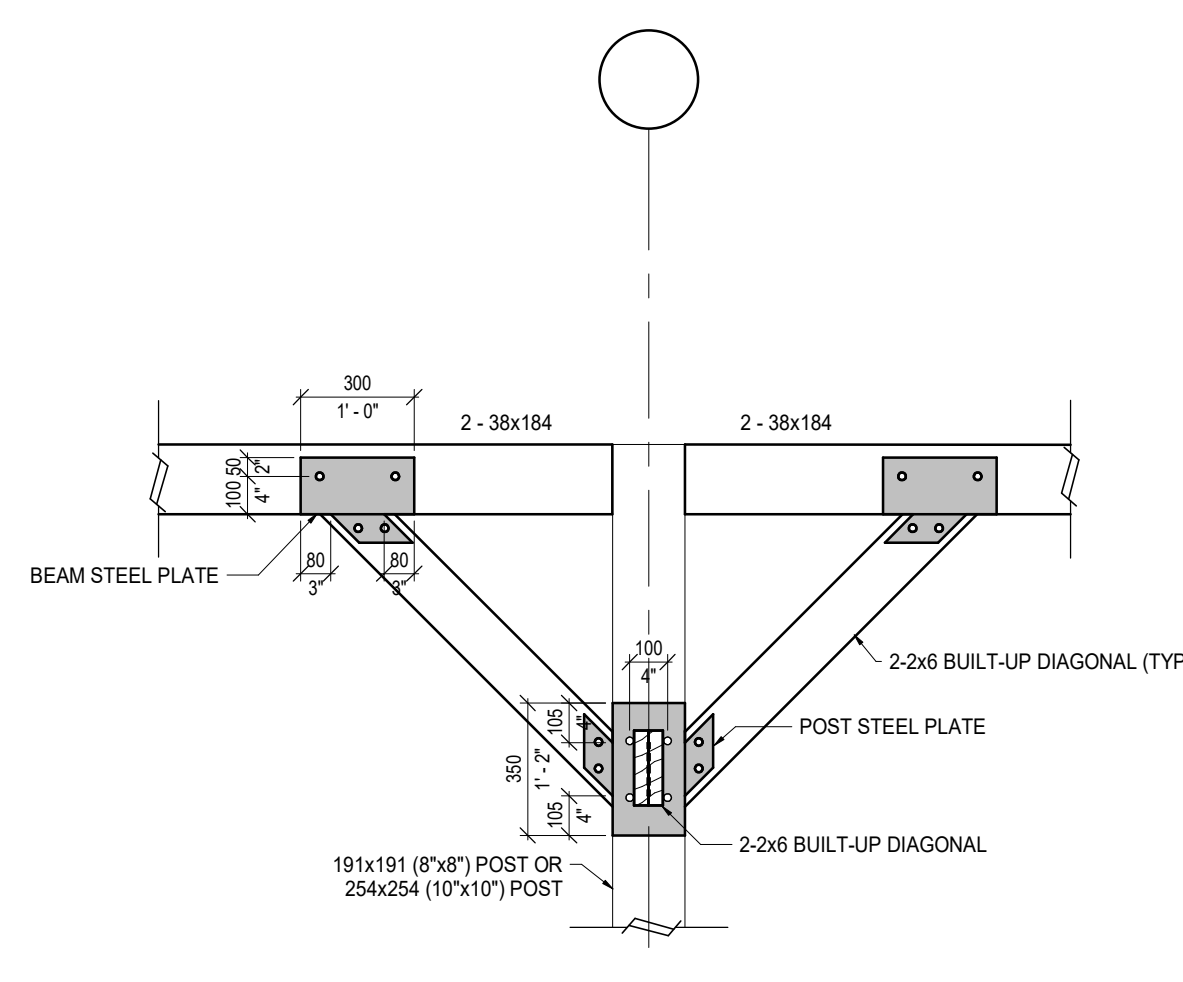

1D POST AND BEAM BRACE STEEL PLATE TYPICAL  
S402 1 : 20

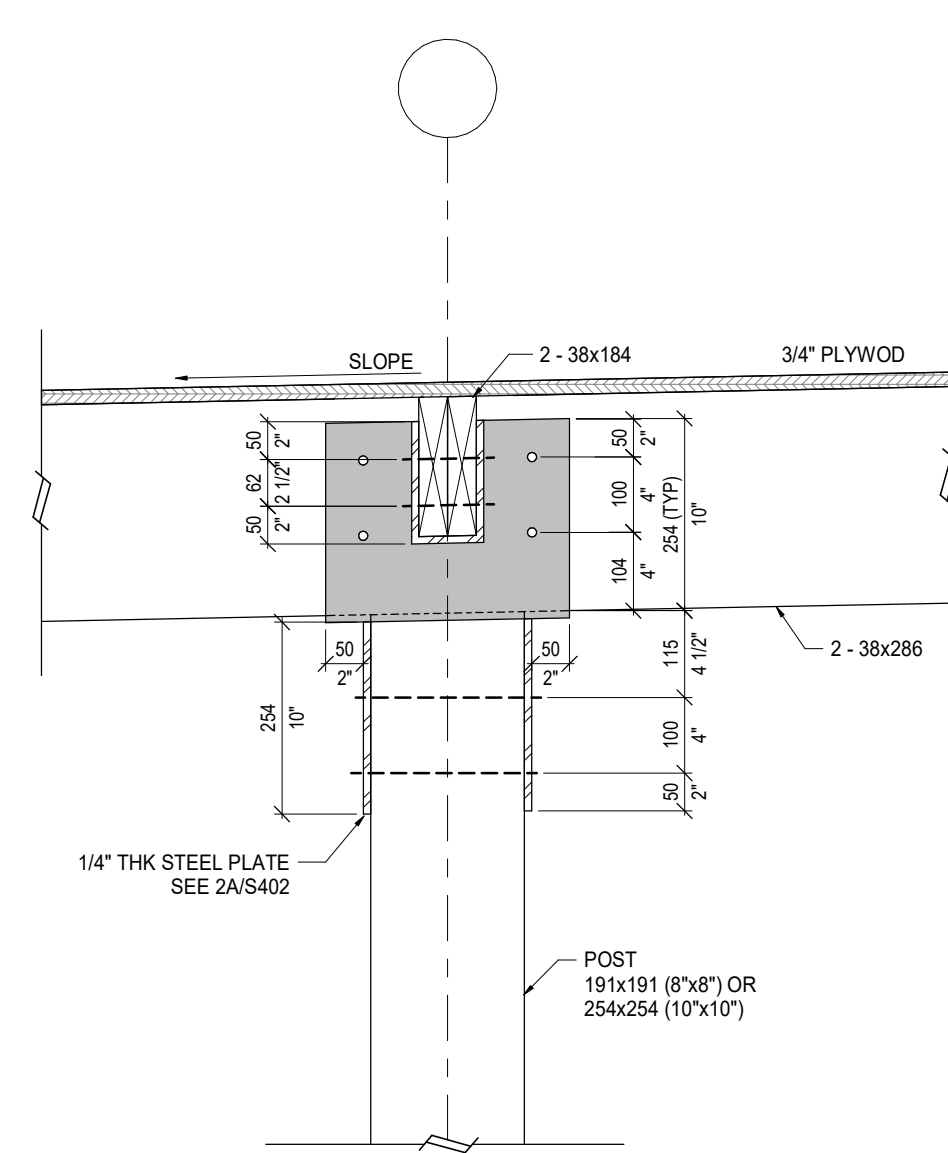


2 SECTION  
S402 1 : 10

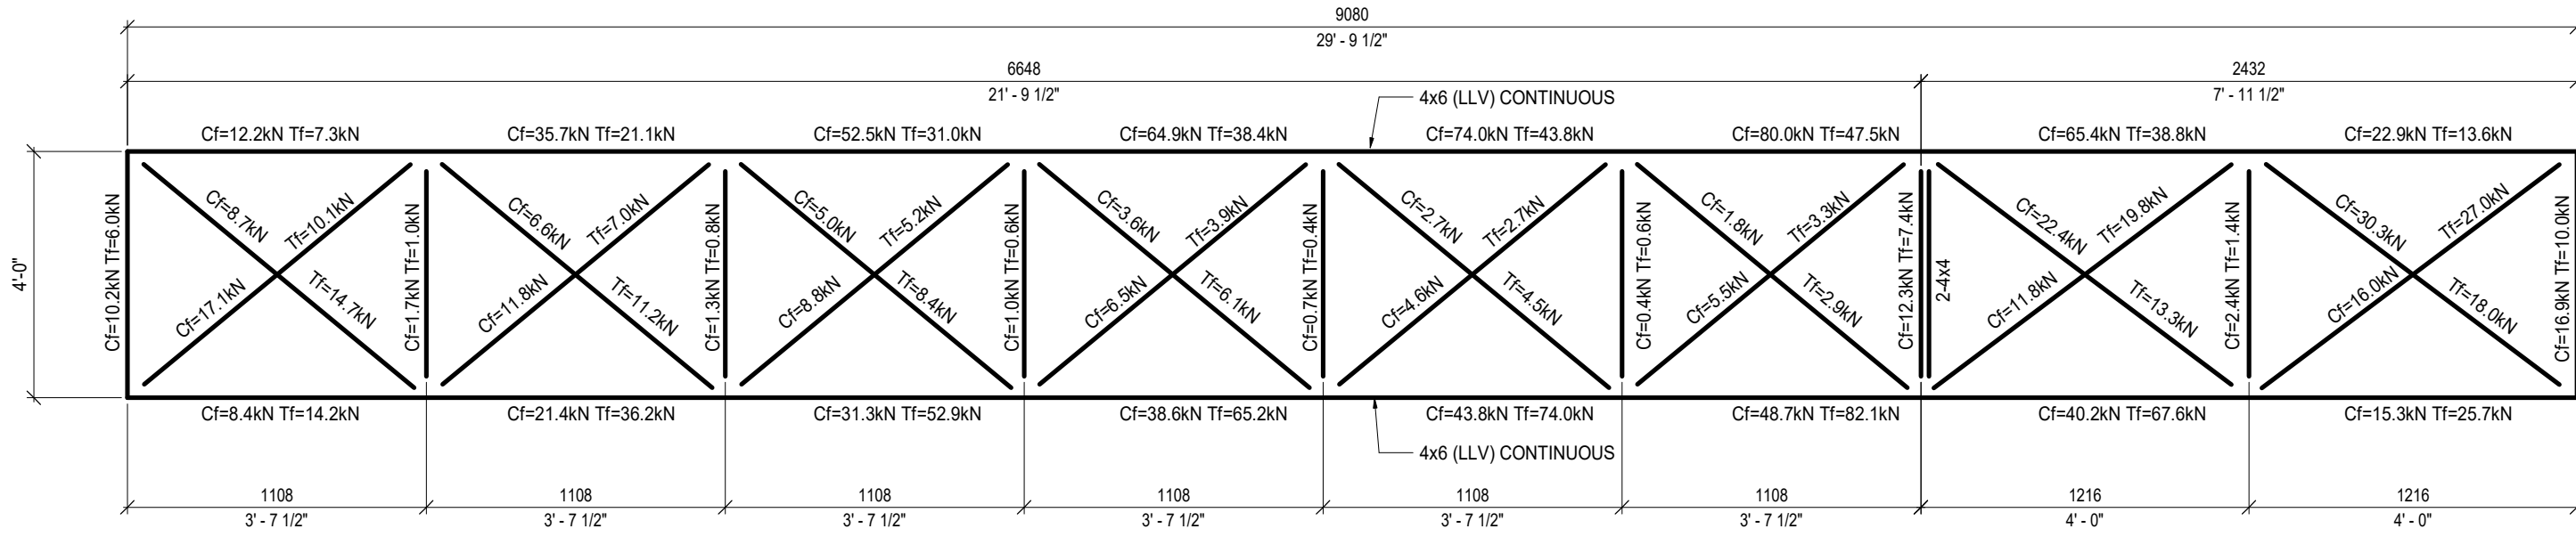


3 ELEVATION AT TRUSS  
S402 1 : 25


- NOTES:
- ALL MEMBERS ARE 4x4 SPF GRADE S5 PRESSURE TREATED SAWN LUMBER (TYPICAL U.O.C.).
  - TRUSS SUPPLIER TO DESIGN THE WOOD TRUSS AND PROVIDE SHOP DRAWINGS WITH P. ENG. STAMP.
  - FEATURE WOOD TRUSS. STAMP FOR REVIEW.
  - MAX ALLOWED DEFLECTION  $\leq 2"$  (51mm).

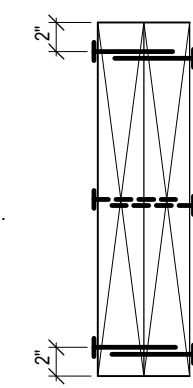

2-PLY WOOD JOIST NAIL ARRANGEMENT  
10x(3") COMMON WIRE NAIL@12" O.C.

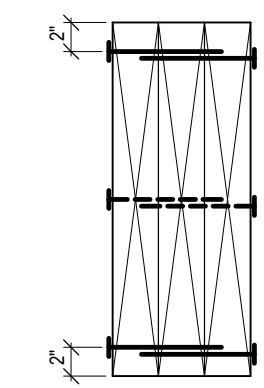


3-PLY WOOD JOIST NAIL ARRANGEMENT  
16x(3-12") COMMON WIRE NAIL@12" O.C.

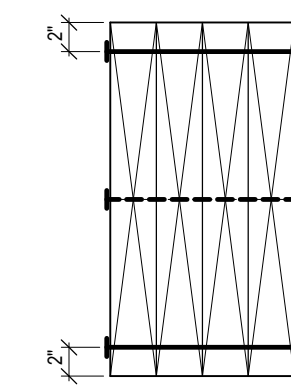


4-PLY OR 5-PLY WOOD JOIST NAIL CONNECTION  
1/2" A307 THROUGH BOLTS @ 12" O.C.



4 WOOD JOIST BUILT-UP MEMBER  
S402 1 : 50

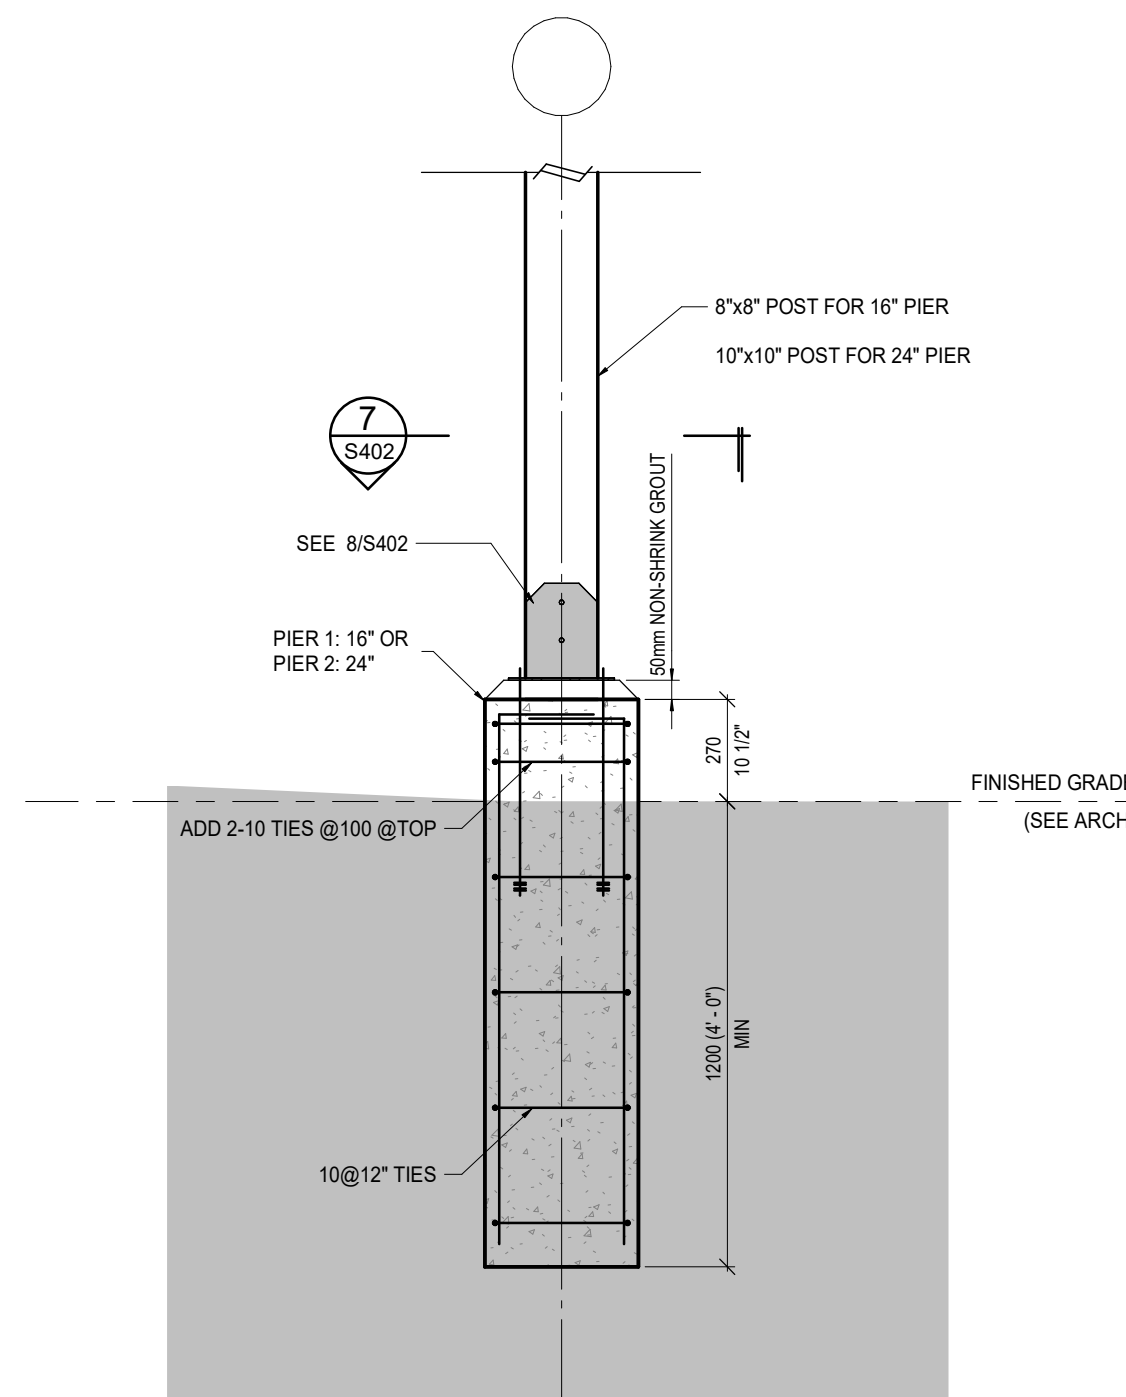

6 CONCRETE PIER & POST ELEVATION (TYPICAL)  
S402 1 : 20

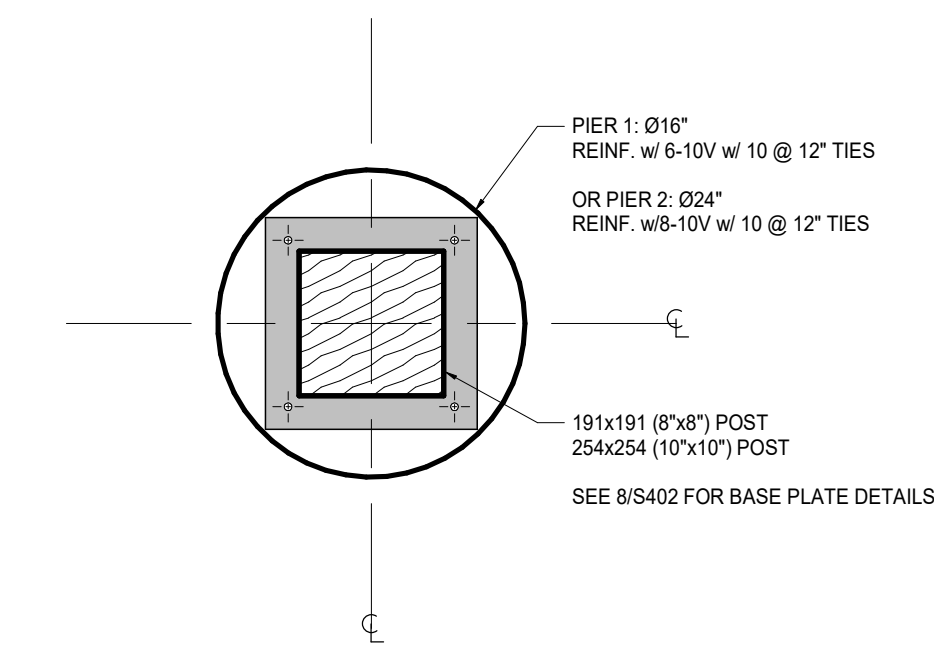


7 CONCRETE PIER & POST PLAN  
S402 1 : 10

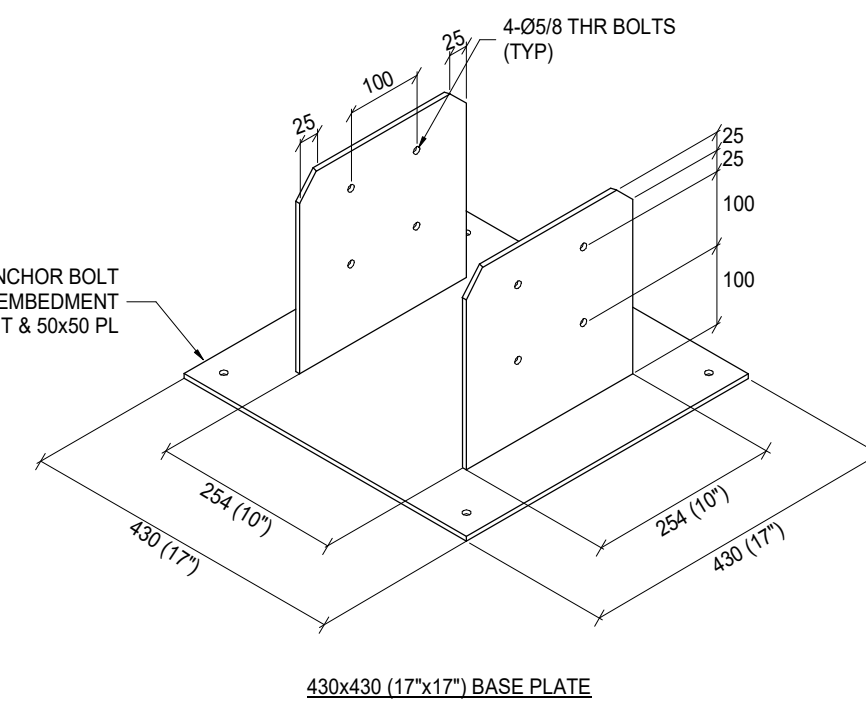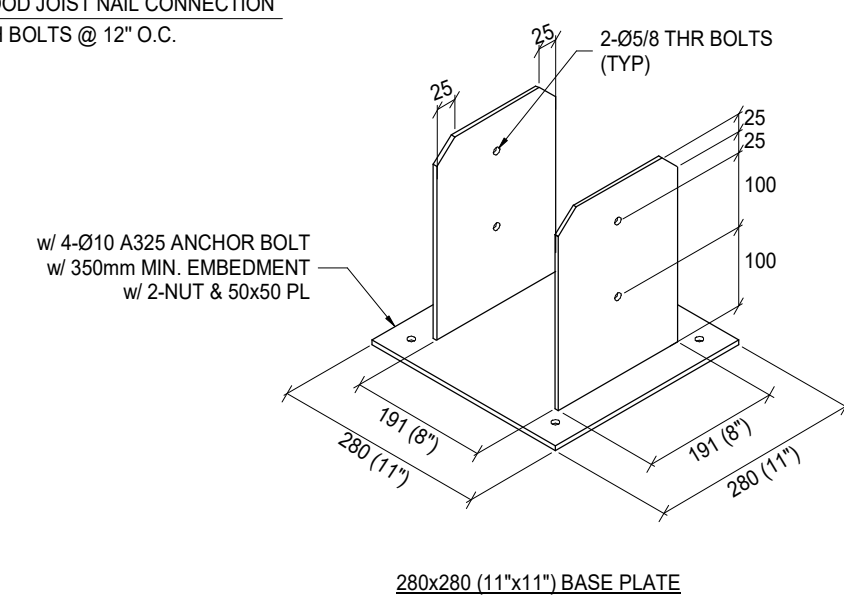



8 BASE PLATE DETAILS  
S402 1 : 10

- NOTE:
- ALL PLATES ARE 10mm (3/8") THICK.

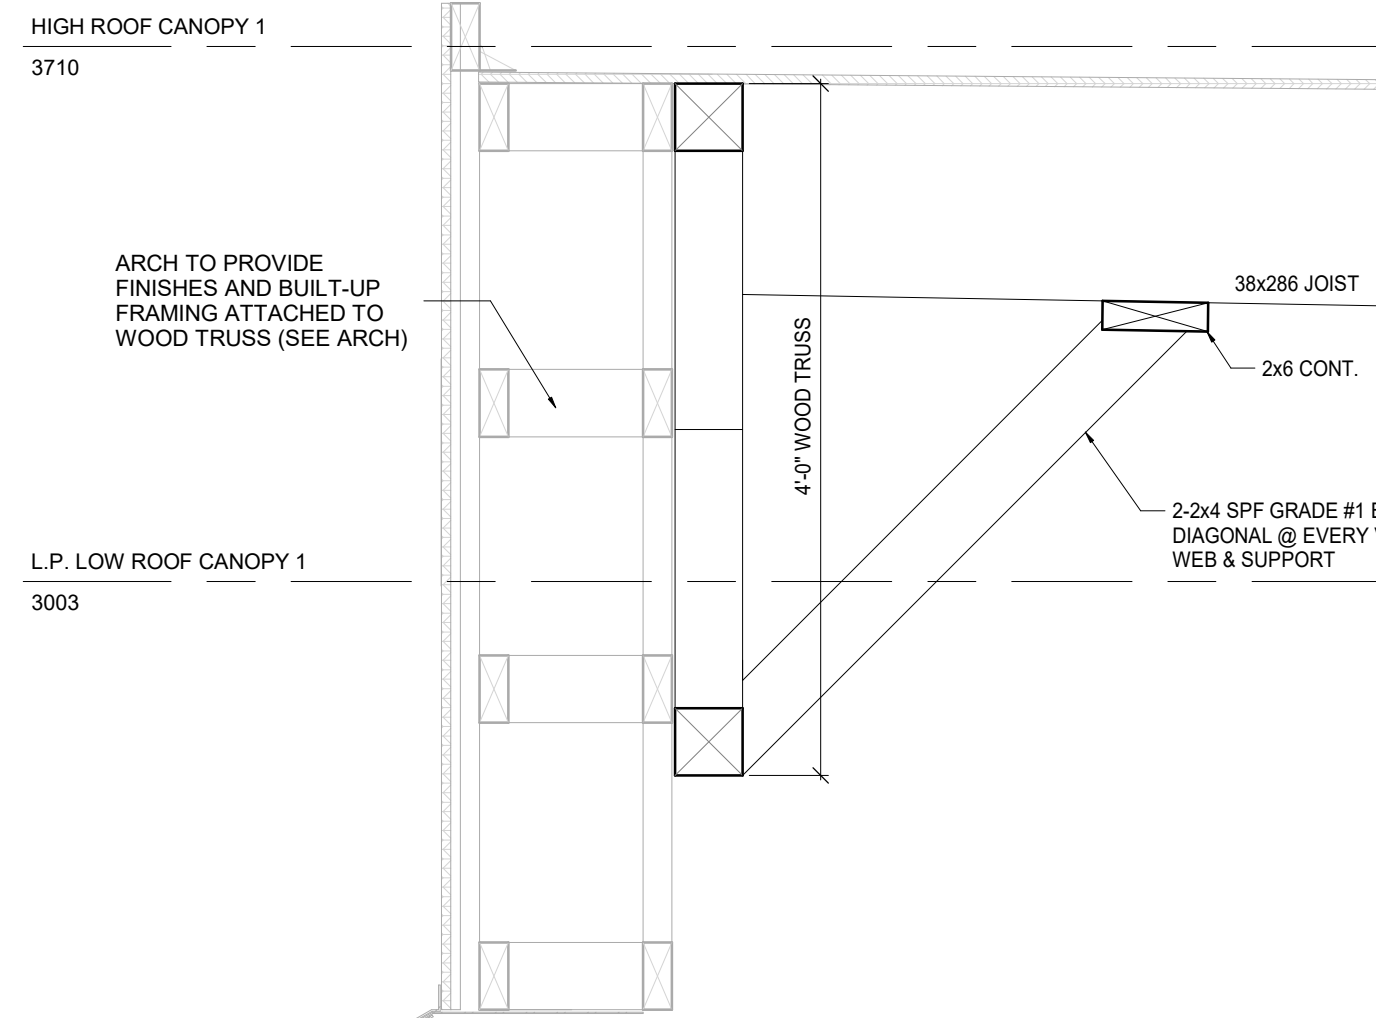


5 SECTION AT WOOD TRUSS  
S402 1 : 10

2A TYPICAL POST & BEAM CONNECTION STEEL PLATE  
S402 1 : 10

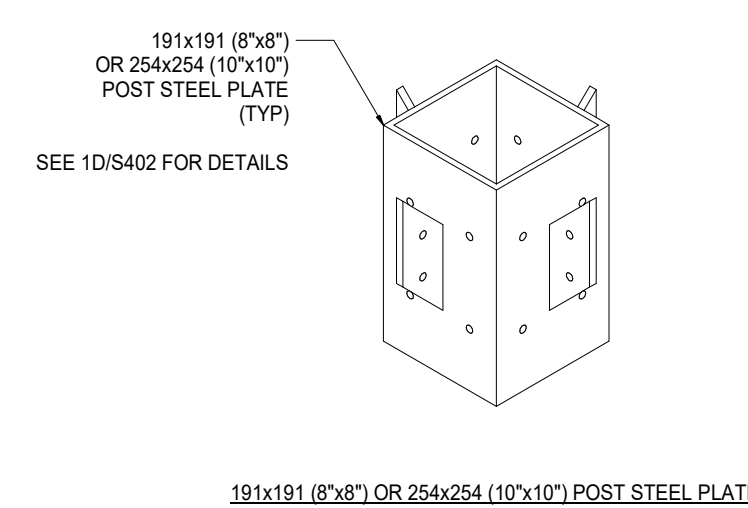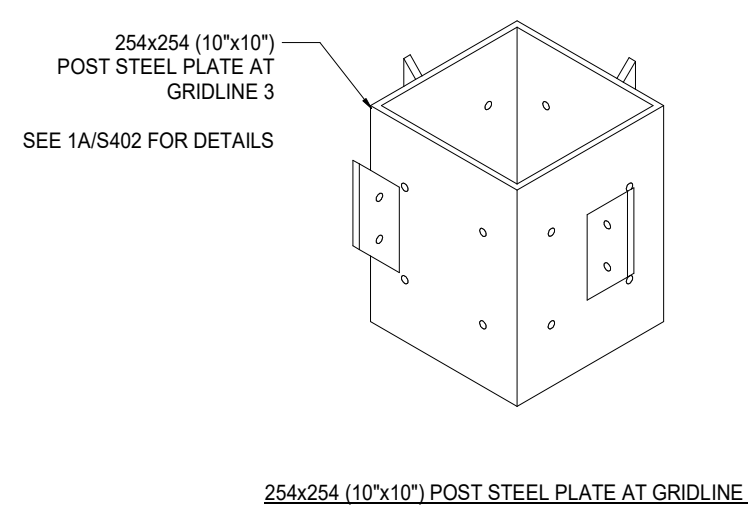

9 TYPICAL BRACE STEEL PLATE  
S402 1 : 10

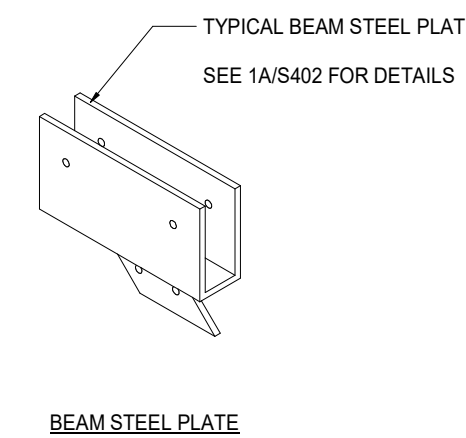

PROJECT  
MOHAWK PARK - STORAGE  
CANOPY

P.O. Box 160, 9430 Guelph Line  
Campbellville, Ontario, L0P 1B0

CLIENT




WOODBINE ENTERTAINMENT GROUP  
MOHAWK PARK  
P.O. Box 160, 9430 Guelph Line  
Campbellville, Ontario, L0P 1B0

ARCHITECT




143 Spadina Ave. Toronto, ON M5S 4E2, Canada  
t: 416.961.8254 e: dr@pa-architects.com

CONSULTANT

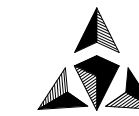

Quinn Dressel  
ASSOCIATES  
CONSULTING STRUCTURAL ENGINEERS  
880 Yonge St. Suite 303 Toronto, Ontario, Canada M4B 1P4  
t: 416.961.8254 e: qd@quindressel.com

THIS DRAWING IS NOT TO BE SCALED.  
REFER TO APPROPRIATE SURVEY, STRUCTURAL, MECHANICAL,  
ELECTRICAL, LANDSCAPE, ETC. CONSULTANT DRAWINGS BEFORE  
PROCEEDING WITH THE WORK.  
CONSTRUCTION MUST CONFORM TO ALL APPLICABLE CODES AND  
REQUIREMENTS OF AUTHORITIES HAVING JURISDICTION.  
THE CONTRACTOR WORKING FROM DRAWINGS NOT SPECIFICALLY  
MARKED "FOR CONSTRUCTION" MUST ASSUME FULL  
RESPONSIBILITY AND BEAR COSTS FOR ANY CORRECTIONS OR  
DAMAGES RESULTING FROM THEIR WORK.  
THIS DRAWING, AS AN INSTRUMENT OF SERVICE IS PROVIDED BY  
AND IS THE PROPERTY OF THE ARCHITECT.  
THE CONTRACTOR SHALL VERIFY AND ACCEPT RESPONSIBILITY  
FOR ALL DIMENSIONS AND CONDITIONS ON SITE AND SHALL NOTIFY  
THE APPROPRIATE CONSULTANT OF ANY VARIATIONS FROM THE  
SUPPLIED INFORMATION.

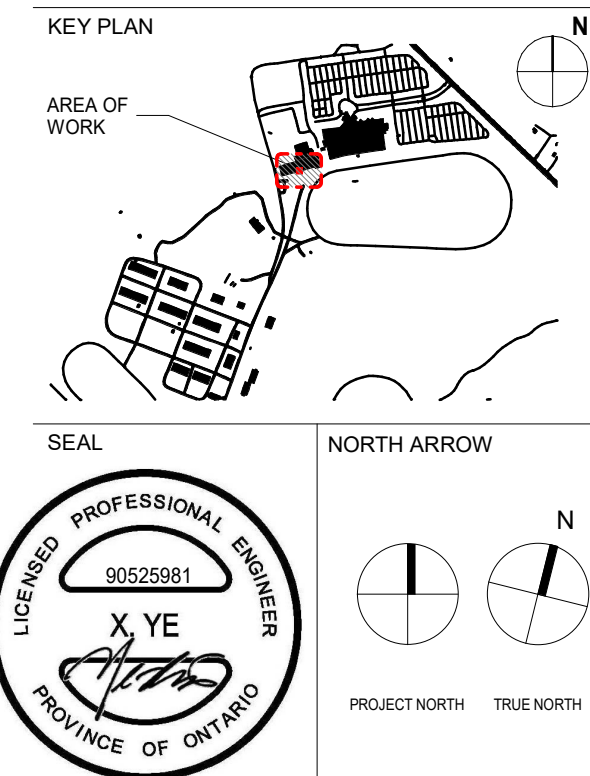

| REVISIONS |      |             |
|-----------|------|-------------|
| No.       | Date | Description |

|   |            |                          |
|---|------------|--------------------------|
| 4 | 2025-04-30 | ISSUED FOR ADDENDUM S01  |
| 3 | 2025-04-28 | ISSUED FOR PERMIT TENDER |
| 2 | 2024-08-21 | ISSUED FOR TENDER ADD 02 |
| 1 | 2024-05-08 | ISSUED FOR COSTING       |

| No.                 | Date | Description         |
|---------------------|------|---------------------|
| ISSUED:             |      |                     |
| DRAWN BY: XS        |      | REVIEWED BY: RY     |
| DATE: Issue Date    |      | SCALE: As Indicated |
| PROJECT NO.: 24-055 |      |                     |
| SHEET TITLE         |      |                     |

SECTIONS AND DETAILS

|               |              |
|---------------|--------------|
| SHEET NUMBER: | REVISION NO. |
| S402          | 4            |